

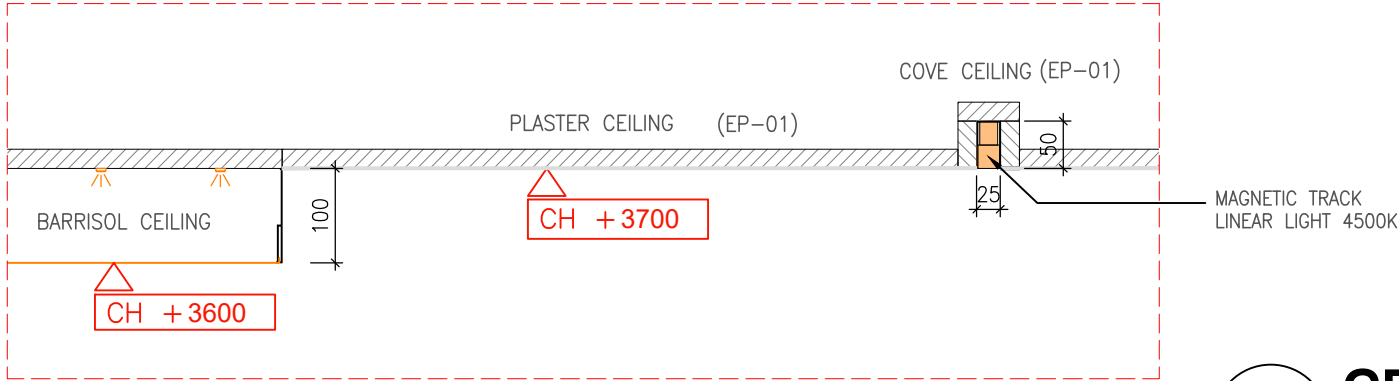


Rev	Date	Description
Client:		
Project:		
FRAN @ BUGIS+ (#01-04)		
Project Management:		
 Studio J Solutions Pte. Ltd.		
email : enquiries@studioj.sg web : www.studioj.sg Add : 7 Mandal Link #03-20 Mandal Connection Singapore 728653		
Design Consultant:		
Main Contractor:		
 Studio J Solutions Pte. Ltd.		
email : enquiries@studioj.sg web : www.studioj.sg Add : 7 Mandal Link #03-20 Mandal Connection Singapore 728653		
Mechanical & Electrical Consultant:		
Structural Engineer:		
General Notes:		
COPYRIGHT OF ALL DESIGNS AND DATA SHOWN IN THIS DRAWING IS RETAINED BY STUDIO J SOLUTION PTE.LTD. WRITTEN PERMISSION IS REQUIRED FOR ANY USE AND/OR REPRODUCTION. ALL PRINTS, SPECIFICATIONS AND COPYRIGHTS ARE THE PROPERTY OF STUDIO J SOLUTION PTE.LTD. AND SHALL BE RETURNED ON COMPLETION OF WORKS. ALL MEASUREMENTS MUST BE CHECKED AT SITE BY THE CONTRACTOR AND NOTIFICATION TO BE MADE TO THE DESIGNER BEFORE COMMENCEMENT OF WORK. IN THE EVENT OF ANY DISCREPANCIES ARISING FROM THE DRAWINGS, ALL DRAWINGS MUST BE READ IN CONJUNCTION WITH OTHER CONSULTANT DRAWINGS.		
Drawn :		
WILLIAM		
Checked:		
JF		
Approved:		
First submission date:		
Scale :		
A3 AS SHOWN		
Drawing Title:		
CEILING PLAN		
Drawing Number:		
PL-05		
Project Number:		
FRAN_BUGIS+_020726		

LEGEND:		
SYMBOL	DESCRIPTION	CODE
	OPEN CEILING BLACK EMULSION PAINT FIN; CH + 4000	EP-02
	PLASTER CEILING WHITE EMULSION PAINT FIN; CH + 3700	EP-01
	PLASTER CEILING WHITE EMULSION PAINT FIN; CH + 2400	EP-01
	BARRISOL CEILING CH + 3600	
	BARRISOL CEILING CH + 2400	
	COVE CEILING WHITE EMULSION PAINT FIN; CH + 3750	EP-01
	SLANTED LED SCREEN (49 Deg) CH + 2400	
	WHITE PLASTER CEILING CH + 2400	WP-01
	GRAY PLASTER CEILING CH + 3500	WP-02
	GRID CEILING 600X600MM CH + 2400	

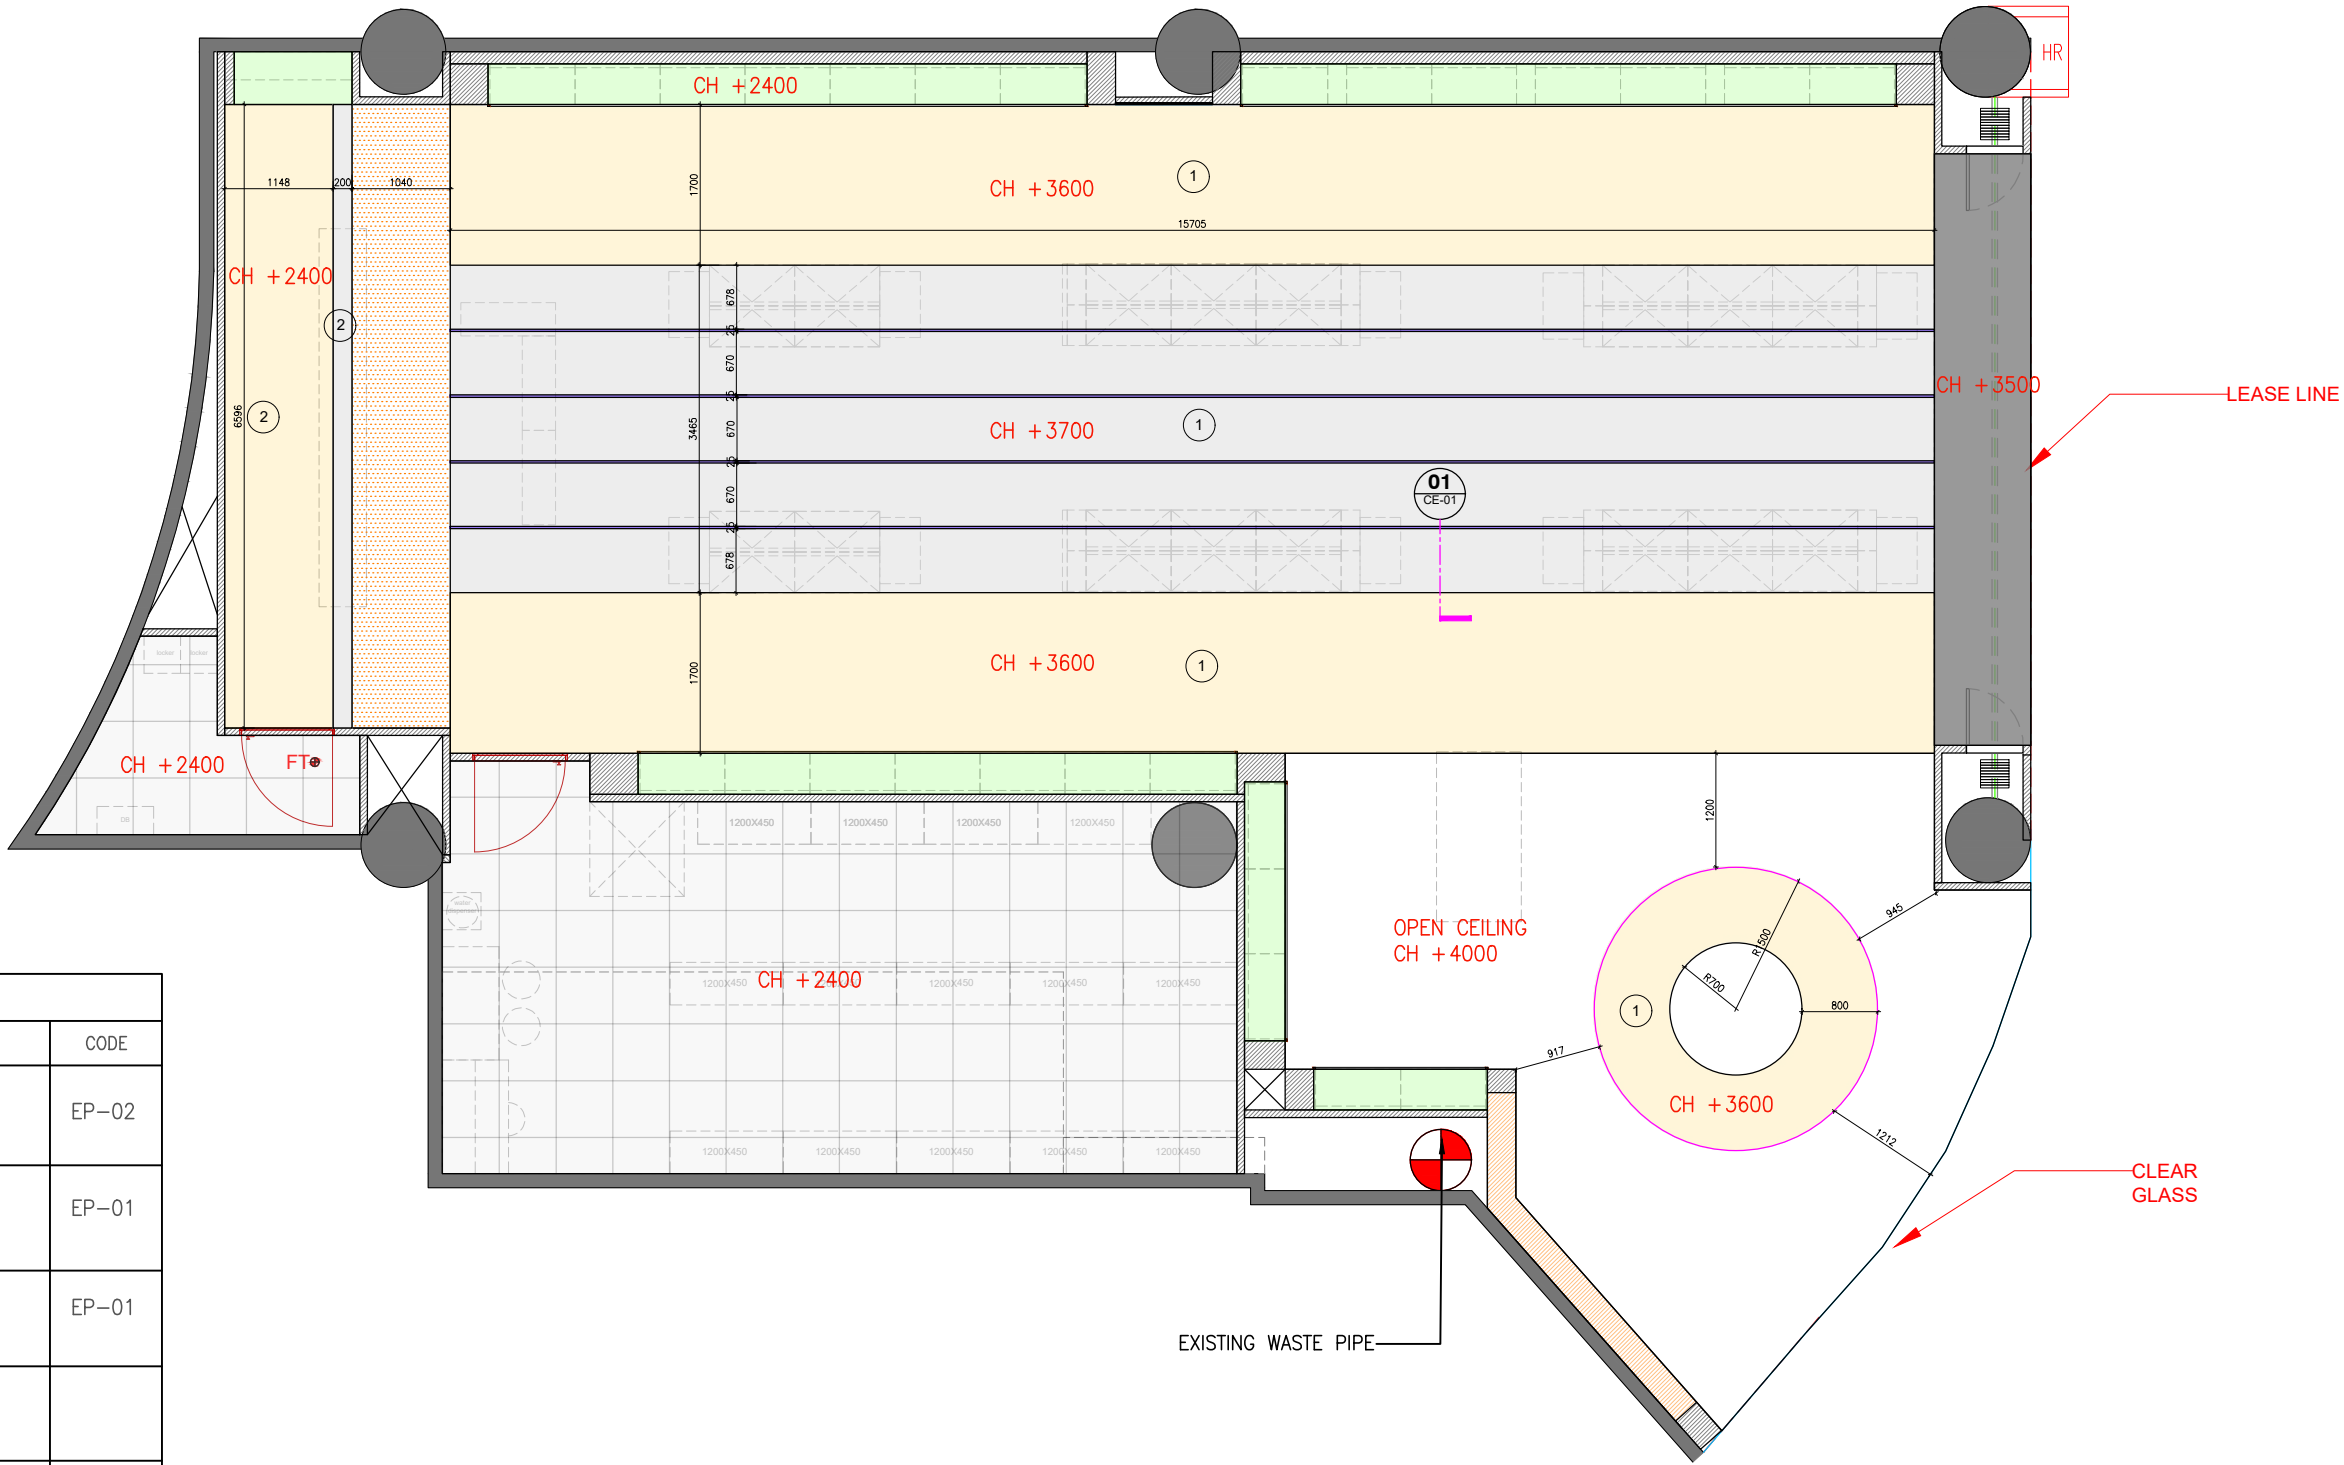

05 CEILING PLAN
SCALE 1 : 80

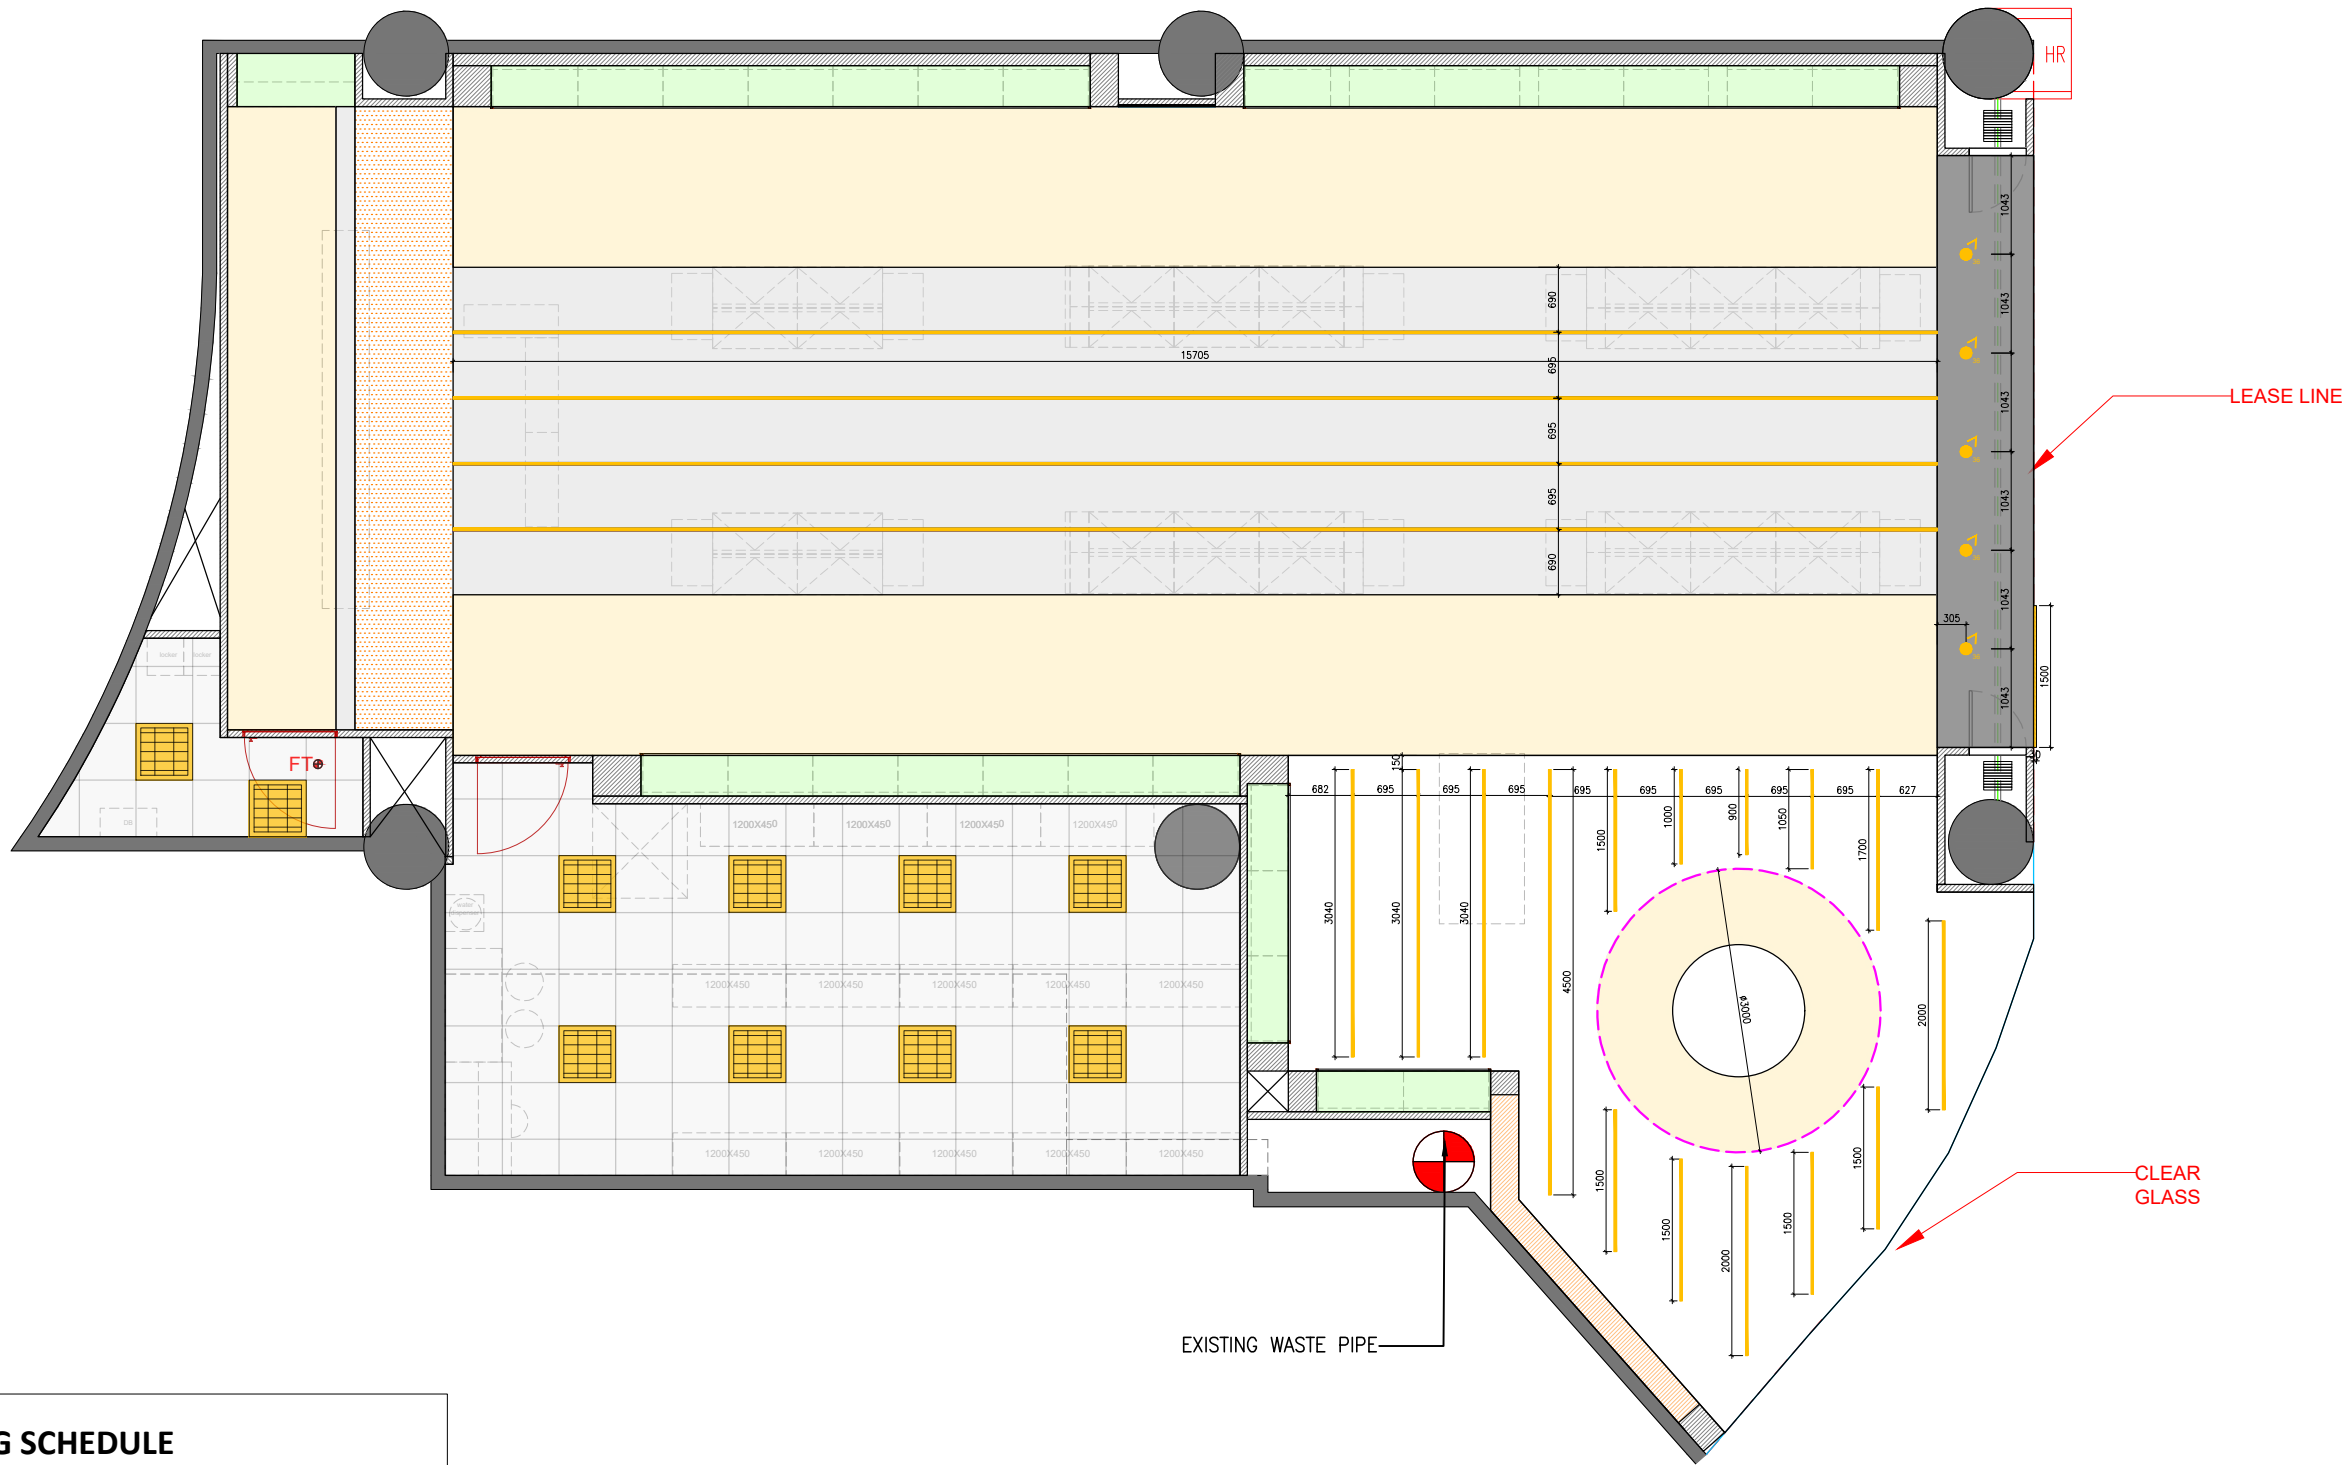

LIGHTING SCHEDULE

TO BE READ IN CONJUNCTION WITH THE ELECTRICAL SPECIFICATION

SYMBOL	CODE	DESCRIPTION	QTY
		Downlight Wide Beam - 4500K - 36deg - 20W	5
		Magnetic Track Linear Light - 4500K	
		600X600 LED PANEL LIGHT 6000K	10
		FRONT LIT FRAN LOGO (6000K) SHOPFRONT	1
		LED PANEL	

06 **LIGHTING PLAN**
SCALE 1 : 80

Rev	Date	Description
Client		
Project :		
FRAN @ BUGIS+ (#01-04)		
Project Management:		
 Studio J Solutions Pte. Ltd.		
email : enquiries@studioj.sg web : www.studioj.sg Add : 7 Mandal Link #03-20 Mandal Connection Singapore 728653		
Design Consultant:		
Main Contractor:		
 Studio J Solutions Pte. Ltd.		
email : enquiries@studioj.sg web : www.studioj.sg Add : 7 Mandal Link #03-20 Mandal Connection Singapore 728653		
Mechanical & Electrical Consultant:		
Structural Engineer:		
General Notes:		
COPYRIGHT OF ALL DESIGNS AND DATA SHOWN IN THIS DRAWING IS RETAINED BY STUDIO J SOLUTION PTE.LTD. WRITTEN PERMISSION IS REQUIRED FOR ANY USE AND/OR REPRODUCTION. ALL PRINTS, SPECIFICATIONS AND COPYRIGHTS ARE THE PROPERTY OF STUDIO J SOLUTION PTE.LTD. AND SHALL BE RETURNED ON COMPLETION OF WORKS. ALL MEASUREMENTS MUST BE CHECKED AT SITE BY THE CONTRACTOR AND NOTIFICATION TO BE MADE TO THE DESIGNER BEFORE COMMENCEMENT OF WORK. IN THE EVENT OF ANY DISCREPANCIES ARISING FROM THE DRAWINGS, ALL DRAWINGS MUST BE READ IN CONJUNCTION WITH OTHER CONSULTANT DRAWINGS.		
Drawn :		
WILLIAM		
Checked:		
JF		
Approved:		
First submission date:		
Scale :		
A3 AS SHOWN		
Drawing Title:		
LIGHTING PLAN		
Drawing Number:		
PL-06		
Project Number:		
FRAN_BUGIS+_020726		

