


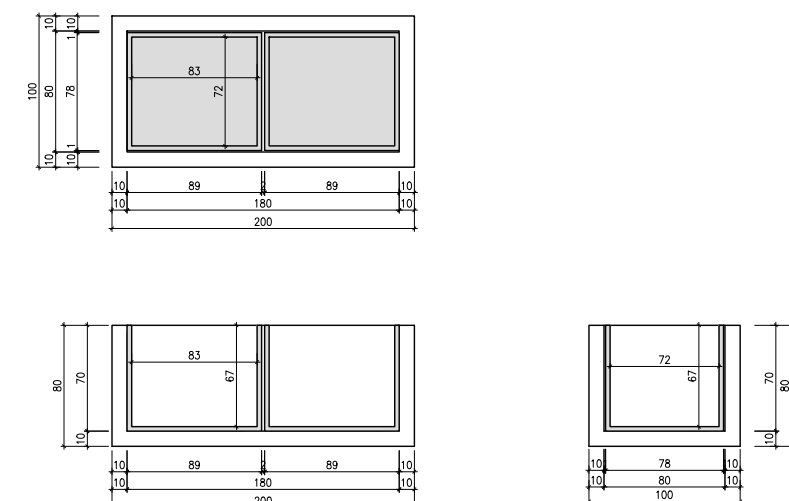
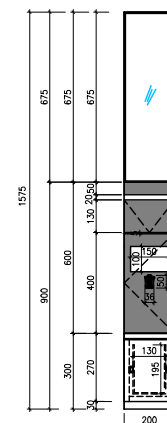
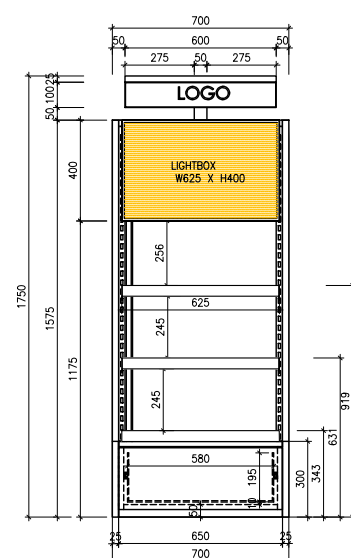
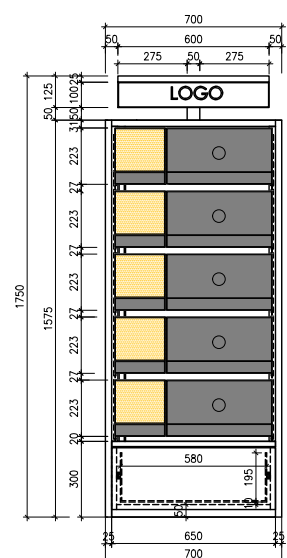
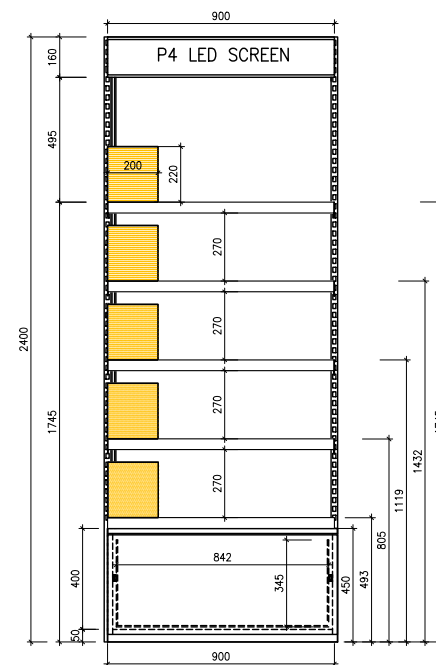
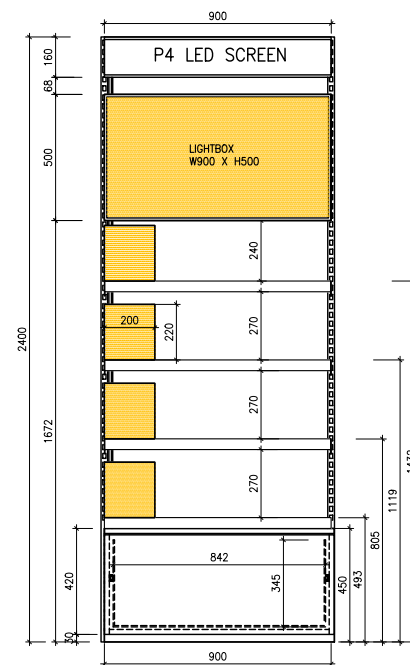
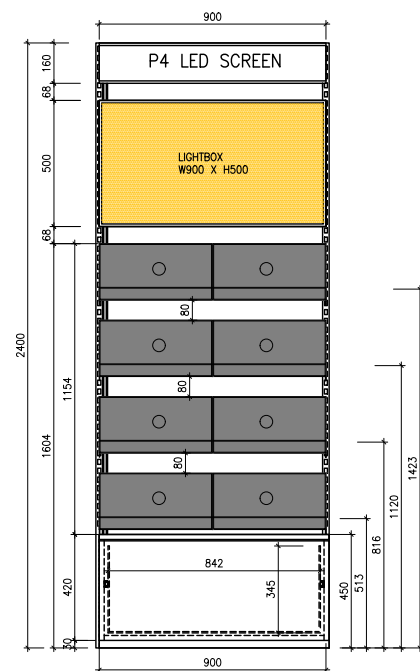
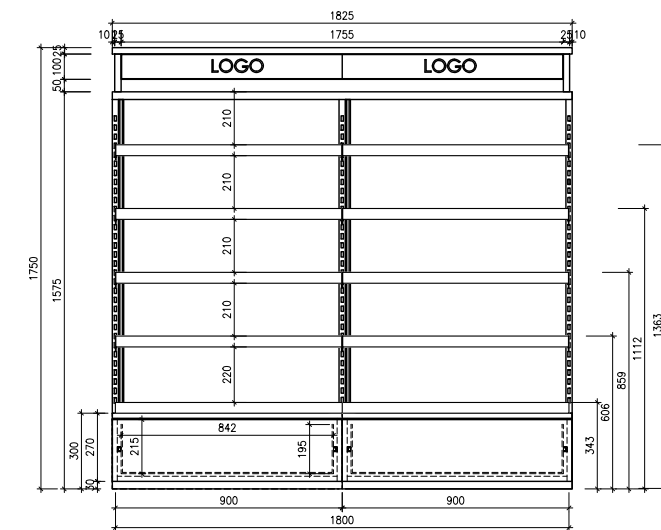
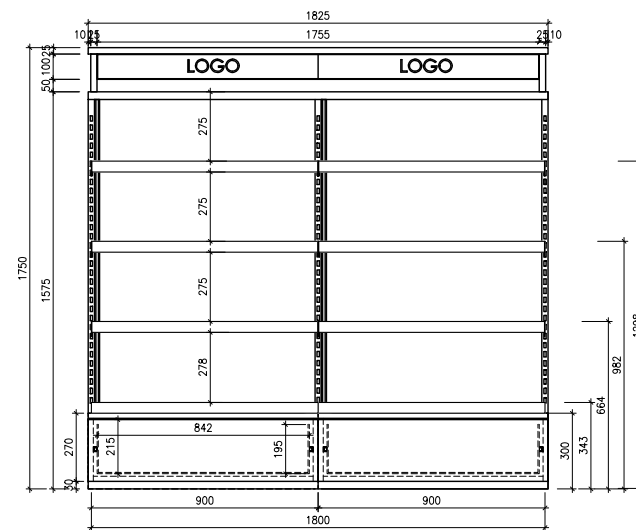


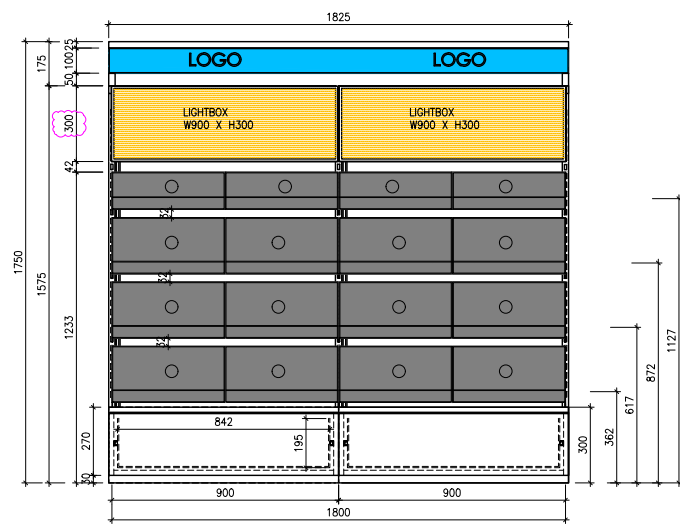


Rev	Date	Description
Client:		
Project :		
FRAN @ BUGIS+ (#01-04)		
Project Management:		
		
Studio J Solutions Pte. Ltd		
email : enquiries@studioj.sg web : www.studioj.sg Add : 7 Mandal Link #03-20 Mandal Connection Singapore 728653		
Design Consultant:		
Main Contractor:		
		
Studio J Solutions Pte. Ltd		
email : enquiries@studioj.sg web : www.studioj.sg Add : 7 Mandal Link #03-20 Mandal Connection Singapore 728653		
Mechanical & Electrical Consultant:		
Structural Engineer:		
General Notes:		
COPYRIGHT OF ALL DESIGNS AND DATA SHOWN IN THIS DRAWING IS RETAINED BY STUDIO J SOLUTION PTE.LTD. WRITTEN PERMISSION IS REQUIRED FOR ANY USE AND/OR REPRODUCTION. ALL PRINTS, SPECIFICATIONS AND COPYRIGHTS ARE THE PROPERTY OF STUDIO J SOLUTION PTE.LTD AND SHALL BE RETURNED ON COMPLETION OF WORKS. ALL MEASUREMENTS MUST BE CHECKED AT SITE BY THE CONTRACTOR AND NOTIFICATION TO BE MADE TO THE DESIGNER BEFORE COMMENCEMENT OF WORK. IN THE EVENT OF ANY DISCREPANCIES ARISING FROM THE DRAWINGS, ALL DRAWINGS MUST BE READ IN CONJUNCTION WITH OTHER CONSULTANT DRAWINGS.		
Drawn :		
WILLIAM		
Checked:		
JF		
Approved:		
First submission date:		
Scale :		
A3 AS SHOWN		
Drawing Title:		
FITURE ELEVATIONS		
Drawing Number:		
ELE -1		
Project Number:		
FRAN_BUGIS+_270726		

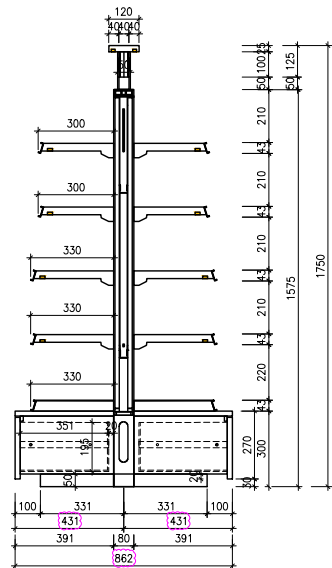


GONDOLA (MAKEUP)
(GD-M)

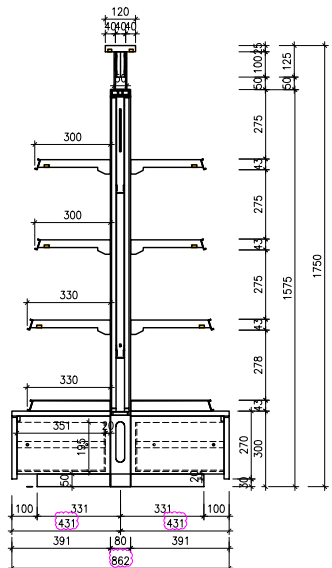


GONDOLA (STANDARD)
(GD-S4)

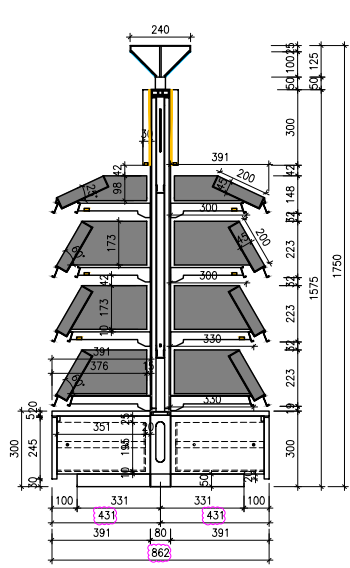


GONDOLA (STANDARD)
(GD-S5)

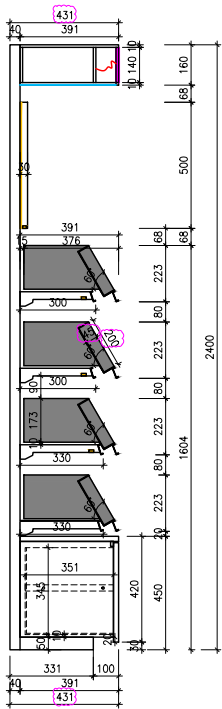


WALLBAY (MAKEUP)
(WB-M)

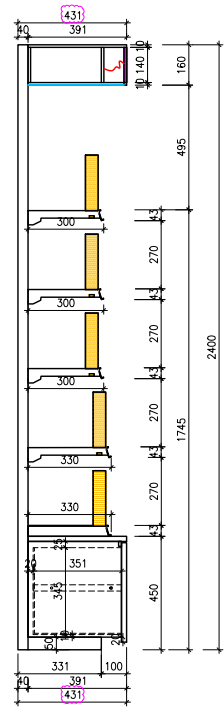


WALLBAY (STANDARD)
(WB-S4)

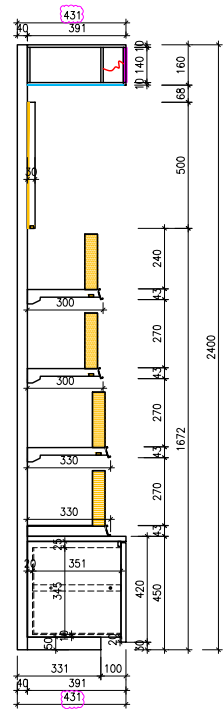



WALLBAY (STANDARD)
(WB-S5)

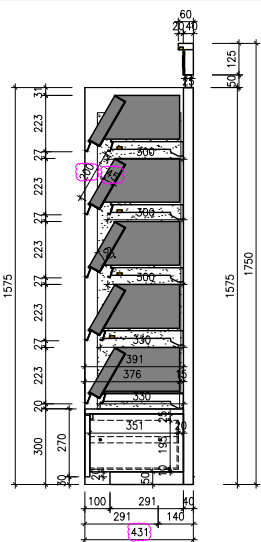

ENDCAP-BACK (MAKEUP)
(EC-M)

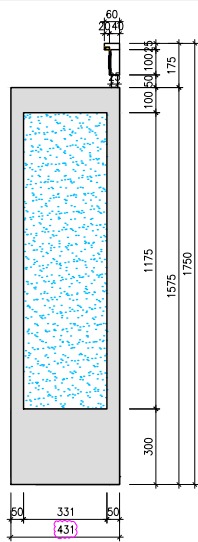


ENDCAP-FRONT (STANDARD)
(EC-S)

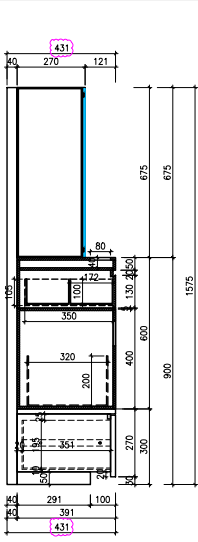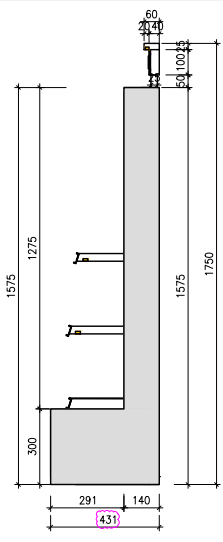


HYGIENE STATION
(HS-M)

Rev	Date	Description
Client:		
Project:		
FRAN @ BUGIS+ (#01-04)		
Project Management:		
 Studio J Solutions Pte. Ltd.		
email : enquiries@studioj.sg web : www.studioj.sg Add : 7 Mandal Link #03-20 Mandal Connection Singapore 728653		
Design Consultant:		
Main Contractor:		
 Studio J Solutions Pte. Ltd.		
email : enquiries@studioj.sg web : www.studioj.sg Add : 7 Mandal Link #03-20 Mandal Connection Singapore 728653		
Mechanical & Electrical Consultant:		
Structural Engineer:		
General Notes:		
COPYRIGHT OF ALL DESIGNS AND DATA SHOWN IN THIS DRAWING IS RETAINED BY STUDIO J SOLUTION PTE.LTD. WRITTEN PERMISSION IS REQUIRED FOR ANY USE AND/OR REPRODUCTION. ALL RIGHTS, SPECIFICATIONS AND COPYRIGHTS ARE THE PROPERTY OF STUDIO J SOLUTION PTE.LTD. AND SHALL BE RETURNED ON COMPLETION OF WORKS. ALL MEASUREMENTS MUST BE CHECKED AT SITE BY THE CONTRACTOR AND NOTIFICATION TO BE MADE TO THE DESIGNER BEFORE COMMENCEMENT OF WORK IN THE EVENT OF ANY DISCREPANCIES ARISING FROM THE DRAWINGS. ALL DRAWINGS MUST BE READ IN CONJUNCTION WITH OTHER CONSULTANT DRAWINGS.		
Drawn :		
WILLIAM		
Checked:		
JF		
Approved:		
First submission date:		
Scale :		
A3 AS SHOWN		
Drawing Title:		
FIXTURE SECTIONS		
Drawing Number:		
ELE-2		
Project Number:		
FRAN_BUGIS+_270726		

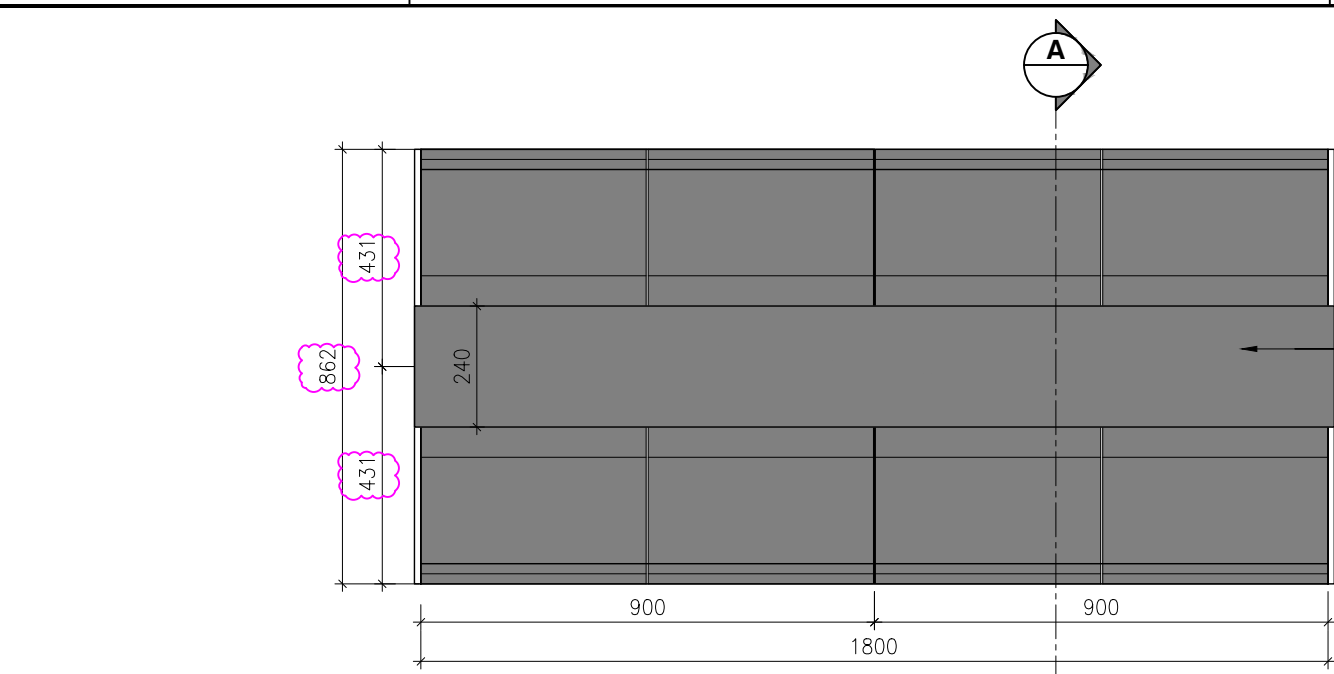


1 PLAN
SCALE 1:15

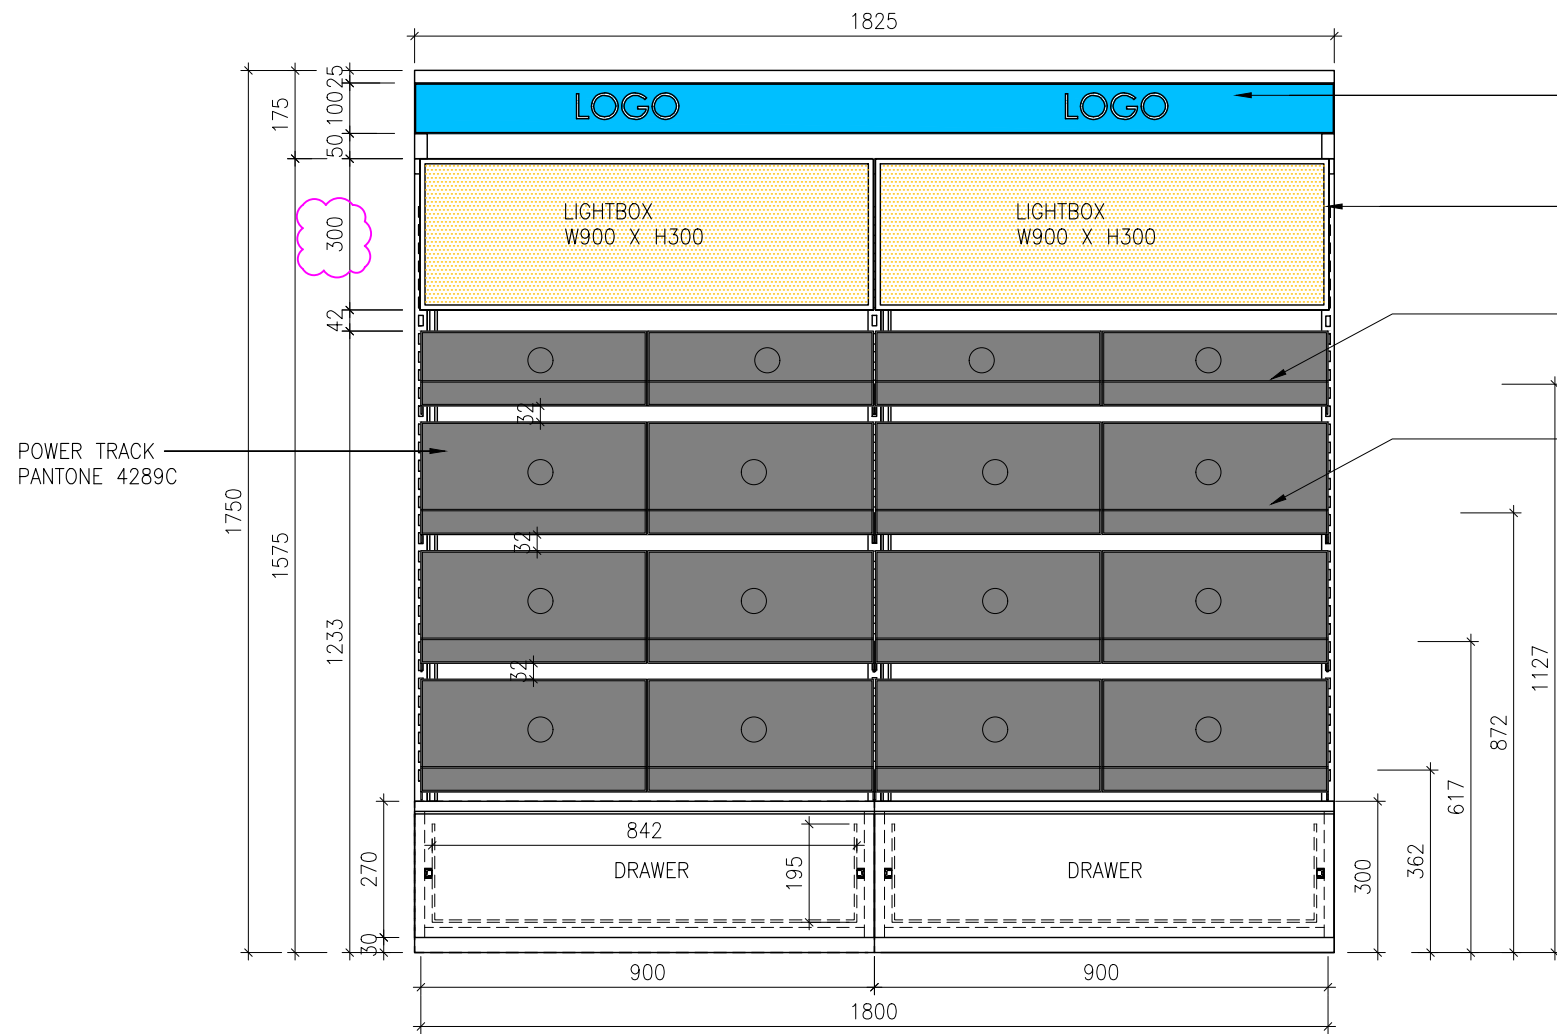

2 ELEVATION 1
SCALE 1:15

GONDOLA IN POWDER COATED FIN; PANTONE 4289C

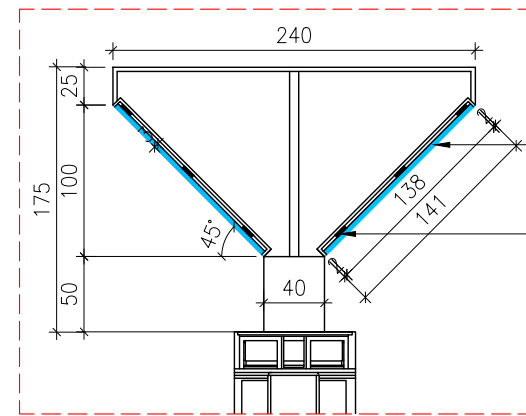

DETAIL A

REMOVABLE MIRROR WITH WHITE LOGO STICKER

MAGNETS


REMOVABLE MIRROR WITH WHITE LOGO STICKER

GONDOLA IN POWDER COATED FIN; PANTONE 4289C

MAKEUP DRAWER W450XD376XH148

MAKEUP DRAWER W450XD376XH223


SHELF IN PANTONE 4289C LED STRIP LIGHT 6000K

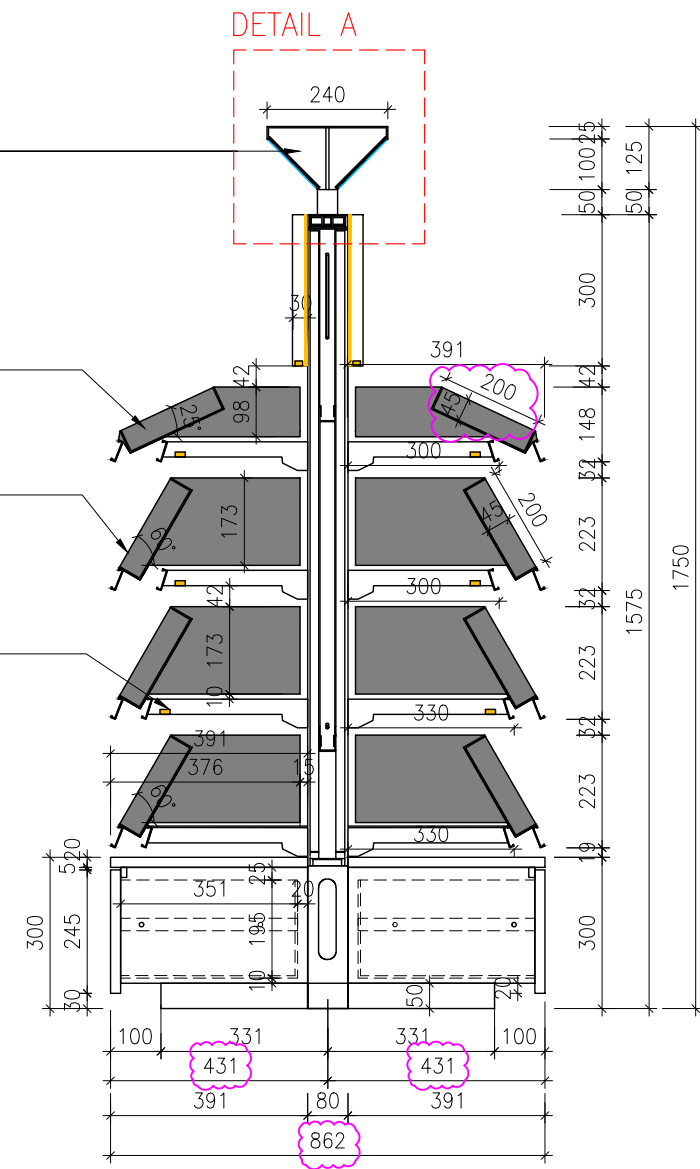


3 SECTION A
SCALE 1:15


GONDOLA	
MAKEUP	MAKEUP DRAWER + LIGHTBOX

Rev	Date	Description
Client:		
Project:		
FRAN @ BUGIS+ (#01-04)		
Project Management:		
Studio J Solutions Pte. Ltd		
email : enquiries@studioj.sg web : www.studioj.sg Add : 7 Mandal Link #03-20 Mandal Connection Singapore 728653		
Design Consultant:		
Main Contractor:		
Studio J Solutions Pte. Ltd		
email : enquiries@studioj.sg web : www.studioj.sg Add : 7 Mandal Link #03-20 Mandal Connection Singapore 728653		
Mechanical & Electrical Consultant:		
Structural Engineer:		
General Notes:		
COPYRIGHT OF ALL DESIGNS AND DATA SHOWN IN THIS DRAWING IS RETAINED BY STUDIO J SOLUTION PTE.LTD. WRITTEN PERMISSION IS REQUIRED FOR ANY USE AND/OR REPRODUCTION. ALL PRINTS, SPECIFICATIONS AND COPYRIGHTS ARE THE PROPERTY OF STUDIO J SOLUTION PTE.LTD. AND SHALL BE RETURNED ON COMPLETION OF WORKS. ALL MEASUREMENTS MUST BE CHECKED AT SITE BY THE CONTRACTOR AND NOTIFICATION TO BE MADE TO THE DESIGNER BEFORE COMMENCEMENT OF WORK IN THE EVENT OF ANY DISCREPANCIES ARISING FROM THE DRAWINGS. ALL DRAWINGS MUST BE READ IN CONJUNCTION WITH OTHER CONSULTANT DRAWINGS.		
Drawn :		
WILLIAM		
Checked:		
JF		
Approved:		
First submission date:		
Scale :		
A3 AS SHOWN		
Drawing Title:		
GONDOLA (MAKE UP)		
Drawing Number:		
GD-M		
Project Number:		
FRAN_BUGIS+_270726		

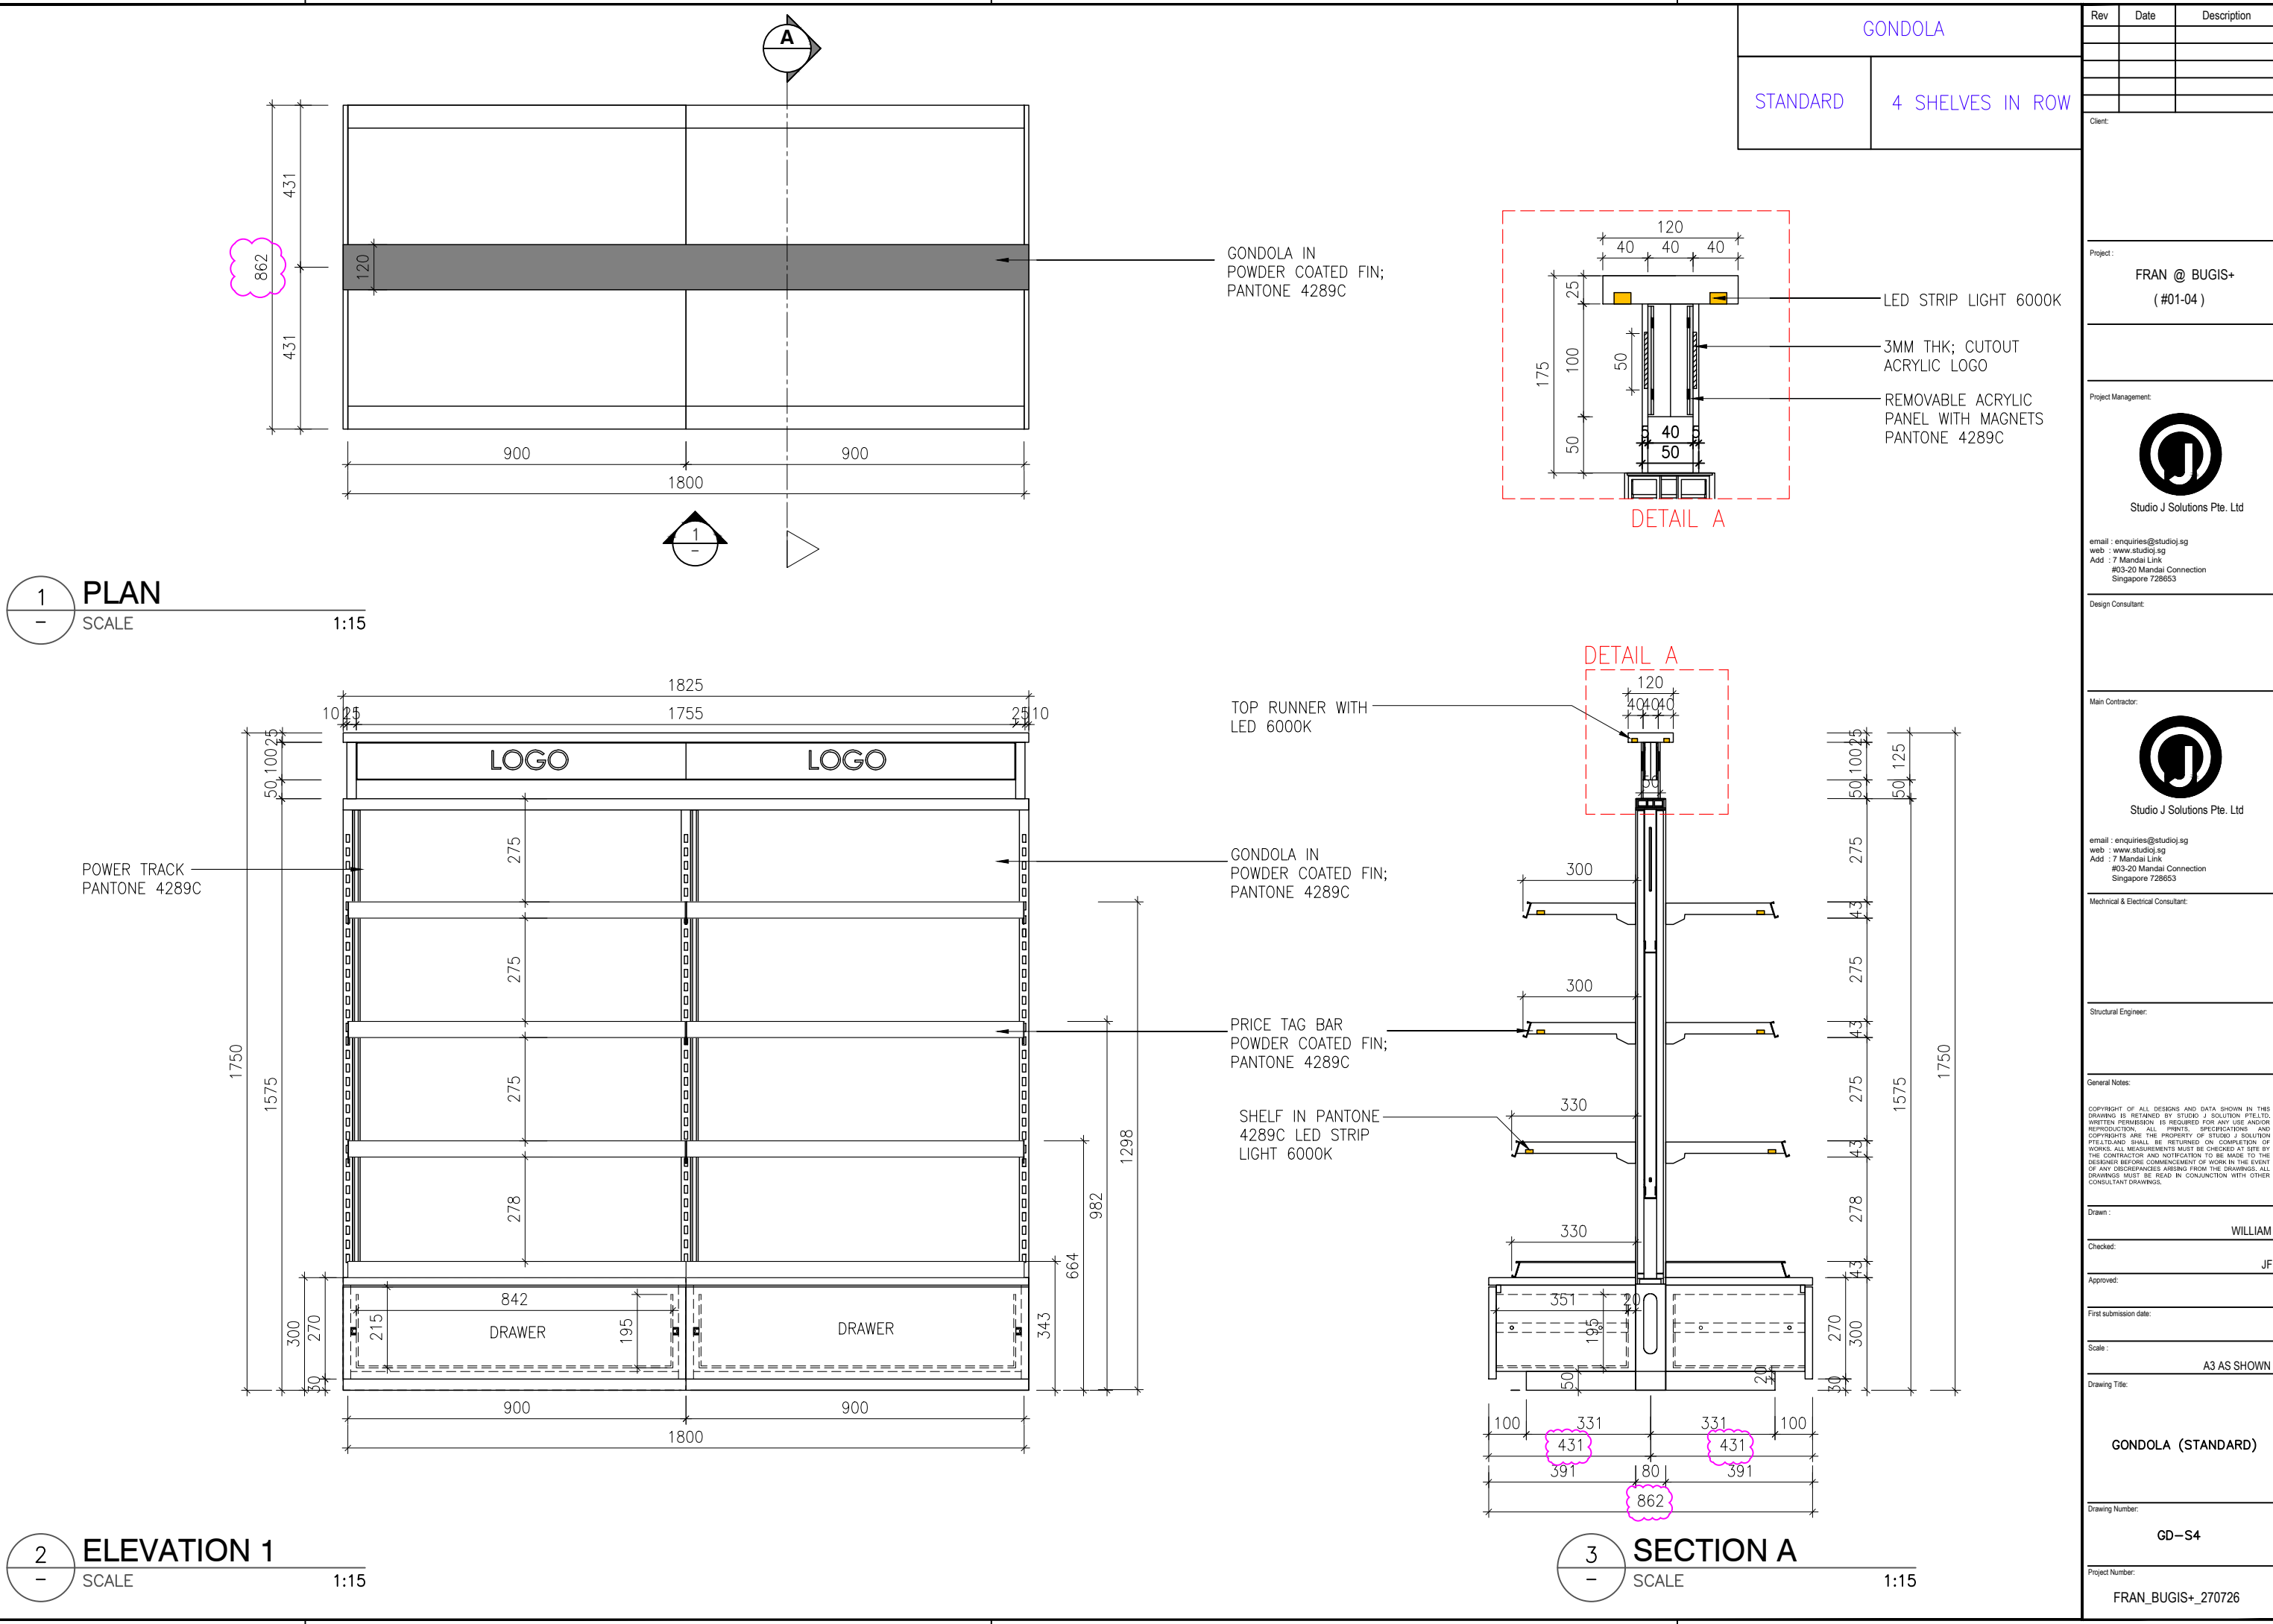

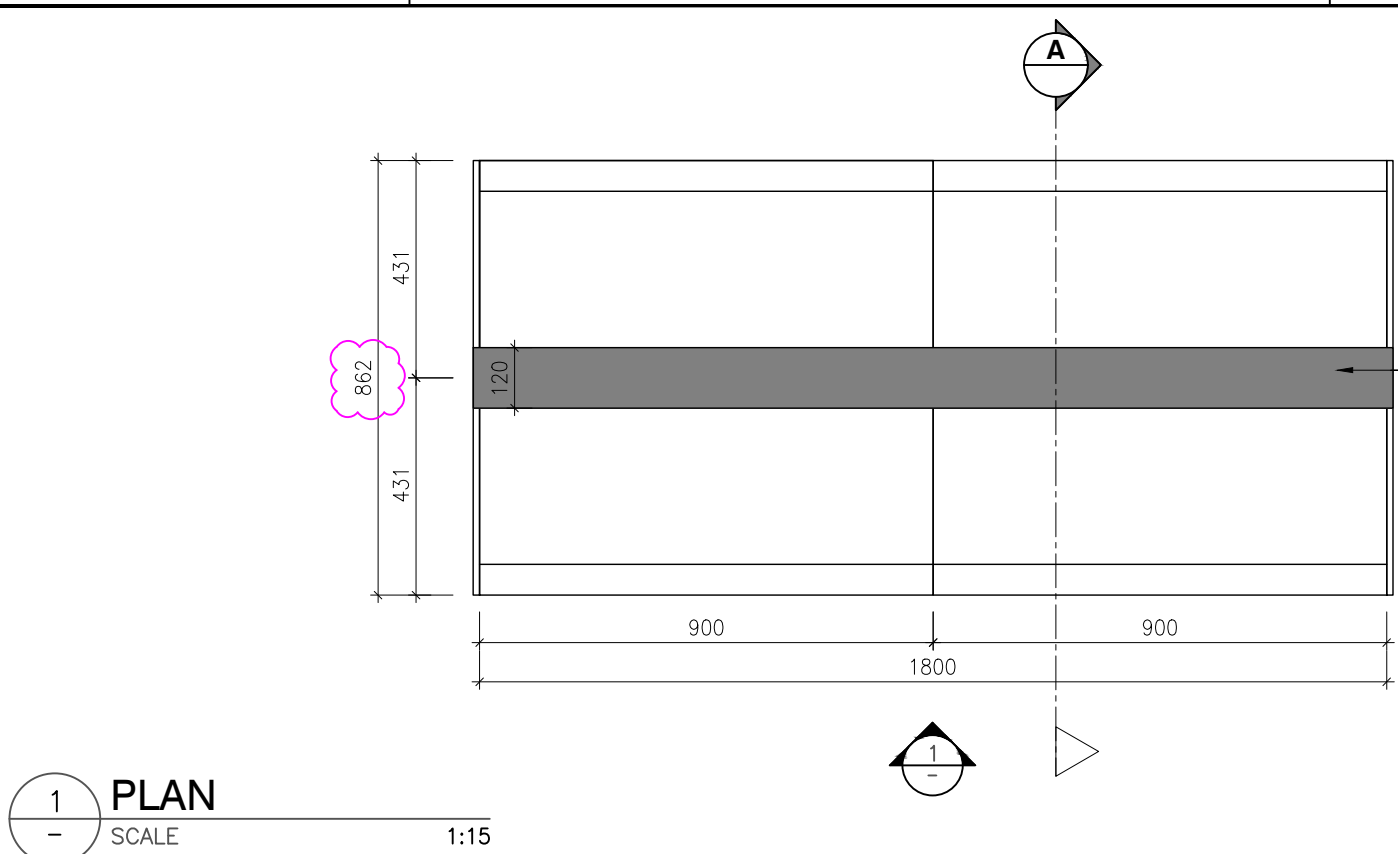

1 PLAN
SCALE 1:15

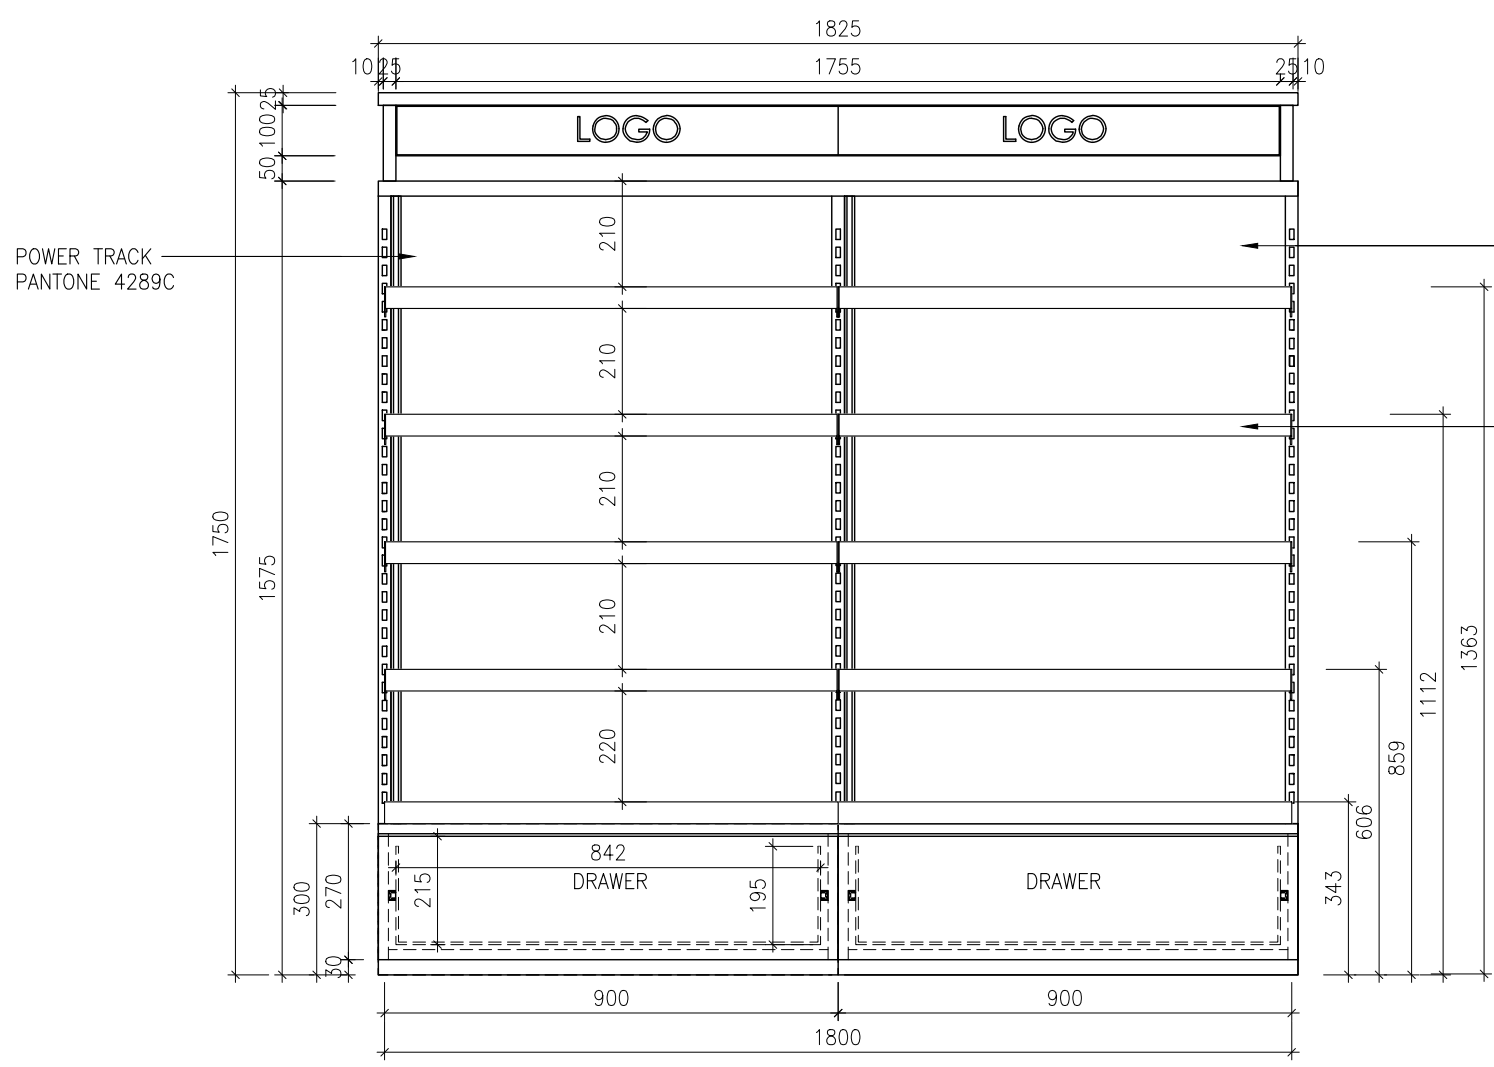

2 ELEVATION 1
SCALE 1:15


GONDOLA IN
POWDER COATED FIN;
PANTONE 4289C

TOP RUNNER WITH
LED 6000K

GONDOLA IN
POWDER COATED FIN;
PANTONE 4289C

PRICE TAG BAR
POWDER COATED FIN;
PANTONE 4289C


SHELF IN PANTONE
4289C LED STRIP
LIGHT 6000K

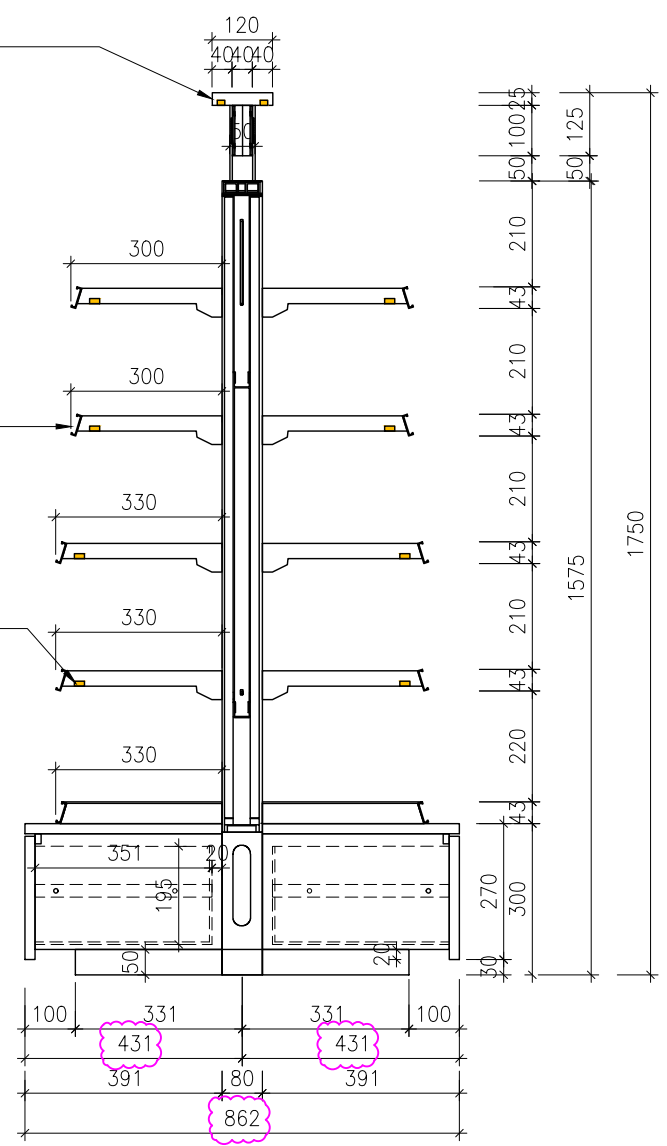


3 SECTION A
SCALE 1:15

GONDOLA	
STANDARD	5 SHELVES IN ROW

Rev	Date	Description
Client:		
Project:		
FRAN @ BUGIS+ (#01-04)		
Project Management:		
Studio J Solutions Pte. Ltd		
email : enquiries@studioj.sg web : www.studioj.sg Add : 7 Mandal Link #03-20 Mandal Connection Singapore 728653		
Design Consultant:		
Main Contractor:		
Studio J Solutions Pte. Ltd		
email : enquiries@studioj.sg web : www.studioj.sg Add : 7 Mandal Link #03-20 Mandal Connection Singapore 728653		
Mechanical & Electrical Consultant:		
Structural Engineer:		
General Notes:		
COPYRIGHT OF ALL DESIGNS AND DATA SHOWN IN THIS DRAWING IS RETAINED BY STUDIO J SOLUTION PTE.LTD. WRITTEN PERMISSION IS REQUIRED FOR ANY USE AND/OR REPRODUCTION. ALL PRINTS, SPECIFICATIONS AND COPYRIGHTS ARE THE PROPERTY OF STUDIO J SOLUTION PTE.LTD. AND SHALL BE RETURNED ON COMPLETION OF WORKS. ALL MEASUREMENTS MUST BE CHECKED AT SITE BY THE CONTRACTOR AND NOTIFICATION TO BE MADE TO THE DESIGNER BEFORE COMMENCEMENT OF WORK IN THE EVENT OF ANY DISCREPANCIES ARISING FROM THE DRAWINGS. ALL DRAWINGS MUST BE READ IN CONJUNCTION WITH OTHER CONSULTANT DRAWINGS.		
Drawn :		
WILLIAM		
Checked:		
JF		
Approved:		
First submission date:		
Scale :		
A3 AS SHOWN		
Drawing Title:		
GONDOLA (STANDARD)		
Drawing Number:		
GD-S5		
Project Number:		
FRAN_BUGIS+_270726		

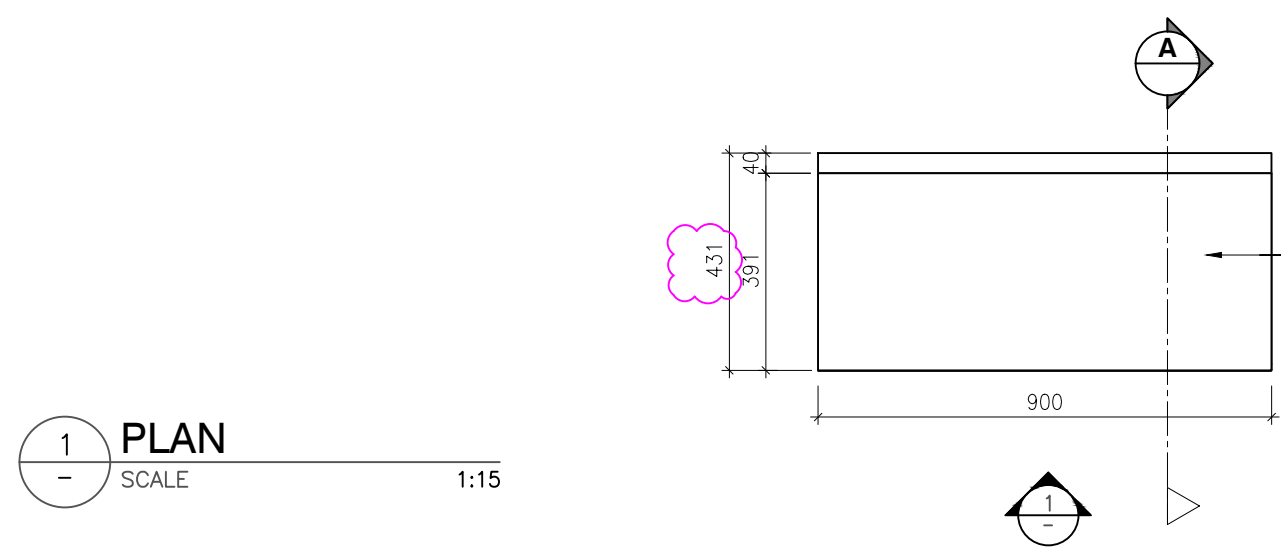

1 PLAN
SCALE 1:15

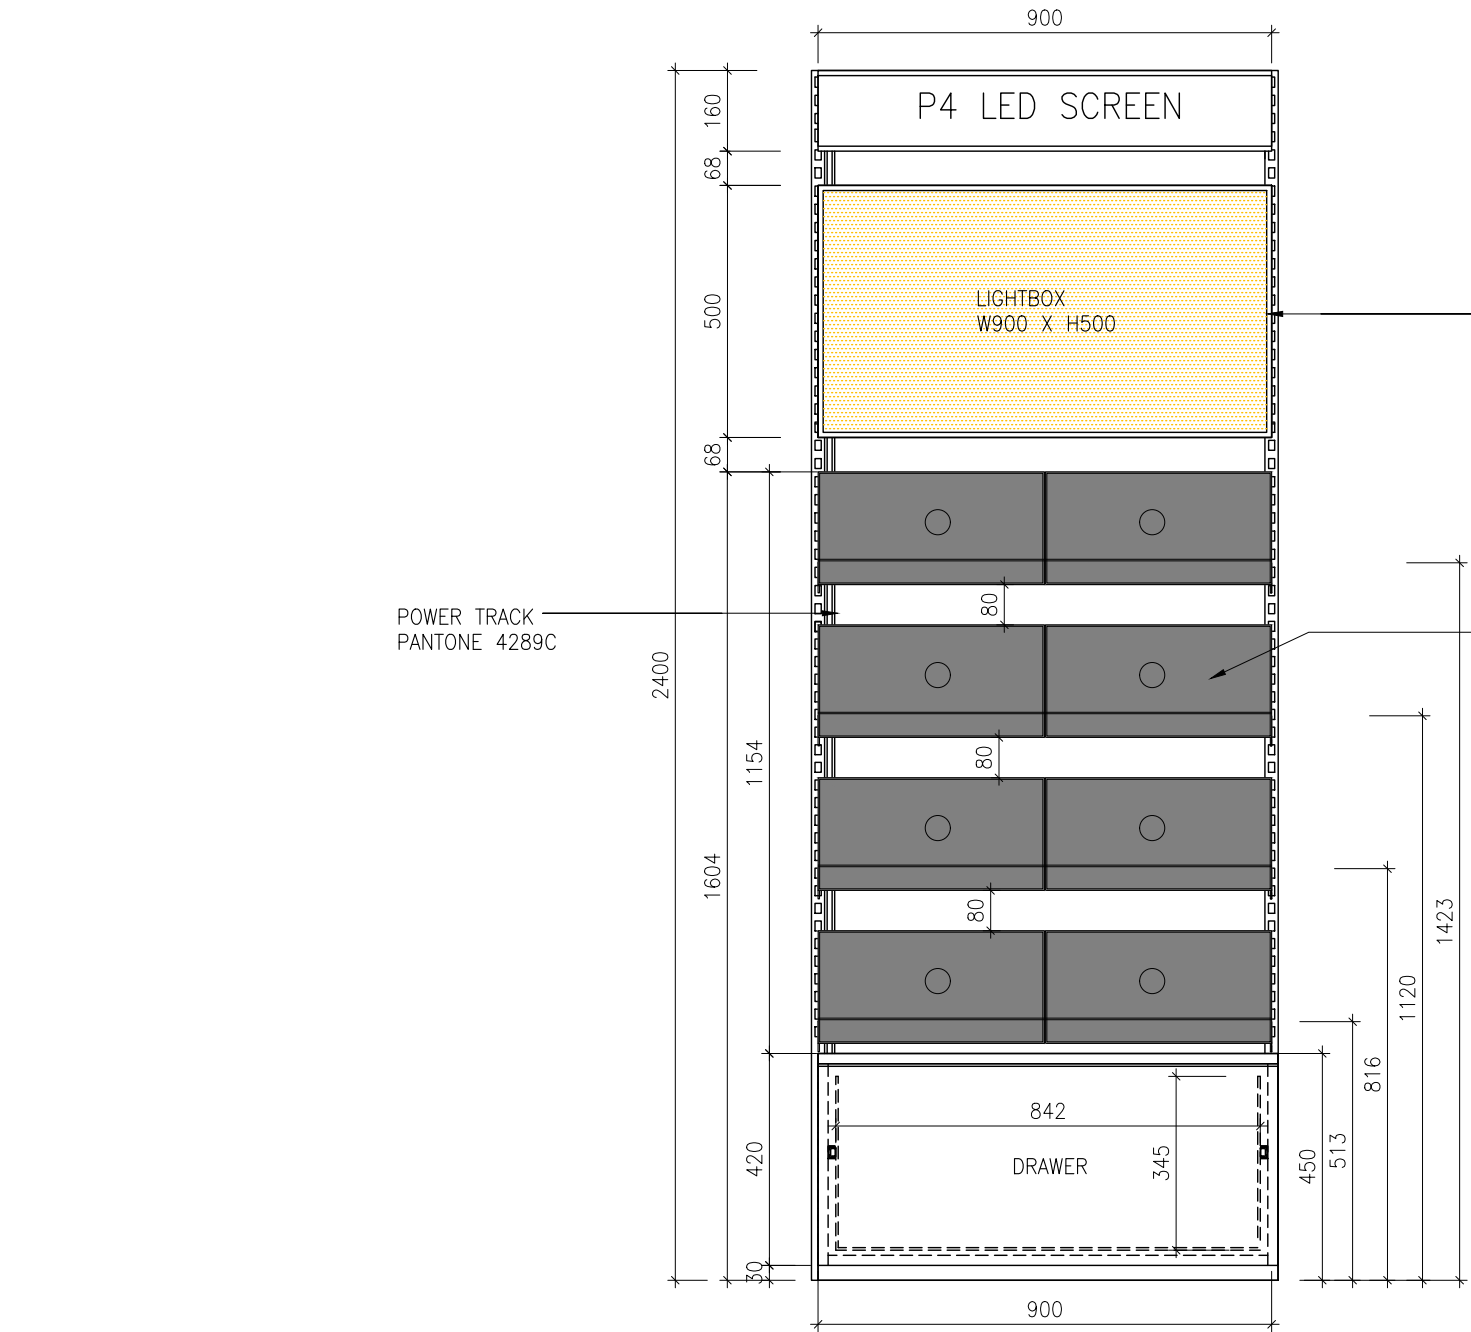


2 ELEVATION 1
SCALE 1:15

LED SCREEN
BOTTOM PANEL
WITH MIRROR FIN;

WALLBAY IN
POWDER COATED FIN;
PANTONE 4289C


MAKEUP DRAWER
W450XD376XH223

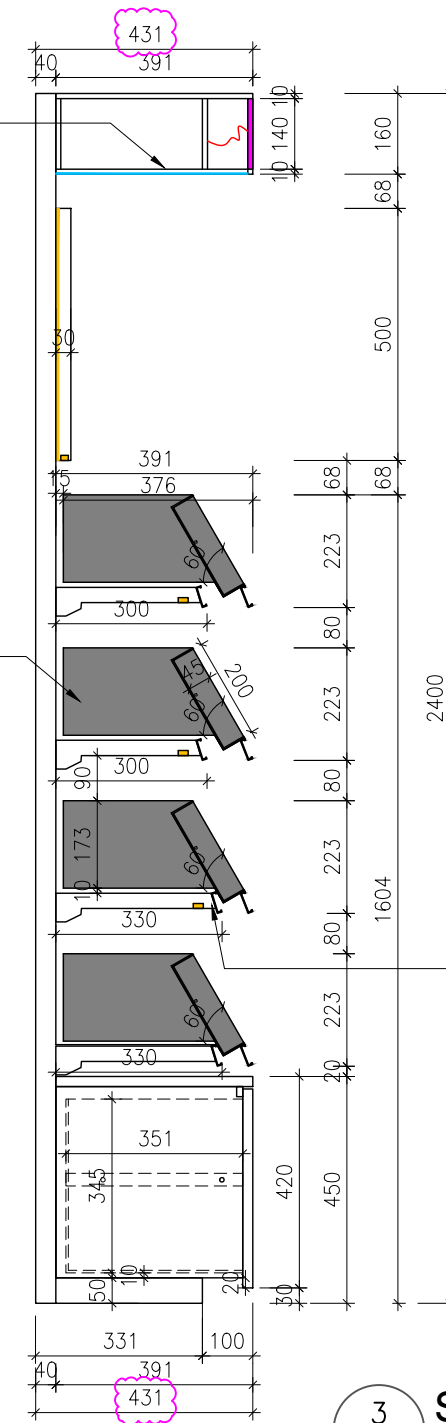


3 SECTION A
SCALE 1:15

WALLBAY		Rev	Date	Description	
MAKEUP	MAKEUP DRAWER + LIGHTBOX				
Client:					
Project :		FRAN @ BUGIS+ (#01-04)			
Project Management:		 Studio J Solutions Pte. Ltd email : enquiries@studioj.sg web : www.studioj.sg Add : 7 Mandai Link #03-20 Mandal Connection Singapore 728653			
Design Consultant:					
Main Contractor:		 Studio J Solutions Pte. Ltd email : enquiries@studioj.sg web : www.studioj.sg Add : 7 Mandai Link #03-20 Mandal Connection Singapore 728653			
Mechanical & Electrical Consultant:					
Structural Engineer:					
General Notes:		COPYRIGHT OF ALL DESIGNS AND DATA SHOWN IN THIS DRAWING IS RETAINED BY STUDIO J SOLUTION PTE.LTD. WRITTEN PERMISSION IS REQUIRED FOR ANY USE AND/OR REPRODUCTION. ALL PRINTS, SPECIFICATIONS AND COPYRIGHTS ARE THE PROPERTY OF STUDIO J SOLUTION PTE.LTD. SHALL BE RETURNED ON COMPLETION OF WORKS. ALL MEASUREMENTS MUST BE CHECKED AT SITE BY THE CONTRACTOR AND NOTIFICATION TO BE MADE TO THE DESIGNER BEFORE COMMENCEMENT OF WORK IN THE EVENT OF ANY DISCREPANCIES ARISING FROM THE DRAWINGS. ALL DRAWINGS MUST BE READ IN CONJUNCTION WITH OTHER CONSULTANT DRAWINGS.			
Drawn :		WILLIAM			
Checked:		JF			
Approved:					
First submission date:					
Scale :		A3 AS SHOWN			
Drawing Title:		WALLBAY (MAKEUP)			
Drawing Number:		WB-M			
Project Number:		FRAN_BUGIS+_270726			

</

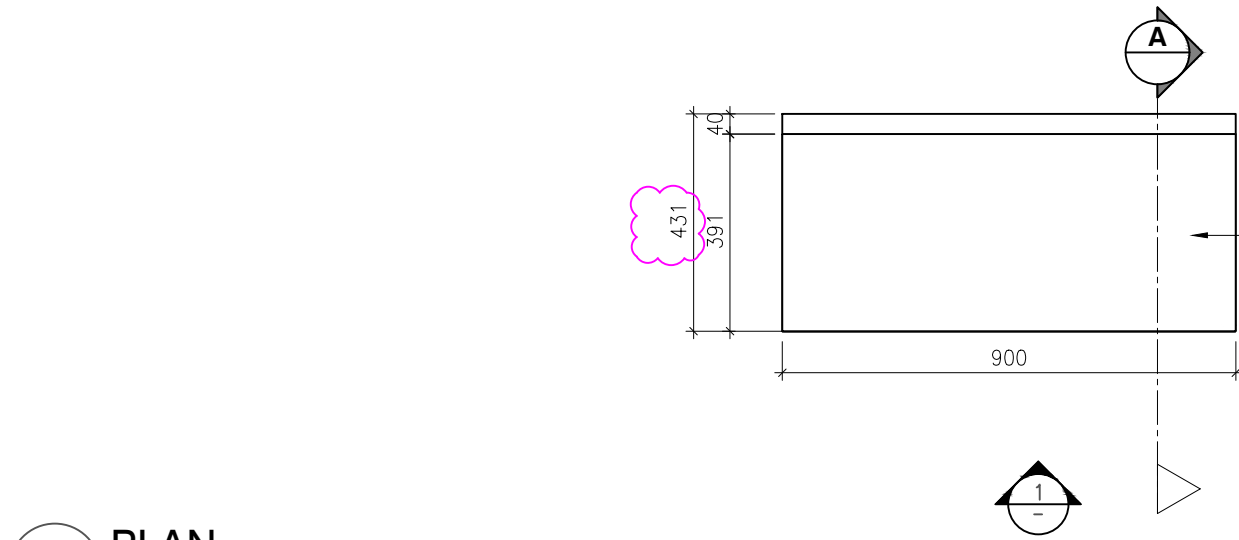

1 PLAN
SCALE 1:15

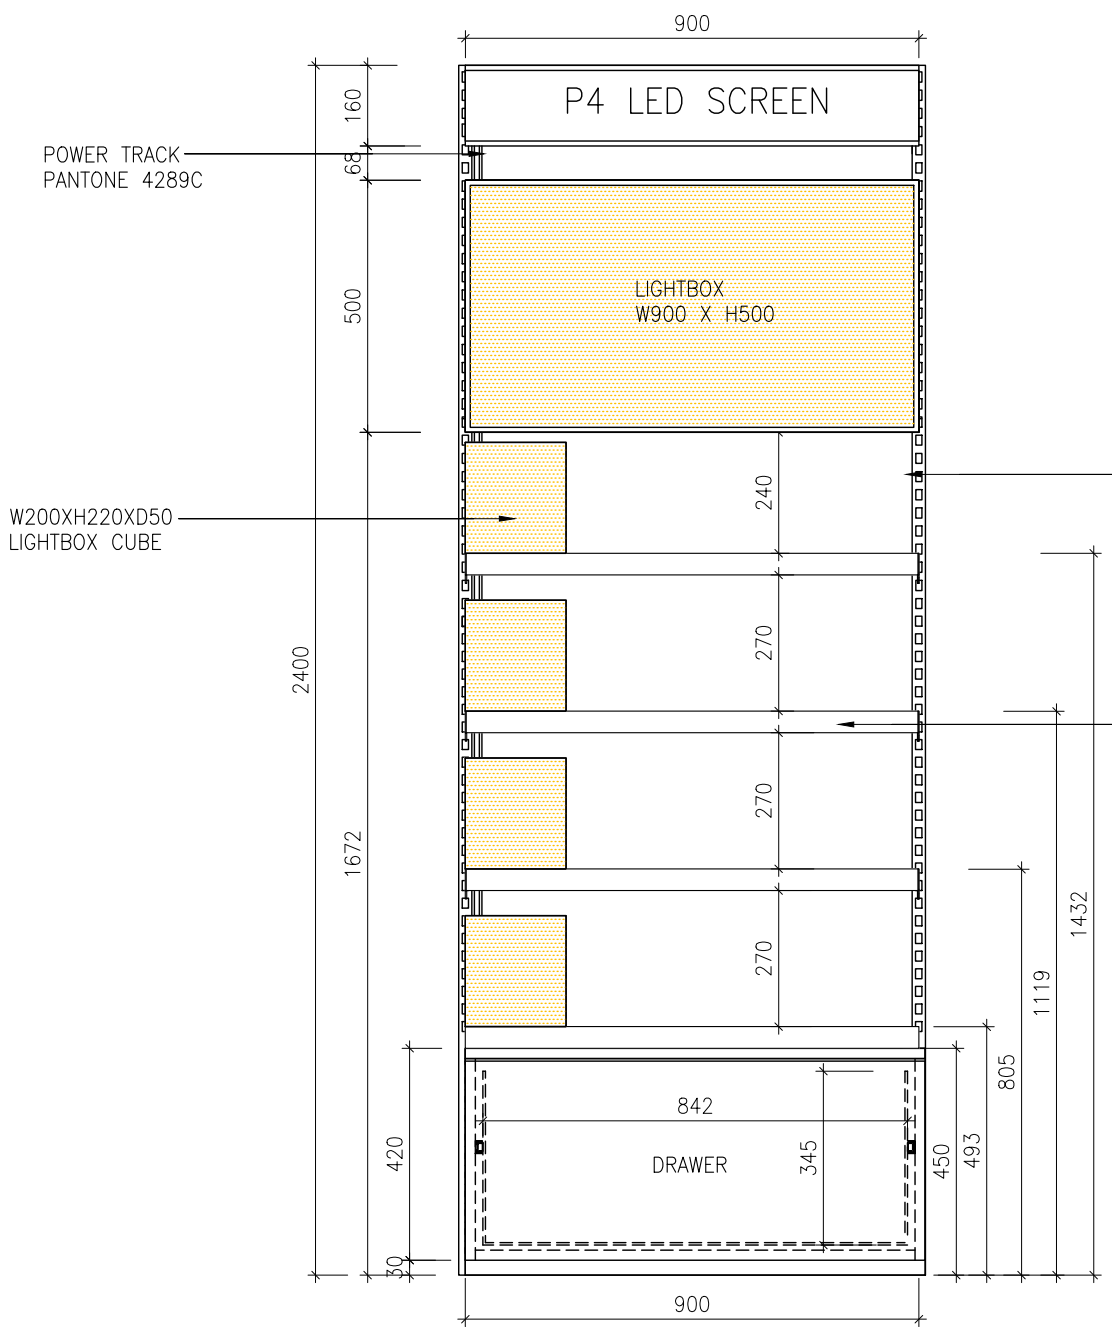


2 ELEVATION 1
SCALE 1:15

WALLBAY IN
POWDER COATED FIN;
PANTONE 4289C

LED SCREEN
BOTTOM PANEL
WITH MIRROR FIN;

WALLBAY IN
POWDER COATED FIN;
PANTONE 4289C


PRICE TAG BAR
POWDER COATED FIN;
PANTONE 4289C

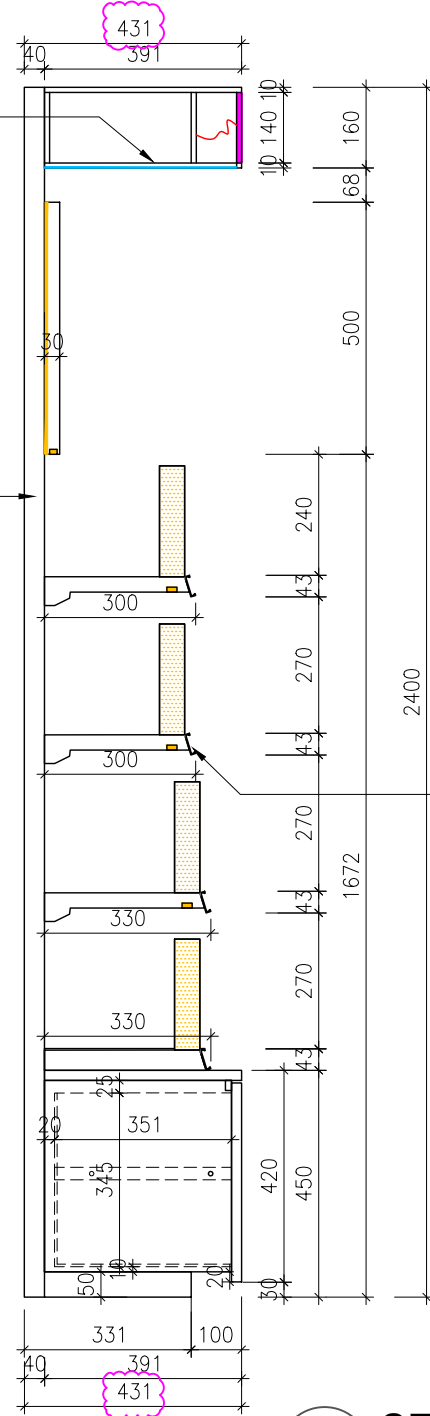


3 SECTION A
SCALE 1:15


WALLBAY	
STANDARD	4 SHELVES+LIGHTBOX +SMALL LIGHTBOX

Rev	Date	Description
Client:		
Project:		
FRAN @ BUGIS+ (#01-04)		
Project Management:		
 Studio J Solutions Pte. Ltd.		
email : enquiries@studioj.sg web : www.studioj.sg Add : 7 Mandal Link #03-20 Mandal Connection Singapore 728653		
Design Consultant:		
Main Contractor:		
 Studio J Solutions Pte. Ltd.		
email : enquiries@studioj.sg web : www.studioj.sg Add : 7 Mandal Link #03-20 Mandal Connection Singapore 728653		
Mechanical & Electrical Consultant:		
Structural Engineer:		
General Notes:		
COPYRIGHT OF ALL DESIGNS AND DATA SHOWN IN THIS DRAWING IS RETAINED BY STUDIO J SOLUTION PTE.LTD. WRITTEN PERMISSION IS REQUIRED FOR ANY USE AND/OR REPRODUCTION. ALL PRINTS, SPECIFICATIONS AND COPYRIGHTS ARE THE PROPERTY OF STUDIO J SOLUTION PTE.LTD. AND SHALL BE RETURNED ON COMPLETION OF WORKS. ALL MEASUREMENTS MUST BE CHECKED AT SITE BY THE CONTRACTOR AND NOTIFICATION TO BE MADE TO THE DESIGNER BEFORE COMMENCEMENT OF WORK IN THE EVENT OF ANY DISCREPANCIES ARISING FROM THE DRAWINGS. ALL DRAWINGS MUST BE READ IN CONJUNCTION WITH OTHER CONSULTANT DRAWINGS.		
Drawn :		
WILLIAM		
Checked:		
JF		
Approved:		
First submission date:		
Scale :		
A3 AS SHOWN		
Drawing Title:		
WALLBAY (STANDARD) WITH VISUAL		
Drawing Number:		
WB-S4		
Project Number:		
FRAN_BUGIS+_270726		

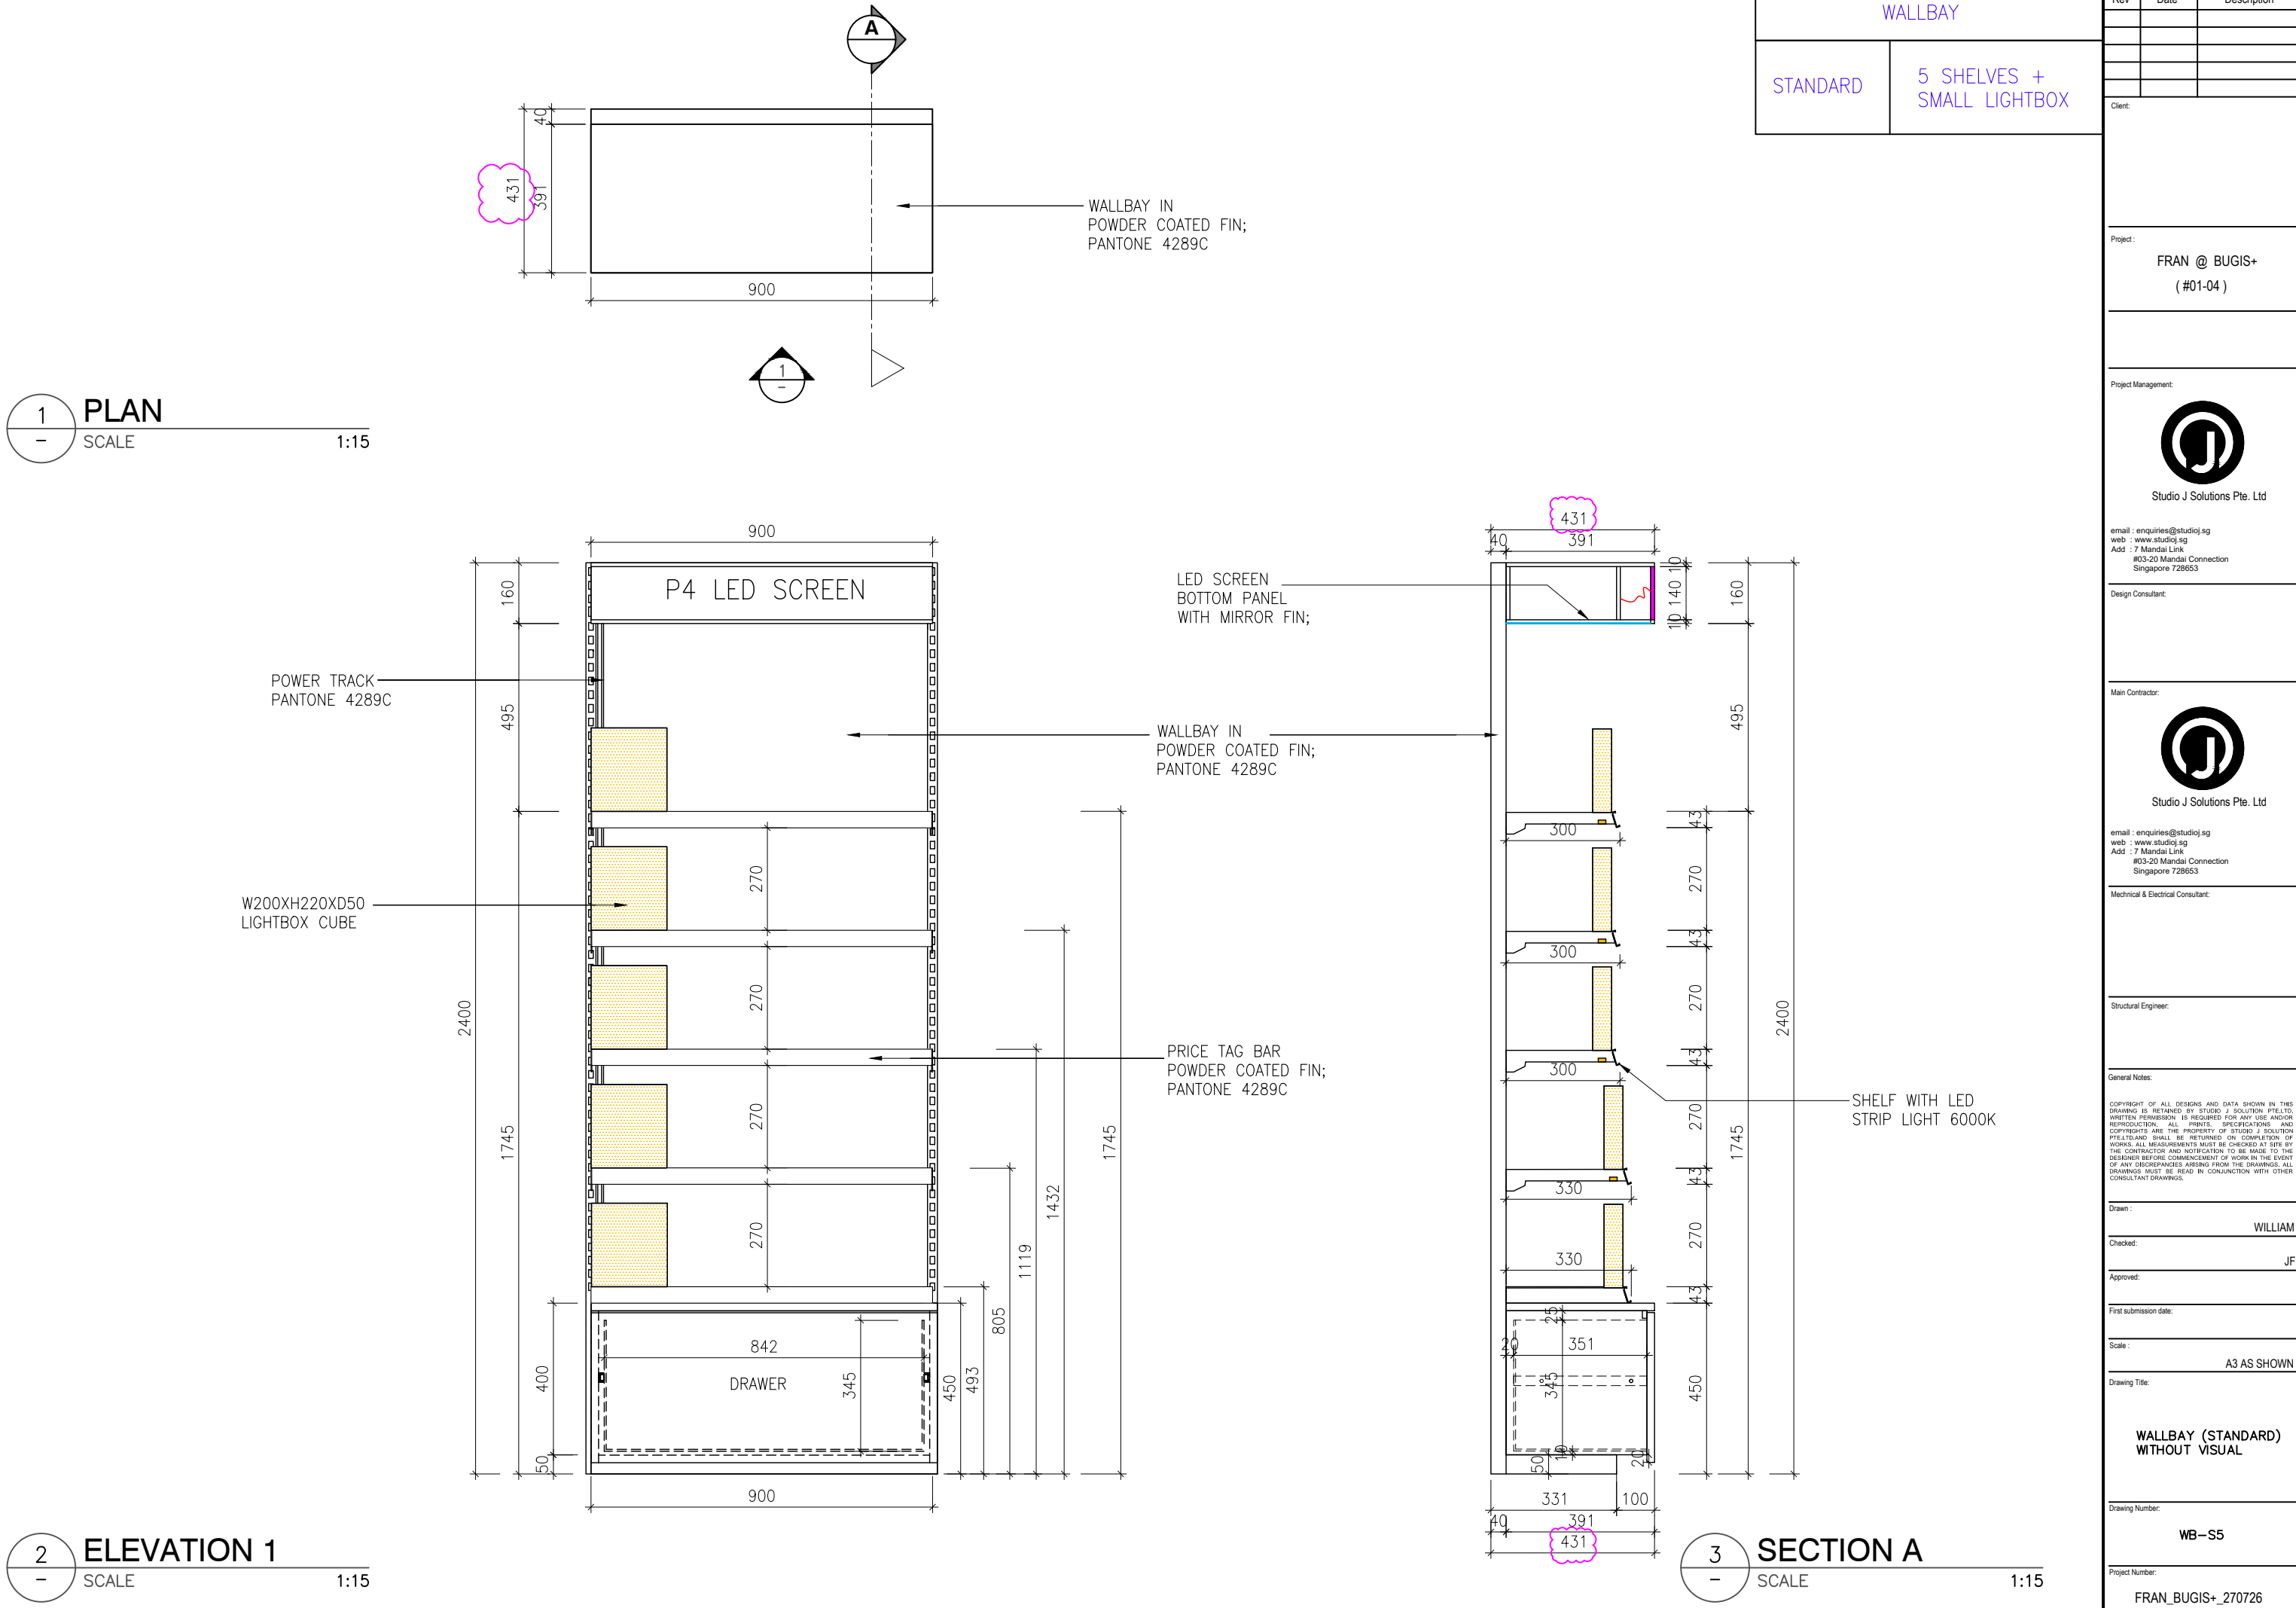

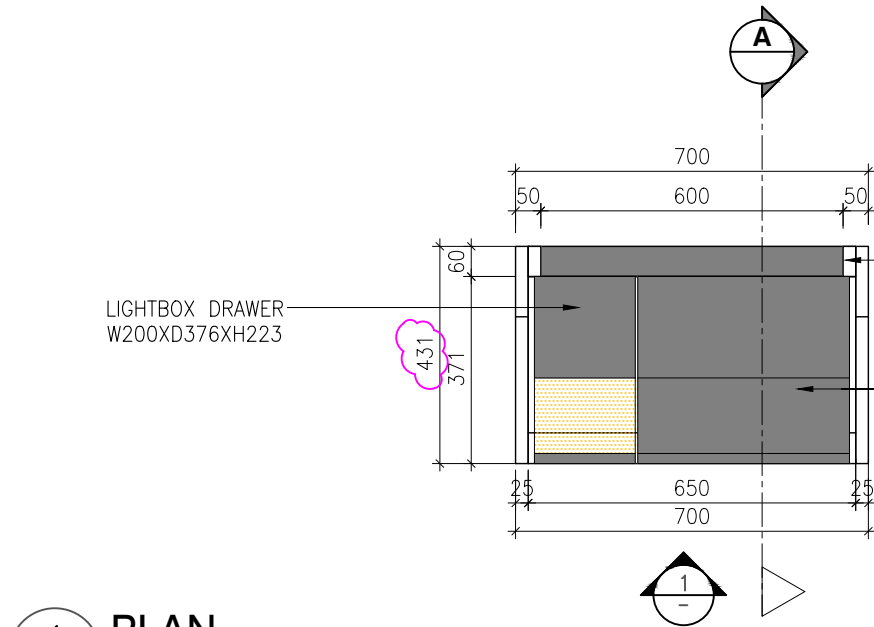


1 PLAN
SCALE 1:15

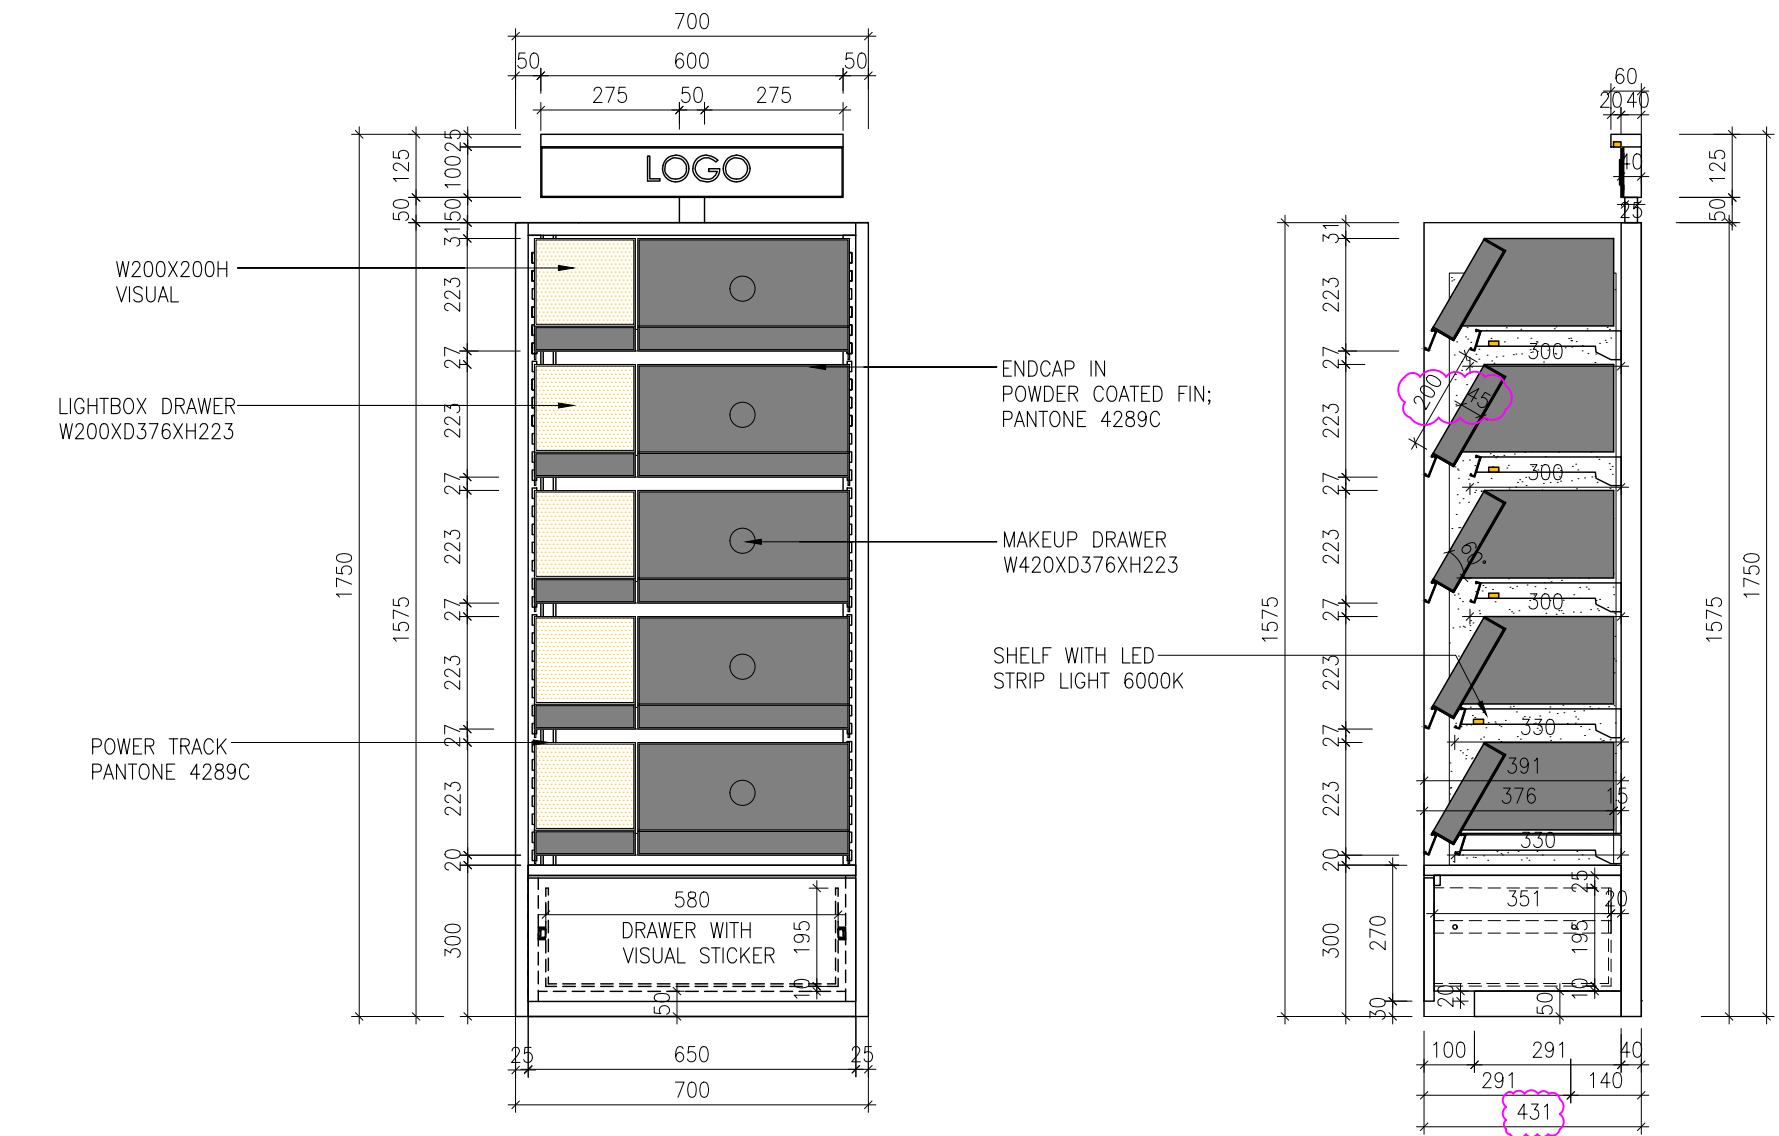


2 ELEVATION 1
SCALE 1:15

3 SECTION A
SCALE 1:15

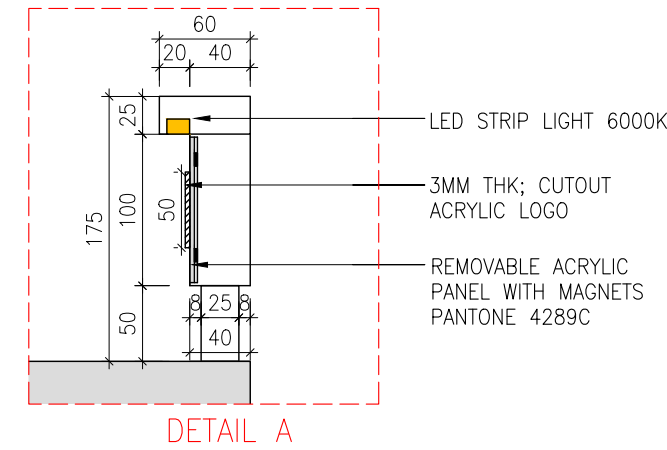

DETAIL A

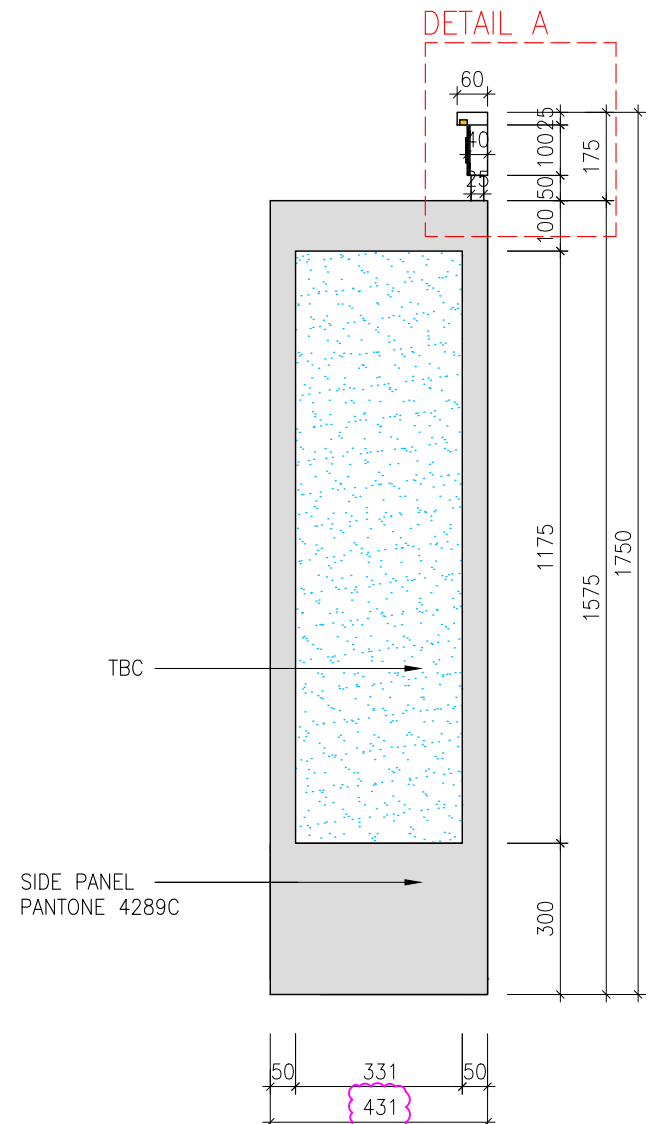

4 SIDE VIEW
SCALE 1:15

ENDCAP		Rev	Date	Description
MAKEUP	MAKEUP DRAWER + LIGHTBOX DRAWER			
		Client:		
		Project :		
		FRAN @ BUGIS+ (#01-04)		
		Project Management:		
		 Studio J Solutions Pte. Ltd		
		email : enquires@studioj.sg web : www.studioj.sg Add : 7 Mandal Link #03-20 Mandal Connection Singapore 728653		
		Design Consultant:		
		Main Contractor:		
		 Studio J Solutions Pte. Ltd		
		email : enquires@studioj.sg web : www.studioj.sg Add : 7 Mandal Link #03-20 Mandal Connection Singapore 728653		
		Mechanical & Electrical Consultant:		
		Structural Engineer:		
		General Notes:		
		COPYRIGHT OF ALL DESIGNS AND DATA SHOWN IN THIS DRAWING IS RETAINED BY STUDIO J SOLUTION PTE.LTD. WRITTEN PERMISSION IS REQUIRED FOR ANY USE AND/OR REPRODUCTION. ALL PRINTS, SPECIFICATIONS AND COPYRIGHTS ARE THE PROPERTY OF STUDIO J SOLUTION PTE.LTD AND SHALL BE RETURNED ON COMPLETION OF WORKS. ALL MEASUREMENTS MUST BE CHECKED AT SITE BY THE CONTRACTOR AND NOTIFICATION TO BE MADE TO THE DESIGNER BEFORE COMMENCEMENT OF WORK. IN THE EVENT OF ANY DISCREPANCIES ARISING FROM THE DRAWINGS, ALL DRAWINGS MUST BE READ IN CONJUNCTION WITH OTHER CONSULTANT DRAWINGS.		
		Drawn :		
		WILLIAM		
		Checked:		
		JF		
		Approved:		
		First submission date:		
		Scale :		
		A3 AS SHOWN		
		Drawing Title:		
		ENDCAP BACK (MAKEUP)		
		Drawing Number:		
		EC—M		
		Project Number:		
		FRAN_BUGIS+_270726		

LED STRIP LIGHT 6000K

3MM THK; CUTOUT
ACRYLIC LOGO

REMOVABLE ACRYLIC
PANEL WITH MAGNETS
PANTONE 4289C

DETAIL A

60

100

50

100

175

1175

1575

1750

300

50

100

50

100

175

1175

1575

1750

300

50

DE VIEW

1:15

FRAN @ BUGIS+
(#01-04)

Studio J Solutions Pte. Ltd

email : enquiries@studioj.sg
web : www.studioj.sg
Add : 7 Mandal Link
#03-20 Mandal Connection
Singapore 728653

Design Consultant:

Main Contractor:

Studio J Solutions Pte. Ltd

email : enquiries@studioj.sg
web : www.studioj.sg
Add : 7 Mandal Link
#03-20 Mandal Connection
Singapore 728653

Mechanical & Electrical Consultant:

Structural Engineer:

General Notes:

COPYRIGHT OF ALL DESIGNS AND DATA SHOWN IN THIS DRAWING IS RETAINED BY STUDIO J SOLUTION PTE.LTD. WRITTEN PERMISSION IS REQUIRED FOR ANY USE AND/OR REPRODUCTION. ALL RIGHTS, SPECIFICATIONS AND COPYRIGHTS ARE THE PROPERTY OF STUDIO J SOLUTION PTE.LTD. AND SHALL BE RETURNED ON COMPLETION OF WORKS. ALL MEASUREMENTS MUST BE CHECKED AT SITE BY THE CONTRACTOR AND NOTIFICATION TO BE MADE TO THE DESIGNER BEFORE COMMENCEMENT OF WORK IN THE EVENT OF ANY DISCREPANCIES ARISING FROM THE DRAWINGS. ALL DRAWINGS MUST BE READ IN CONJUNCTION WITH OTHER CONSULTANT DRAWINGS.

Drawn : WILLIAM

Checked : JF

Approved :

First submission date:


Scale : A3 AS SHOWN

Drawing Title: ENDCAP BACK (MAKEUP)

Drawing Number:


Project Number: EC-M

Project Number: FRAN_BUGIS+_270726

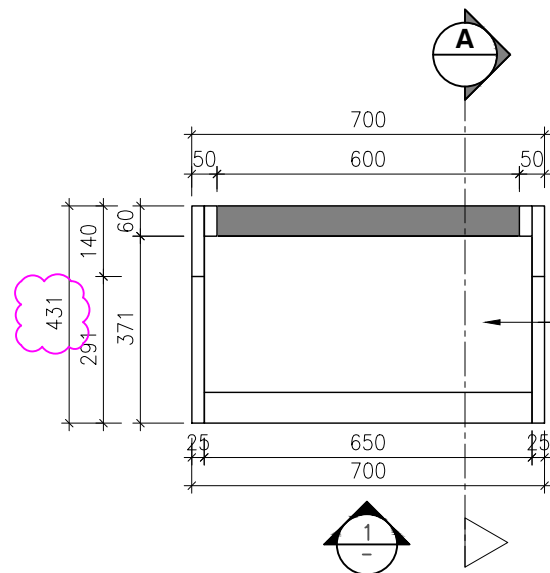

ENDCAP IN
POWDER COATED FIN;
PANTONE 4289C

1 PLAN
SCALE 1:15

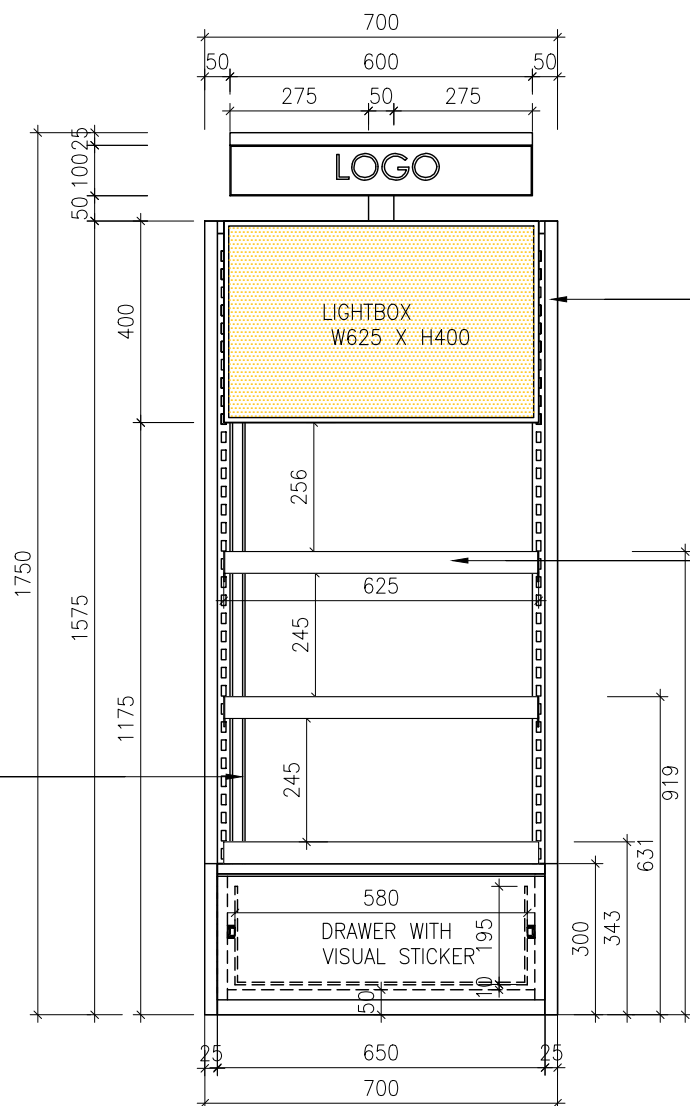


ENDCAP IN
POWDER COATED FIN;
PANTONE 4289C


PRICE TAG BAR
POWDER COATED FIN;
PANTONE 4289C

POWER TRACK
PANTONE 4289C

2 ELEVATION 1
SCALE 1:15

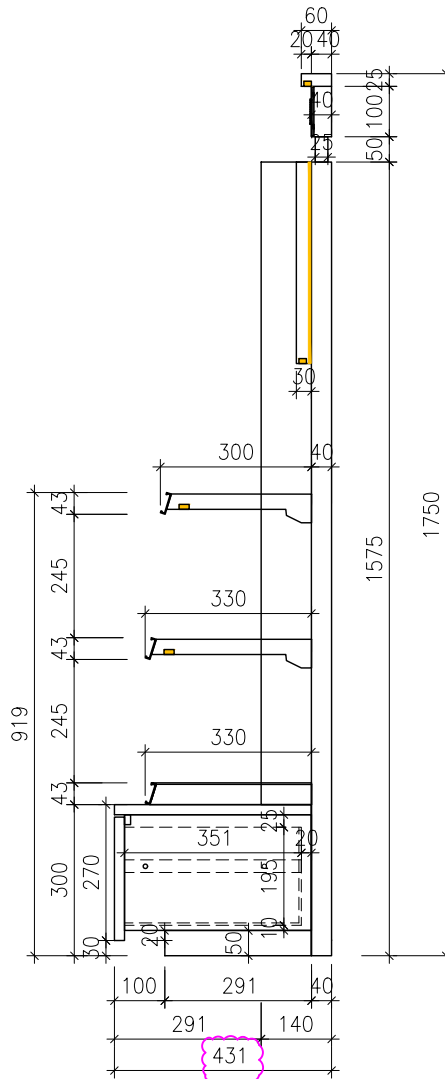

3 SECTION A
SCALE 1:15

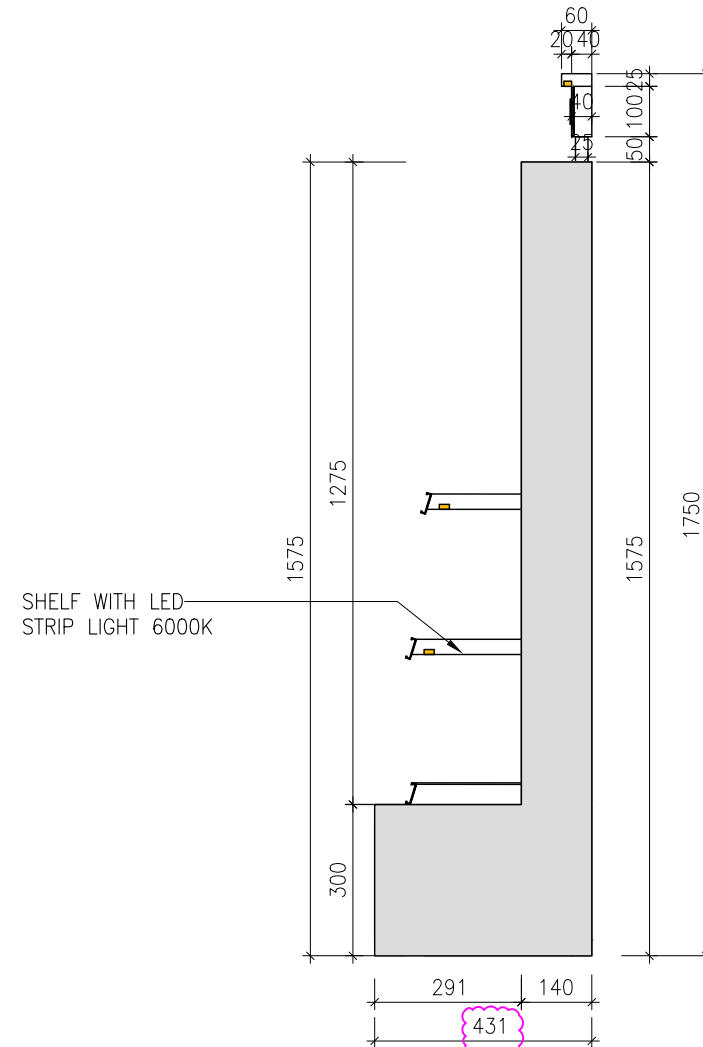


SHELF WITH LED
STRIP LIGHT 6000K

4 SIDE VIEW
SCALE 1:15

ENDCAP		Rev	Date	Description
STANDARD	3 SHELVES + LIGHTBOX			
Client:				
Project :				
FRAN @ BUGIS+ (#01-04)				
Project Management:				
 Studio J Solutions Pte. Ltd email : enquiries@studioj.sg web : www.studioj.sg Add : 7 Mandal Link #03-20 Mandal Connection Singapore 728653				
Design Consultant:				
Main Contractor:				
 Studio J Solutions Pte. Ltd email : enquiries@studioj.sg web : www.studioj.sg Add : 7 Mandal Link #03-20 Mandal Connection Singapore 728653				
Mechanical & Electrical Consultant:				
Structural Engineer:				
General Notes:				
COPYRIGHT OF ALL DESIGNS AND DATA SHOWN IN THIS DRAWING IS RETAINED BY STUDIO J SOLUTION PTE.LTD. WRITTEN PERMISSION IS REQUIRED FOR ANY USE AND/OR REPRODUCTION. ALL RIGHTS, SPECIFICATIONS AND COPYRIGHTS ARE THE PROPERTY OF STUDIO J SOLUTION PTE.LTD. AND SHALL BE RETURNED ON COMPLETION OF WORKS. ALL MEASUREMENTS MUST BE CHECKED AT SITE BY THE CONTRACTOR AND NOTIFICATION TO BE MADE TO THE DESIGNER BEFORE COMMENCEMENT OF WORK IN THE EVENT OF ANY DISCREPANCIES ARISING FROM THE DRAWINGS. ALL DRAWINGS MUST BE READ IN CONJUNCTION WITH OTHER CONSULTANT DRAWINGS.				
Drawn :				
WILLIAM				
Checked:				
JF				
Approved:				
First submission date:				
Scale :				
A3 AS SHOWN				
Drawing Title:				
ENDCAP FRONT (STANDARD)				
Drawing Number:				
EC-S				
Project Number:				
FRAN_BUGIS+_270726				


1 PLAN
SCALE 1:10

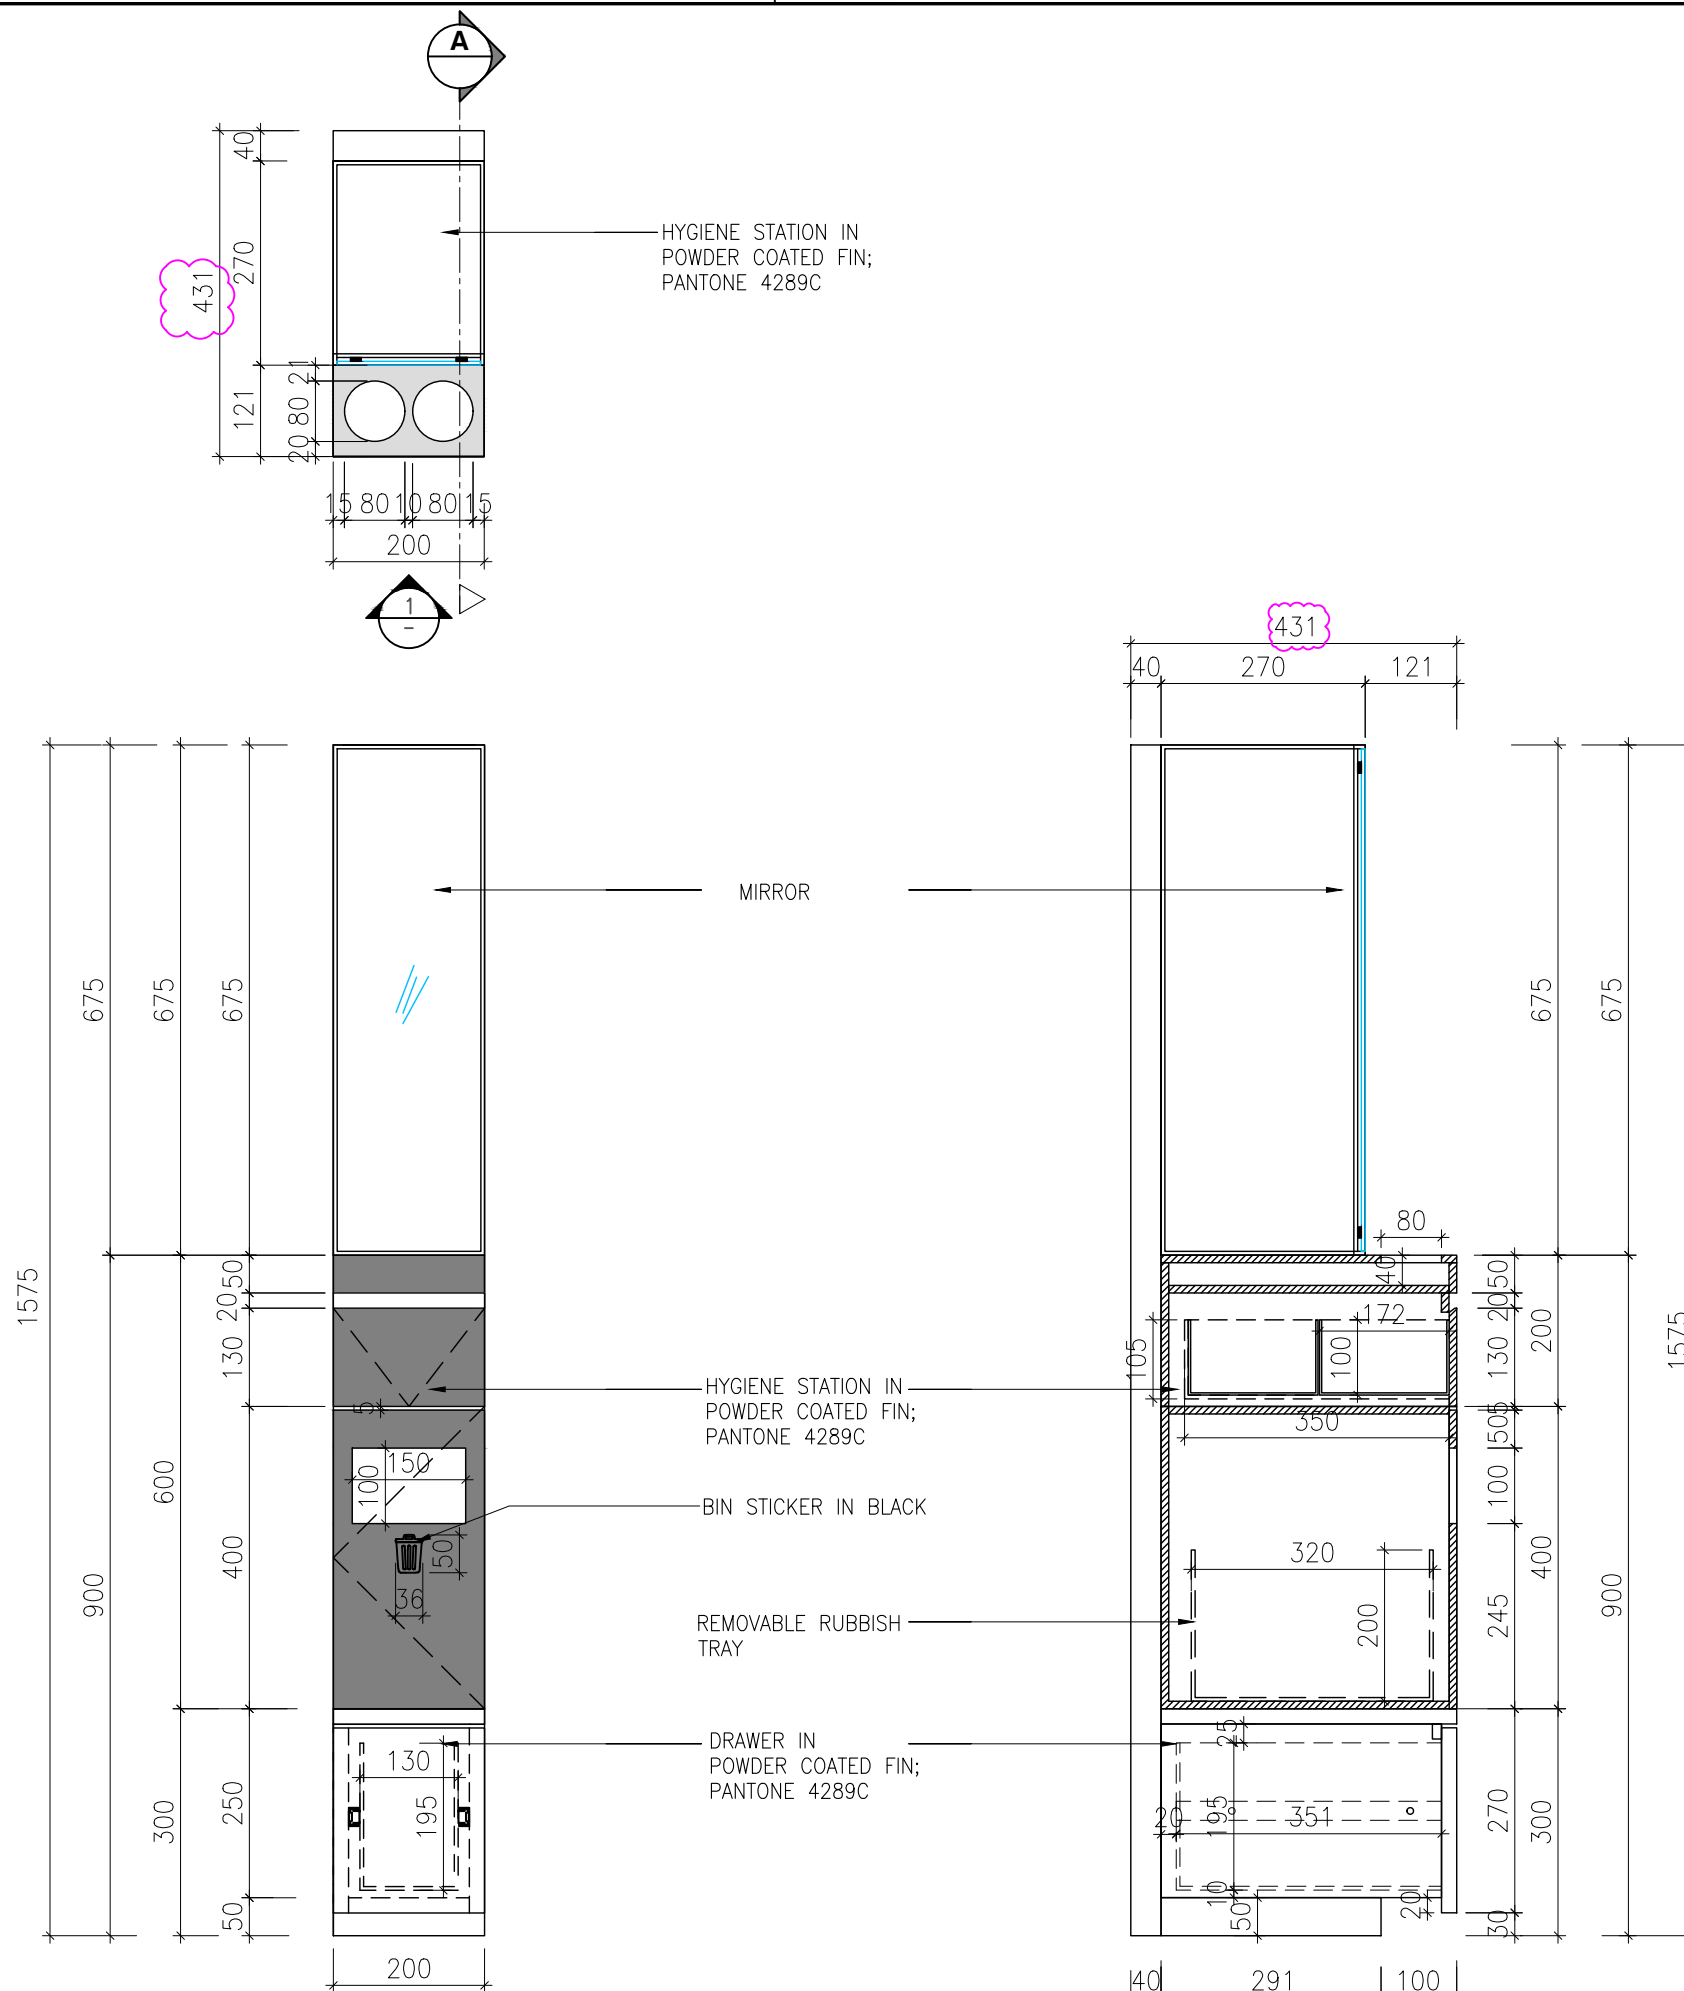

2 ELEVATION 1
SCALE 1:10

3 ELEVATION 2
SCALE 1:10


Rev	Date	Description
Client:		
Project:		
FRAN @ BUGIS+ (#01-04)		
Project Management:		
 Studio J Solutions Pte. Ltd.		
email : enquiries@studioj.sg web : www.studioj.sg Add : 7 Mandai Link #03-20 Mandai Connection Singapore 728653		
Design Consultant:		
Main Contractor:		
 Studio J Solutions Pte. Ltd.		
email : enquiries@studioj.sg web : www.studioj.sg Add : 7 Mandai Link #03-20 Mandai Connection Singapore 728653		
Mechanical & Electrical Consultant:		
Structural Engineer:		
General Notes:		
COPYRIGHT OF ALL DESIGNS AND DATA SHOWN IN THIS DRAWING IS RETAINED BY STUDIO J SOLUTION PTE.LTD. WRITTEN PERMISSION IS REQUIRED FOR ANY USE AND/OR REPRODUCTION. ALL PRINTS, SPECIFICATIONS AND COPYRIGHTS ARE THE PROPERTY OF STUDIO J SOLUTION PTE.LTD. AND SHALL BE RETURNED ON COMPLETION OF WORKS. ALL MEASUREMENTS MUST BE CHECKED AT SITE BY THE CONTRACTOR AND NOTIFICATION TO BE MADE TO THE DESIGNER BEFORE COMMENCEMENT OF WORK IN THE EVENT OF ANY DISCREPANCIES ARISING FROM THE DRAWINGS. ALL DRAWINGS MUST BE READ IN CONJUNCTION WITH OTHER CONSULTANT DRAWINGS.		
Drawn :		
WILLIAM		
Checked:		
JF		
Approved:		
First submission date:		
Scale :		
A3 AS SHOWN		
Drawing Title:		
HYGIENE STATION MAKEUP		
Drawing Number:		
HS-M		
Project Number:		
FRAN_BUGIS+_270726		

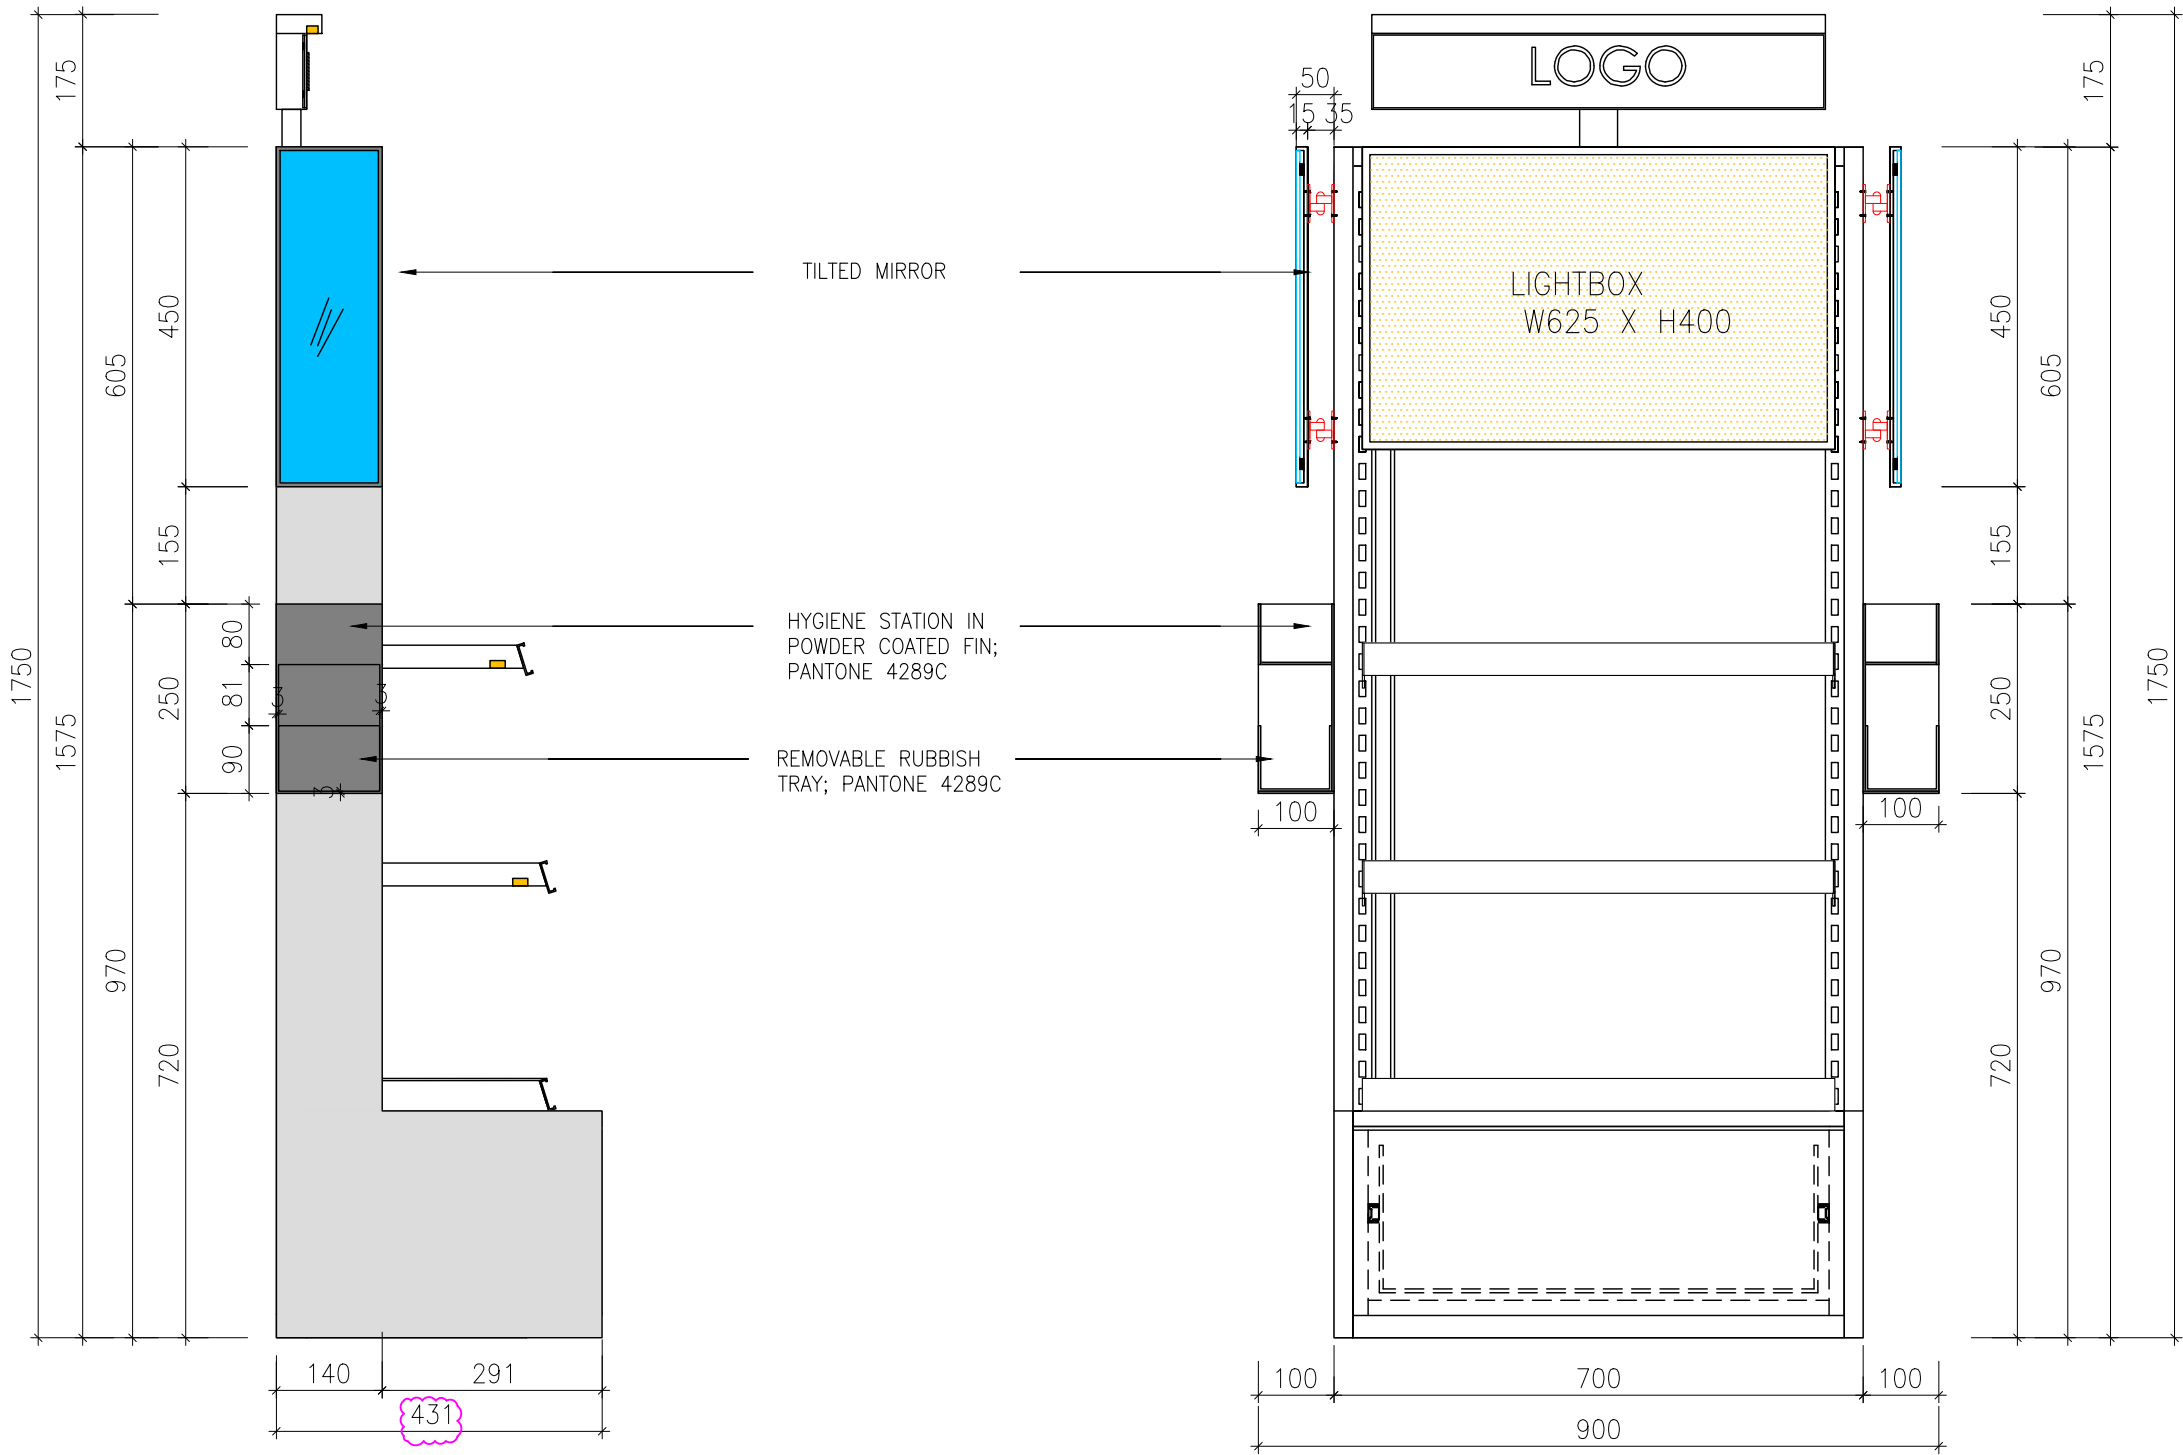


1 FRONT ELEVATION
SCALE 1:10

2 SIDE ELEVATION
SCALE 1:10

Rev	Date	Description
Client:		
Project:		
FRAN @ BUGIS+ (#01-04)		
Project Management:		
 Studio J Solutions Pte. Ltd.		
email : enquiries@studioj.sg web : www.studioj.sg Add : 7 Mandai Link #03-20 Mandai Connection Singapore 728653		
Design Consultant:		
Main Contractor:		
 Studio J Solutions Pte. Ltd.		
email : enquiries@studioj.sg web : www.studioj.sg Add : 7 Mandai Link #03-20 Mandai Connection Singapore 728653		
Mechanical & Electrical Consultant:		
Structural Engineer:		
General Notes:		
COPYRIGHT OF ALL DESIGNS AND DATA SHOWN IN THIS DRAWING IS RETAINED BY STUDIO J SOLUTION PTE.LTD. WRITTEN PERMISSION IS REQUIRED FOR ANY USE AND/OR REPRODUCTION. ALL PRINTS, SPECIFICATIONS AND COPYRIGHTS ARE THE PROPERTY OF STUDIO J SOLUTION PTE.LTD. AND SHALL BE RETURNED ON COMPLETION OF WORKS. ALL MEASUREMENTS MUST BE CHECKED AT SITE BY THE CONTRACTOR AND NOTIFICATION TO BE MADE TO THE DESIGNER BEFORE COMMENCEMENT OF WORK IN THE EVENT OF ANY DISCREPANCIES ARISING FROM THE DRAWINGS. ALL DRAWINGS MUST BE READ IN CONJUNCTION WITH OTHER CONSULTANT DRAWINGS.		
Drawn :		
WILLIAM		
Checked:		
JF		
Approved:		
First submission date:		
Scale :		
A3 AS SHOWN		
Drawing Title:		
HYGIENE STATION MAKEUP		
Drawing Number:		
HS-M		
Project Number:		
FRAN_BUGIS+_270726		

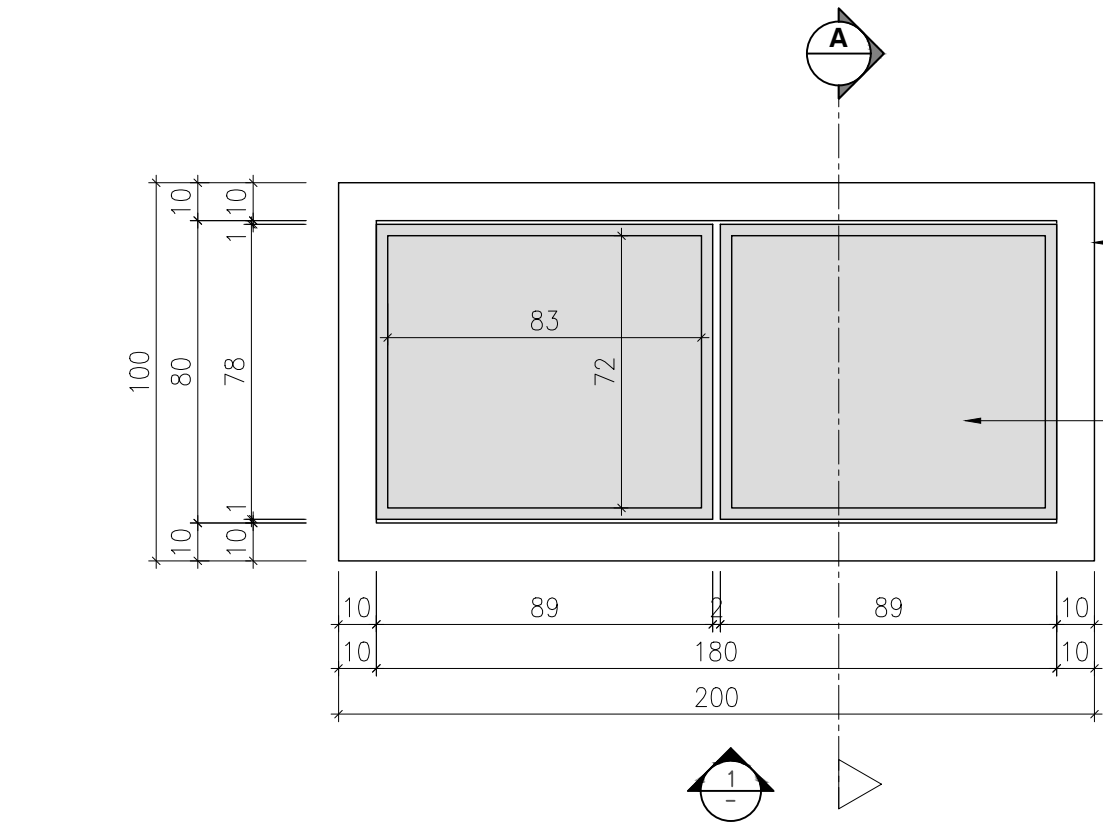

1 PLAN
SCALE 1:2

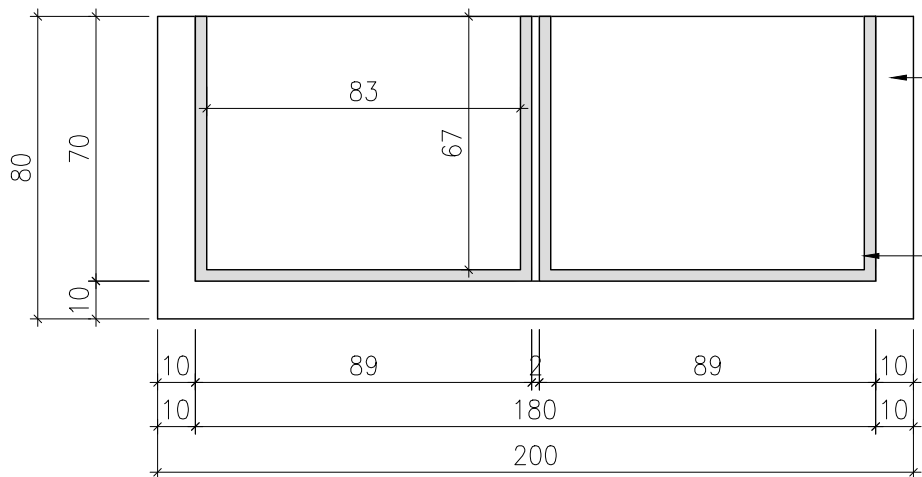


2 ELEVATION 1
SCALE 1:2

HYGIENE TRAY
POWDER COATED FIN;
PANTONE 4289C

3MM THK;
ARCRYLIC BOX

HYGIENE TRAY
POWDER COATED FIN;
PANTONE 4289C

3MM THK;
ARCRYLIC BOX

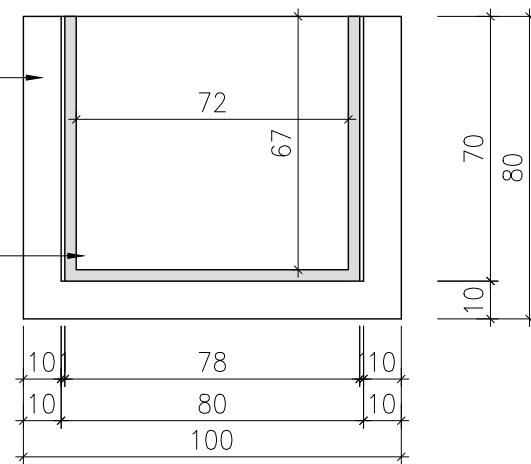

3 SECTION A
SCALE 1:2

Rev	Date	Description
Client:		
Project :		
FRAN @ BUGIS+ (#01-04)		
Project Management:		
 Studio J Solutions Pte. Ltd email : enquiries@studioj.sg web : www.studioj.sg Add : 7 Mandai Link #03-20 Mandai Connection Singapore 728653		
Design Consultant:		
Main Contractor:		
 Studio J Solutions Pte. Ltd email : enquiries@studioj.sg web : www.studioj.sg Add : 7 Mandai Link #03-20 Mandai Connection Singapore 728653		
Mechanical & Electrical Consultant:		
Structural Engineer:		
General Notes:		
COPYRIGHT OF ALL DESIGNS AND DATA SHOWN IN THIS DRAWING IS RETAINED BY STUDIO J SOLUTION PTE.LTD. WRITTEN PERMISSION IS REQUIRED FOR ANY USE AND/OR REPRODUCTION. ALL PRINTS, SPECIFICATIONS AND COPYRIGHTS ARE THE PROPERTY OF STUDIO J SOLUTION PTE.LTD. AND SHALL BE RETURNED ON COMPLETION OF WORKS. ALL MEASUREMENTS MUST BE CHECKED AT SITE BY THE CONTRACTOR AND NOTIFICATION TO BE MADE TO THE DESIGNER BEFORE COMMENCEMENT OF WORK IN THE EVENT OF ANY DISCREPANCIES ARISING FROM THE DRAWINGS. ALL DRAWINGS MUST BE READ IN CONJUNCTION WITH OTHER CONSULTANT DRAWINGS.		
Drawn :		
WILLIAM		
Checked:		
JF		
Approved:		
First submission date:		
Scale :		
A3 AS SHOWN		
Drawing Title:		
HYGIENE TRAY SKINCARE,HAIR,FRAGRANCE		
Drawing Number:		
HT-01		
Project Number:		
FRAN_BUGIS+_270726		

HYGIENE STATION IN
POWDER COATED FIN;
PANTONE 4289C

ENDCAP IN
POWDER COATED FIN;
PANTONE 4289C

GONDOLA IN
POWDER COATED FIN;
PANTONE 4289C

1

PLAN

—

SCALE

1:15



ENDCAP IN
POWDER COATED FIN;
PANTONE 4289C

HYGIENE STATION IN
POWDER COATED FIN;
PANTONE 4289C

GONDOLA IN
POWDER COATED FIN;
PANTONE 4289C

2


ELEVATION 1

—



SCALE

1:15

Rev	Date	Description
Client:		
Project:		
FRAN @ BUGIS+ (#01-04)		
Project Management:		
		
Studio J Solutions Pte. Ltd		
email : enquiries@studioj.sg web : www.studioj.sg Add : 7 Mandai Link #03-20 Mandai Connection Singapore 728653		
Design Consultant:		
Main Contractor:		
		
Studio J Solutions Pte. Ltd		
email : enquiries@studioj.sg web : www.studioj.sg Add : 7 Mandai Link #03-20 Mandai Connection Singapore 728653		
Mechanical & Electrical Consultant:		
Structural Engineer:		
General Notes:		
COPYRIGHT OF ALL DESIGNS AND DATA SHOWN IN THIS DRAWING IS RETAINED BY STUDIO J SOLUTION PTE.LTD. WRITTEN PERMISSION IS REQUIRED FOR ANY USE AND/OR REPRODUCTION. ALL PRINTS, SPECIFICATIONS AND COPYRIGHTS ARE THE PROPERTY OF STUDIO J SOLUTION PTE.LTD. AND SHALL BE RETURNED ON COMPLETION OF WORKS. ALL MEASUREMENTS MUST BE CHECKED AT SITE BY THE CONTRACTOR AND NOTIFICATION TO BE MADE TO THE DESIGNER BEFORE COMMENCEMENT OF WORK IN THE EVENT OF ANY DISCREPANCIES ARISING FROM THE DRAWINGS. ALL DRAWINGS MUST BE READ IN CONJUNCTION WITH OTHER CONSULTANT DRAWINGS.		
Drawn :		
WILLIAM		
Checked:		
JF		
Approved:		
First submission date:		
Scale :		
A3 AS SHOWN		
Drawing Title:		
GONDOLA+ENDCAP+HYGIENE		
Drawing Number:		
DT-1		
Project Number:		
FRAN_BUGIS+_270726		

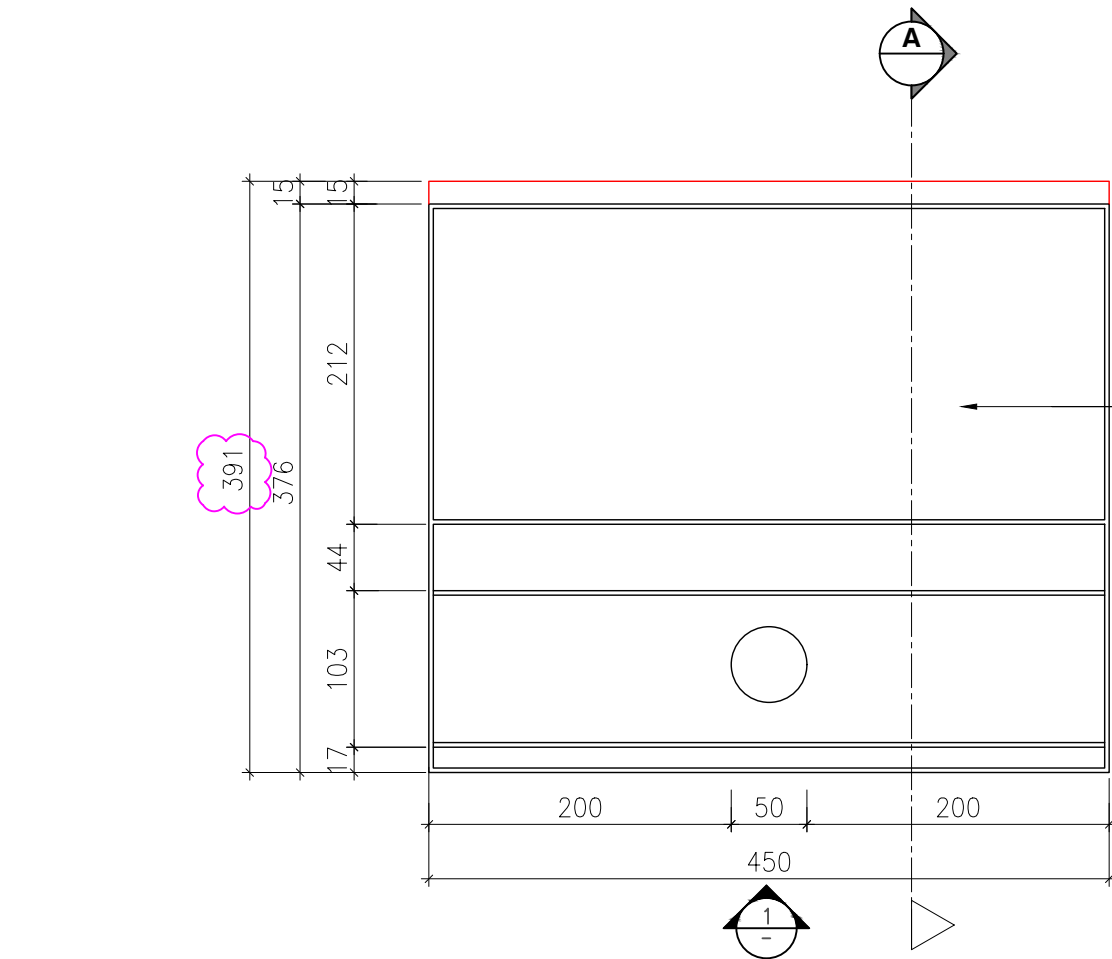

1 PLAN
SCALE 1:5

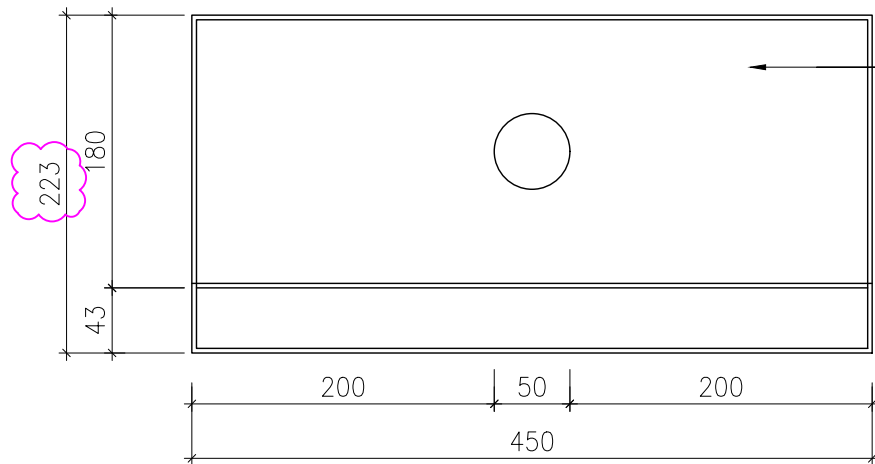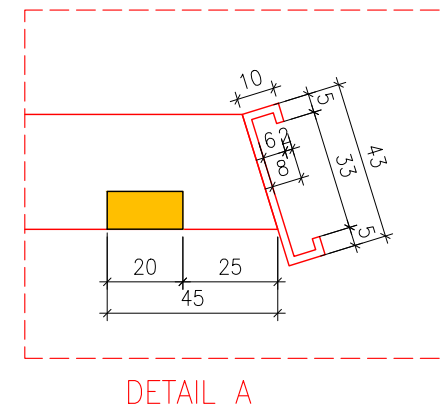


2 ELEVATION 1
SCALE 1:5

MAKEUP DRAWER IN
BLACK PAINT FIN;

DRAWER RUNNER

SHELF WITH LED
LIGHT 6000K

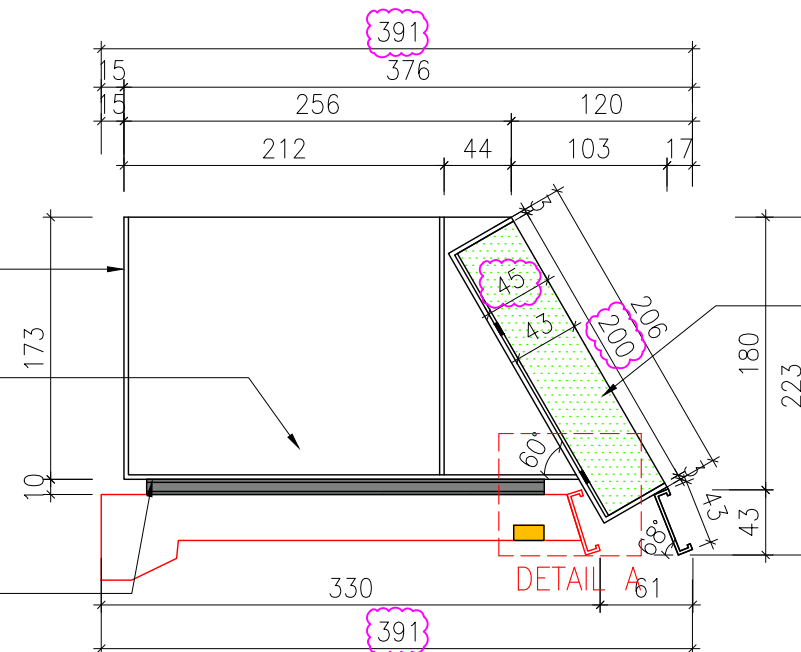


3 SECTION A
SCALE 1:5

PLANOGRAM WITH
MAGNETS


Rev	Date	Description
Client:		
Project:		
FRAN @ BUGIS+ (#01-04)		
Project Management:		
 Studio J Solutions Pte. Ltd		
email : enquiries@studioj.sg web : www.studioj.sg Add : 7 Mandai Link #03-20 Mandai Connection Singapore 728653		
Design Consultant:		
Main Contractor:		
 Studio J Solutions Pte. Ltd		
email : enquiries@studioj.sg web : www.studioj.sg Add : 7 Mandai Link #03-20 Mandai Connection Singapore 728653		
Mechanical & Electrical Consultant:		
Structural Engineer:		
General Notes:		
COPYRIGHT OF ALL DESIGNS AND DATA SHOWN IN THIS DRAWING IS RETAINED BY STUDIO J SOLUTION PTE.LTD. WRITTEN PERMISSION IS REQUIRED FOR ANY USE AND/OR REPRODUCTION. ALL PRINTS, SPECIFICATIONS AND COPYRIGHTS ARE THE PROPERTY OF STUDIO J SOLUTION PTE.LTD. AND SHALL BE RETURNED ON COMPLETION OF WORKS. ALL MEASUREMENTS MUST BE CHECKED AT SITE BY THE CONTRACTOR AND NOTIFICATION TO BE MADE TO THE DESIGNER BEFORE COMMENCEMENT OF WORK IN THE EVENT OF ANY DISCREPANCIES ARISING FROM THE DRAWINGS. ALL DRAWINGS MUST BE READ IN CONJUNCTION WITH OTHER CONSULTANT DRAWINGS.		
Drawn :		
WILLIAM		
Checked:		
JF		
Approved:		
First submission date:		
Scale :		
A3 AS SHOWN		
Drawing Title:		
MAKEUP DRAWER WALLBAY		
Drawing Number:		
MD-WB		
Project Number:		
FRAN_BUGIS+_270726		



Rev	Date	Description
Client:		
Project :	FRAN @ BUGIS+ (#01-04)	
Project Management:	 Studio J Solutions Pte. Ltd email : enquiries@studioj.sg web : www.studioj.sg Add : 7 Mandalink #03-20 Mandal Connection Singapore 728653	
Design Consultant:		
Main Contractor:	 Studio J Solutions Pte. Ltd email : enquiries@studioj.sg web : www.studioj.sg Add : 7 Mandalink #03-20 Mandal Connection Singapore 728653	
Mechanical & Electrical Consultant:		
Structural Engineer:		
General Notes:	COPYRIGHT OF ALL DESIGNS AND DATA SHOWN IN THIS DRAWING IS RETAINED BY STUDIO J SOLUTION PTE.LTD. WRITTEN PERMISSION IS REQUIRED FOR ANY USE AND/OR REPRODUCTION. ALL PRINTS, SPECIFICATIONS AND COPYRIGHTS ARE THE PROPERTY OF STUDIO J SOLUTION PTE.LTD. ALL MEASUREMENTS MUST BE CHECKED AT SITE BY THE CONTRACTOR AND NOTIFICATION TO BE MADE TO THE DESIGNER BEFORE COMMENCEMENT OF WORK. IN THE EVENT OF ANY DISCREPANCIES ARISING FROM THE DRAWINGS, ALL DRAWINGS MUST BE READ IN CONJUNCTION WITH OTHER CONSULTANT DRAWINGS.	
Drawn :	WILLIAM	
Checked :	JF	
Approved :		
First submission date:		
Scale :	A3 AS SHOWN	
Drawing Title:	MAKEUP DRAWER GONDOLA	
Drawing Number:	MD-G1	
Project Number:	FRAN_BUGIS+_270726	

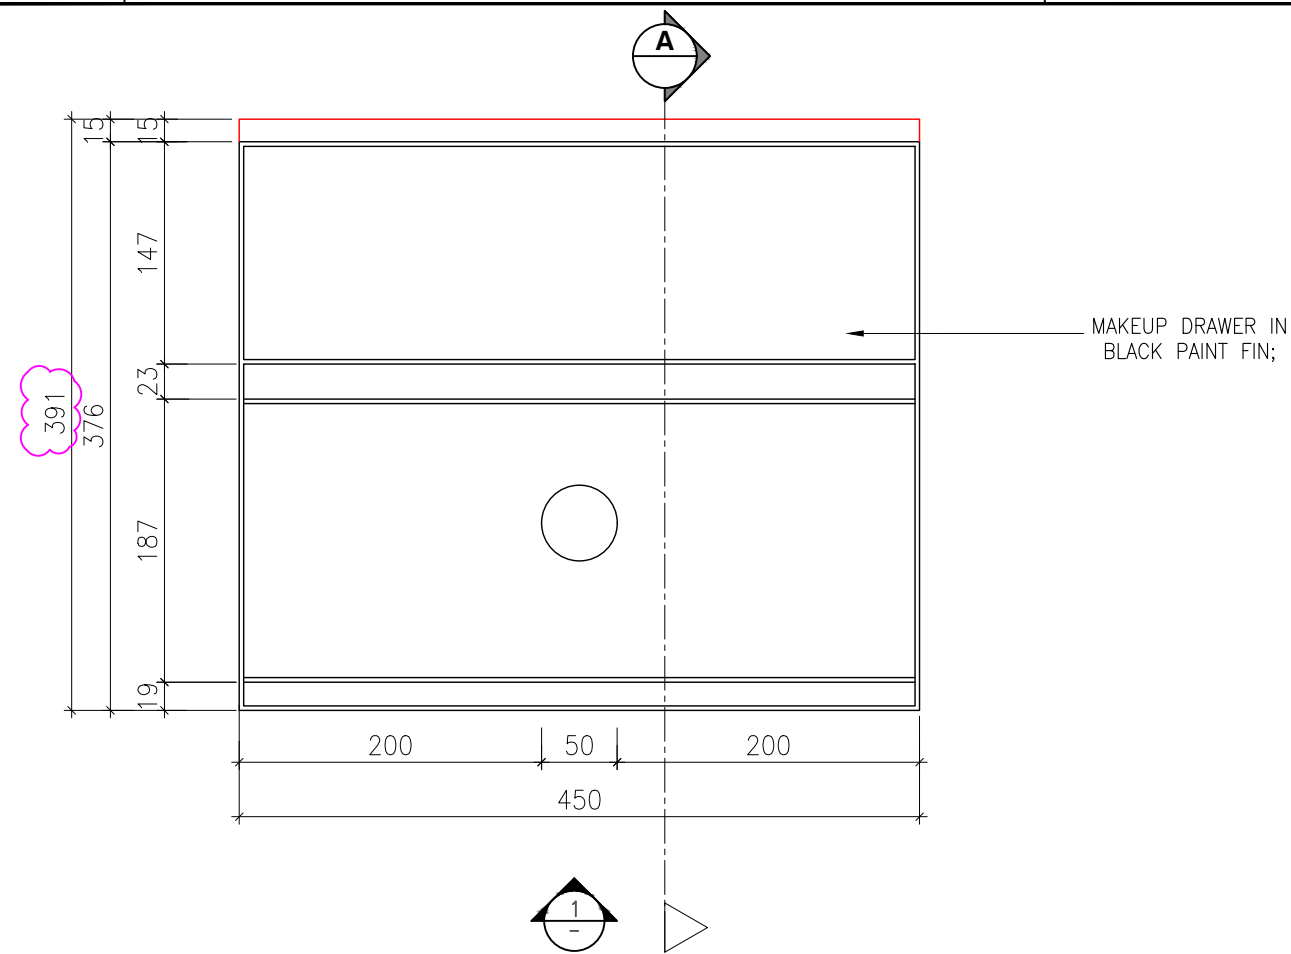

1 PLAN
SCALE 1:5

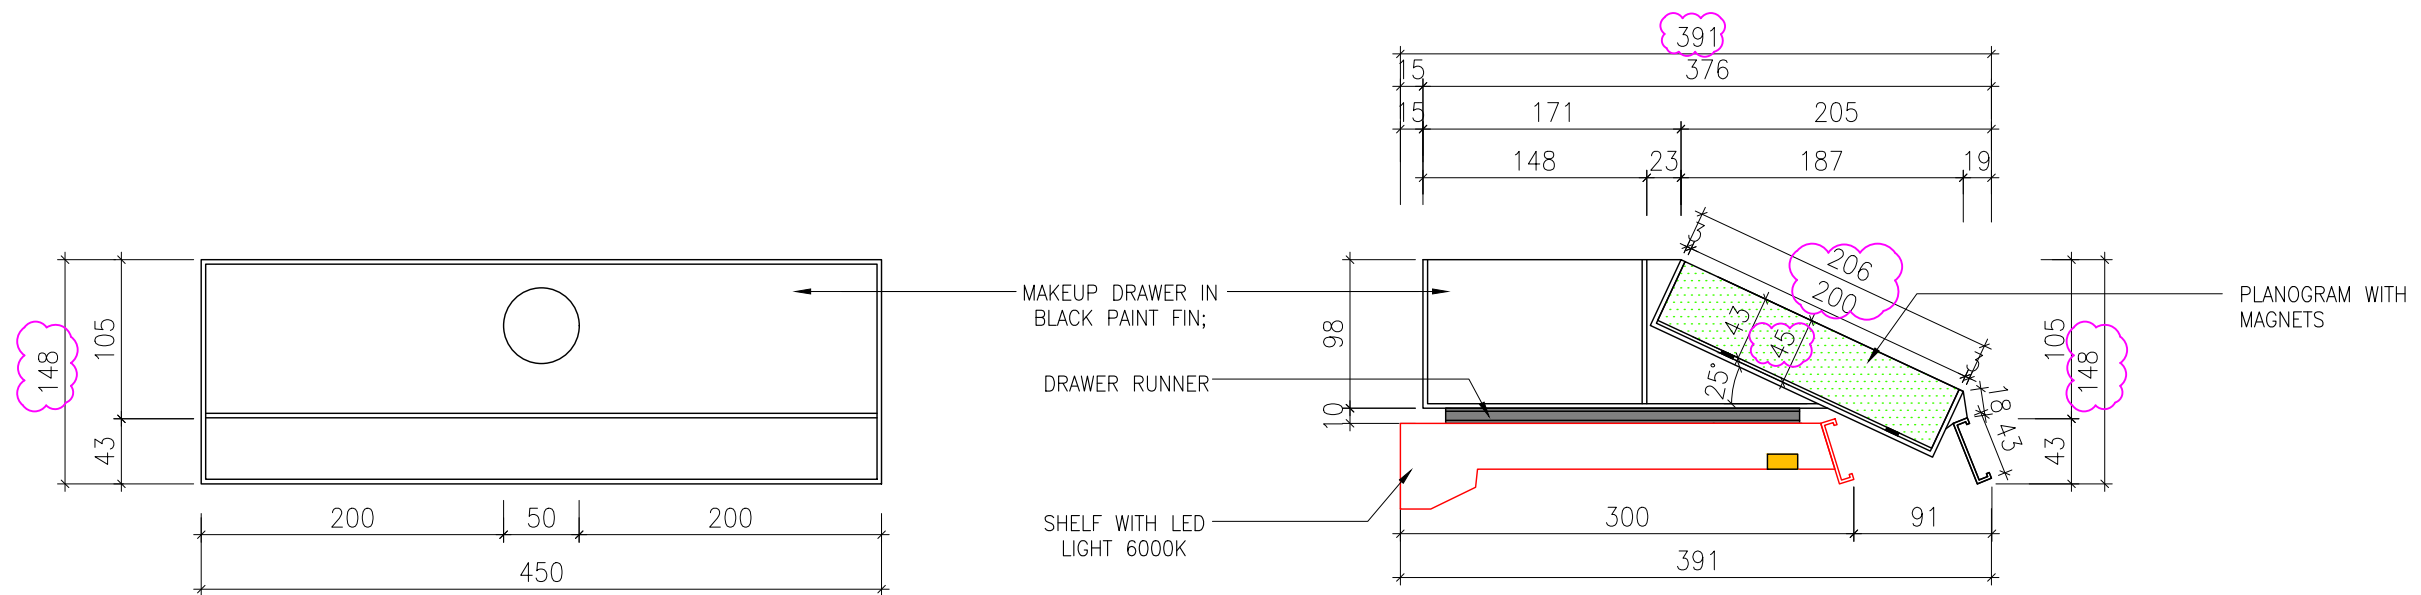


2 ELEVATION 1
SCALE 1:5


3 SECTION A
SCALE 1:5

Rev	Date	Description
Client:		
Project:		
FRAN @ BUGIS+ (#01-04)		
Project Management:		
 Studio J Solutions Pte. Ltd.		
email : enquiries@studioj.sg web : www.studioj.sg Add : 7 Mandai Link #03-20 Mandai Connection Singapore 728653		
Design Consultant:		
Main Contractor:		
 Studio J Solutions Pte. Ltd.		
email : enquiries@studioj.sg web : www.studioj.sg Add : 7 Mandai Link #03-20 Mandai Connection Singapore 728653		
Mechanical & Electrical Consultant:		
Structural Engineer:		
General Notes:		
COPYRIGHT OF ALL DESIGNS AND DATA SHOWN IN THIS DRAWING IS RETAINED BY STUDIO J SOLUTION PTE.LTD. WRITTEN PERMISSION IS REQUIRED FOR ANY USE AND/OR REPRODUCTION. ALL PRINTS, SPECIFICATIONS AND COPYRIGHTS ARE THE PROPERTY OF STUDIO J SOLUTION PTE.LTD. AND SHALL BE RETURNED ON COMPLETION OF WORKS. ALL MEASUREMENTS MUST BE CHECKED AT SITE BY THE CONTRACTOR AND NOTIFICATION TO BE MADE TO THE DESIGNER BEFORE COMMENCEMENT OF WORK IN THE EVENT OF ANY DISCREPANCIES ARISING FROM THE DRAWINGS. ALL DRAWINGS MUST BE READ IN CONJUNCTION WITH OTHER CONSULTANT DRAWINGS.		
Drawn :		
WILLIAM		
Checked:		
JF		
Approved:		
First submission date:		
Scale :		
A3 AS SHOWN		
Drawing Title:		
MAKEUP DRAWER GONDOLA		
Drawing Number:		
MD-G2		
Project Number:		
FRAN_BUGIS+_270726		

Rev	Date	Description
Client:		
Project:		
FRAN @ BUGIS+ (#01-04)		
Project Management:		
 Studio J Solutions Pte. Ltd		
email : enquiries@studioj.sg web : www.studioj.sg Add : 7 Mandai Link #03-20 Mandai Connection Singapore 728653		
Design Consultant:		
Main Contractor:		
 Studio J Solutions Pte. Ltd		
email : enquiries@studioj.sg web : www.studioj.sg Add : 7 Mandai Link #03-20 Mandai Connection Singapore 728653		
Mechanical & Electrical Consultant:		
Structural Engineer:		
General Notes:		
COPYRIGHT OF ALL DESIGNS AND DATA SHOWN IN THIS DRAWING IS RETAINED BY STUDIO J SOLUTION PTE.LTD. WRITTEN PERMISSION IS REQUIRED FOR ANY USE AND/OR REPRODUCTION. ALL PRINTS, SPECIFICATIONS AND COPYRIGHTS ARE THE PROPERTY OF STUDIO J SOLUTION PTE.LTD. AND SHALL BE RETURNED ON COMPLETION OF WORKS. ALL MEASUREMENTS MUST BE CHECKED AT SITE BY THE CONTRACTOR AND NOTIFICATION TO BE MADE TO THE DESIGNER BEFORE COMMENCEMENT OF WORK IN THE EVENT OF ANY DISCREPANCIES ARISING FROM THE DRAWINGS. ALL DRAWINGS MUST BE READ IN CONJUNCTION WITH OTHER CONSULTANT DRAWINGS.		
Drawn :		
WILLIAM		
Checked:		
JF		
Approved:		
First submission date:		
Scale :		
A3 AS SHOWN		
Drawing Title:		
MAKEUP DRAWER ENDCAP		
Drawing Number:		
MD-E1		
Project Number:		
FRAN_BUGIS+_270726		



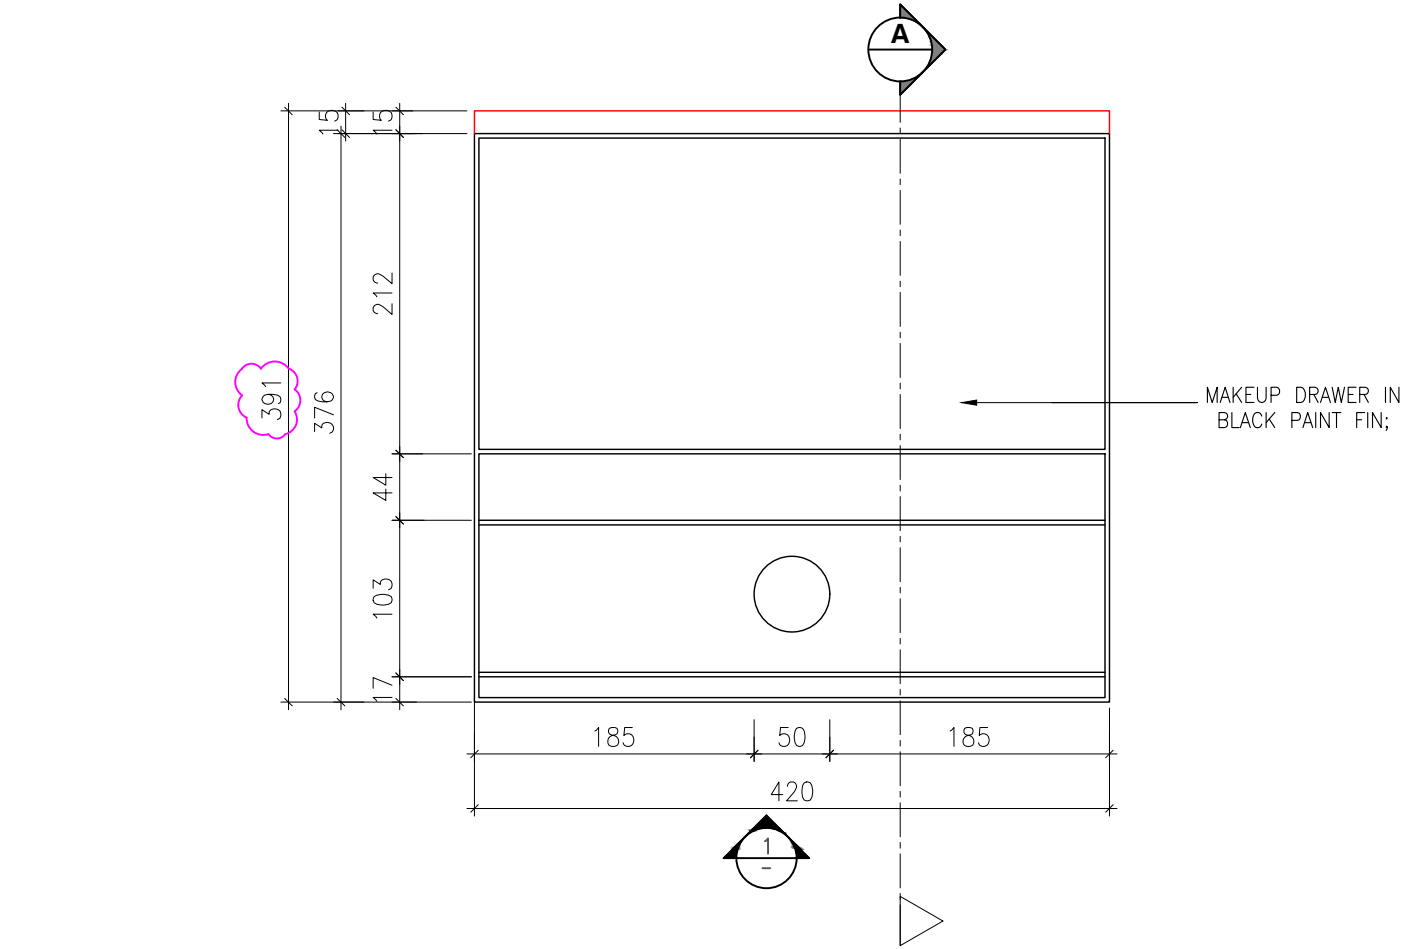


1 PLAN
SCALE 1:5

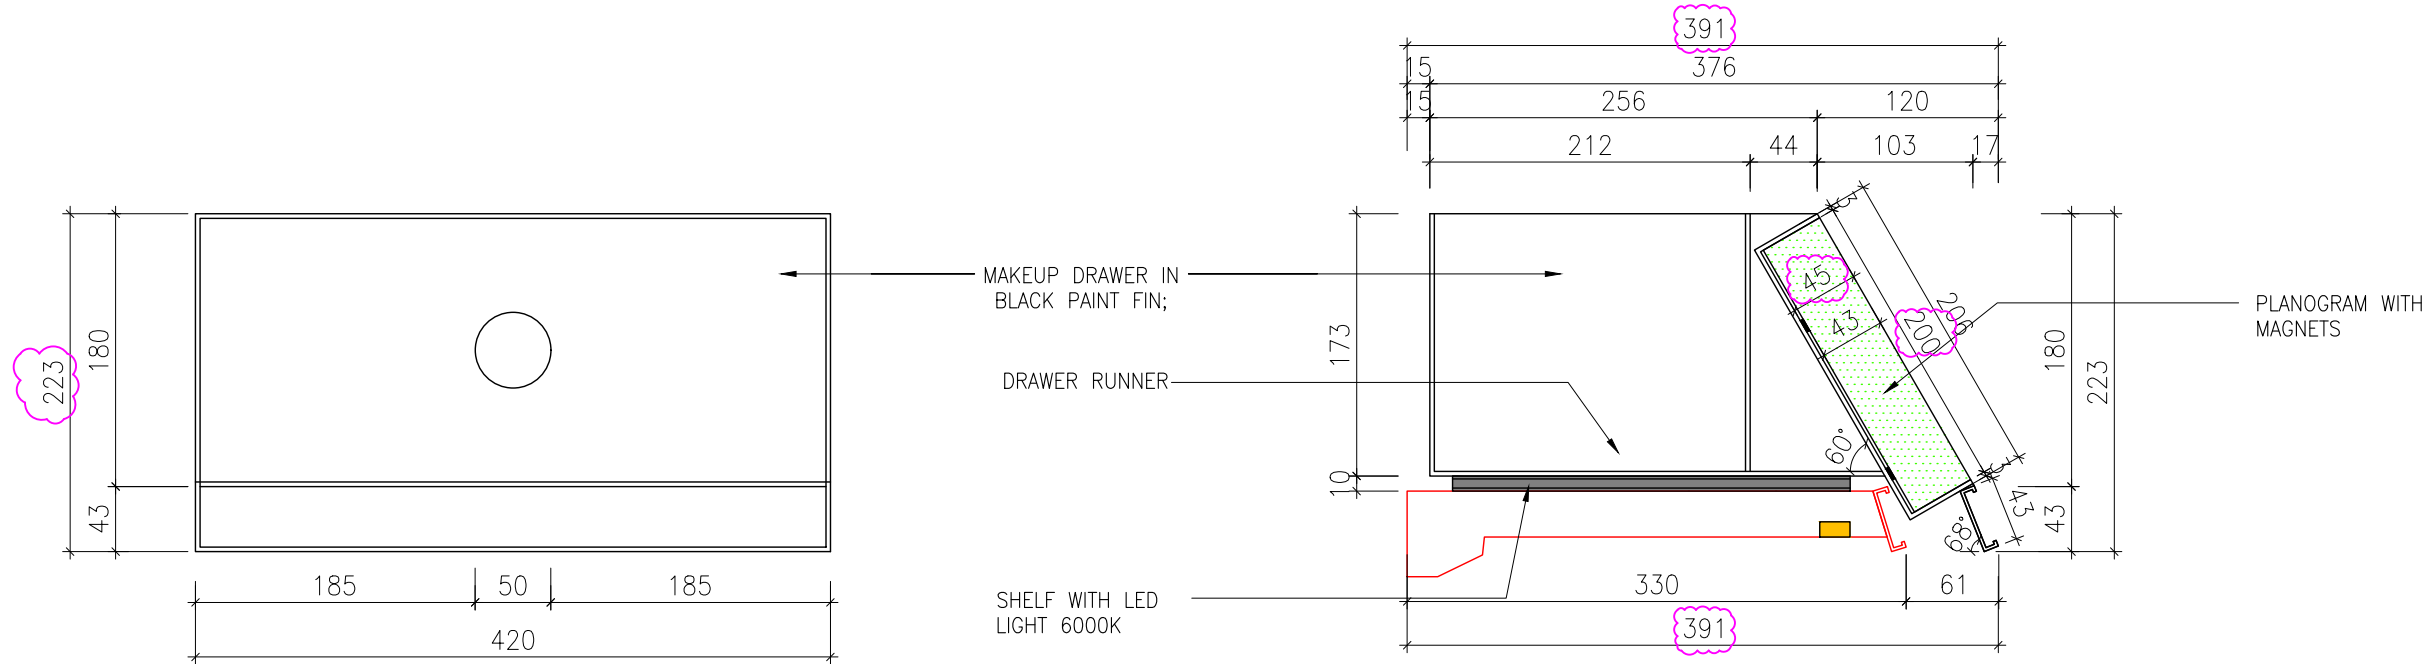

2 ELEVATION 1
SCALE 1:5

3 SECTION A
SCALE 1:5

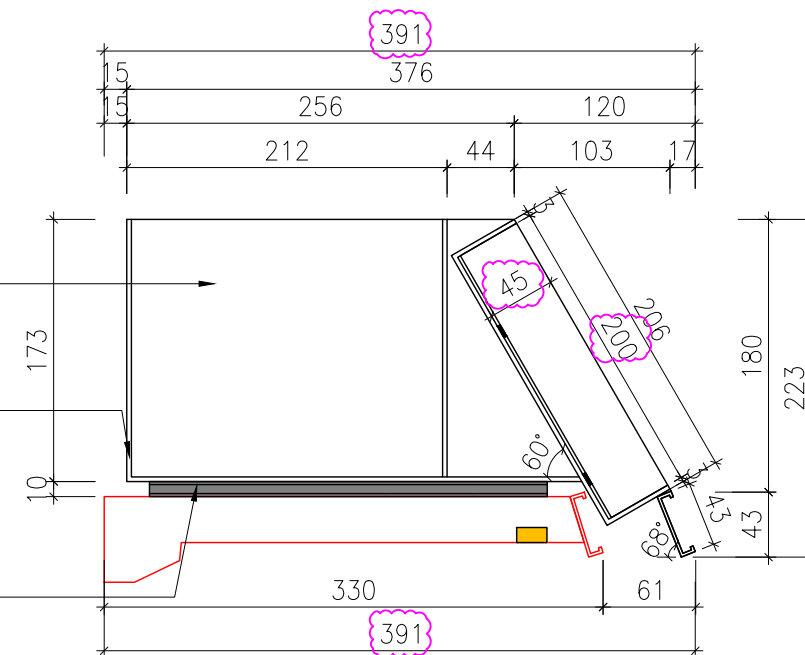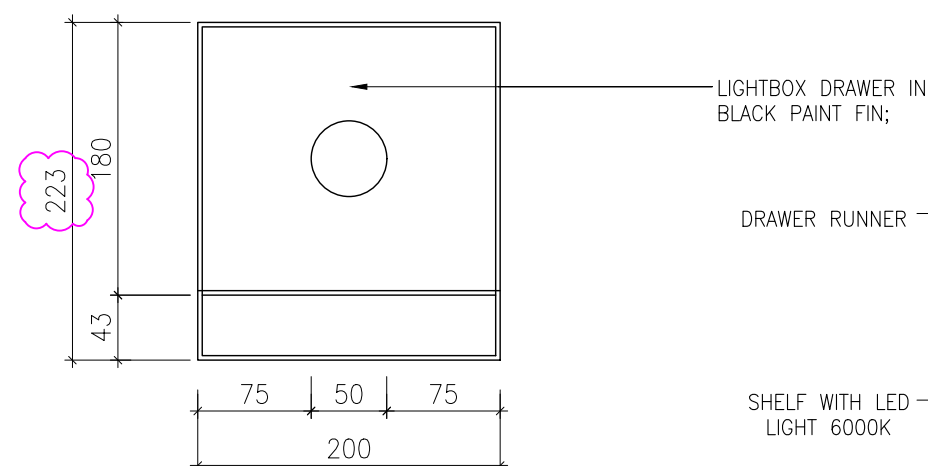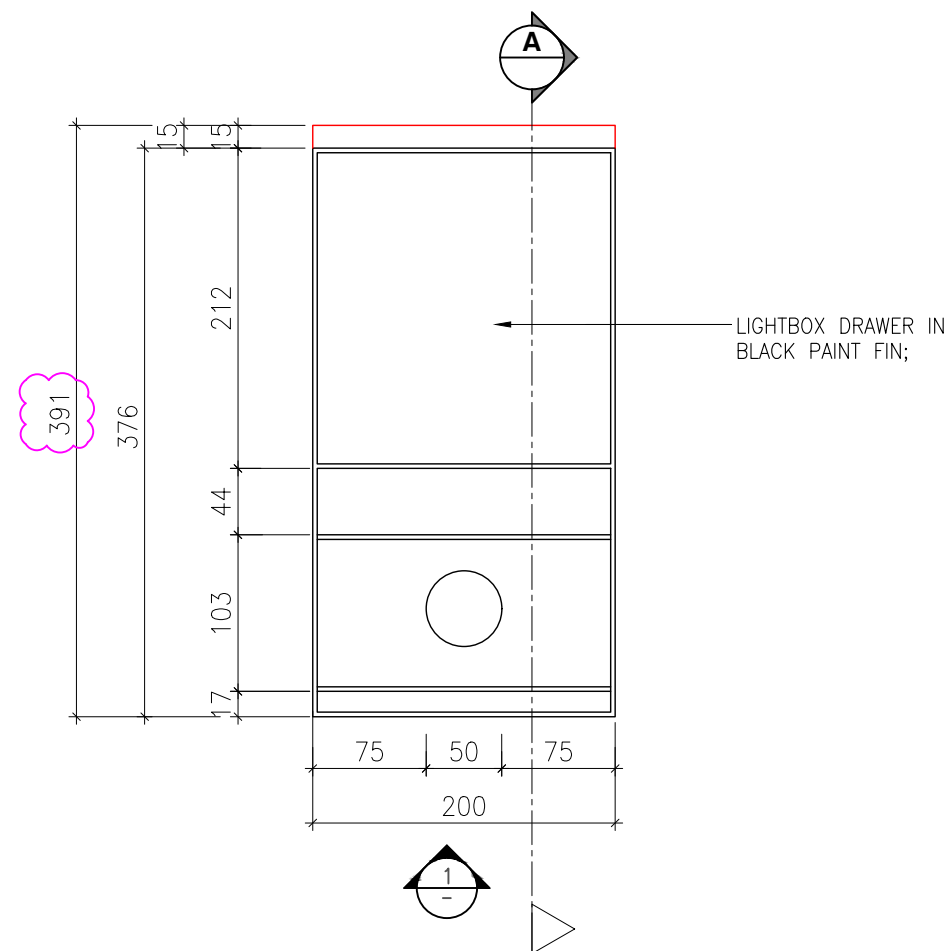

Rev	Date	Description
Client:		
Project :	FRAN @ BUGIS+ (#01-04)	
Project Management:		
 Studio J Solutions Pte. Ltd email : enquiries@studioj.sg web : www.studioj.sg Add : 7 Mandai Link #03-20 Mandai Connection Singapore 728653		
Design Consultant:		
Main Contractor:		
 Studio J Solutions Pte. Ltd email : enquiries@studioj.sg web : www.studioj.sg Add : 7 Mandai Link #03-20 Mandai Connection Singapore 728653		
Mechanical & Electrical Consultant:		
Structural Engineer:		
General Notes:		
COPYRIGHT OF ALL DESIGNS AND DATA SHOWN IN THIS DRAWING IS RETAINED BY STUDIO J SOLUTION PTE.LTD. WRITTEN PERMISSION IS REQUIRED FOR ANY USE AND/OR REPRODUCTION. ALL PRINTS, SPECIFICATIONS AND COPYRIGHTS ARE THE PROPERTY OF STUDIO J SOLUTION PTE.LTD. SHALL BE RETURNED ON COMPLETION OF WORKS. ALL MEASUREMENTS MUST BE CHECKED AT SITE BY THE CONTRACTOR AND NOTIFICATION TO BE MADE TO THE DESIGNER BEFORE COMMENCEMENT OF WORK IN THE EVENT OF ANY DISCREPANCIES ARISING FROM THE DRAWINGS. ALL DRAWINGS MUST BE READ IN CONJUNCTION WITH OTHER CONSULTANT DRAWINGS.		
Drawn :		
WILLIAM		
Checked :		
JF		
Approved:		
First submission date:		
Scale :		
A3 AS SHOWN		
Drawing Title:		
LIGHTBOX DRAWER ENDCAP		
Drawing Number:		
MD-E2		
Project Number:		
FRAN_BUGIS+ 270726		