



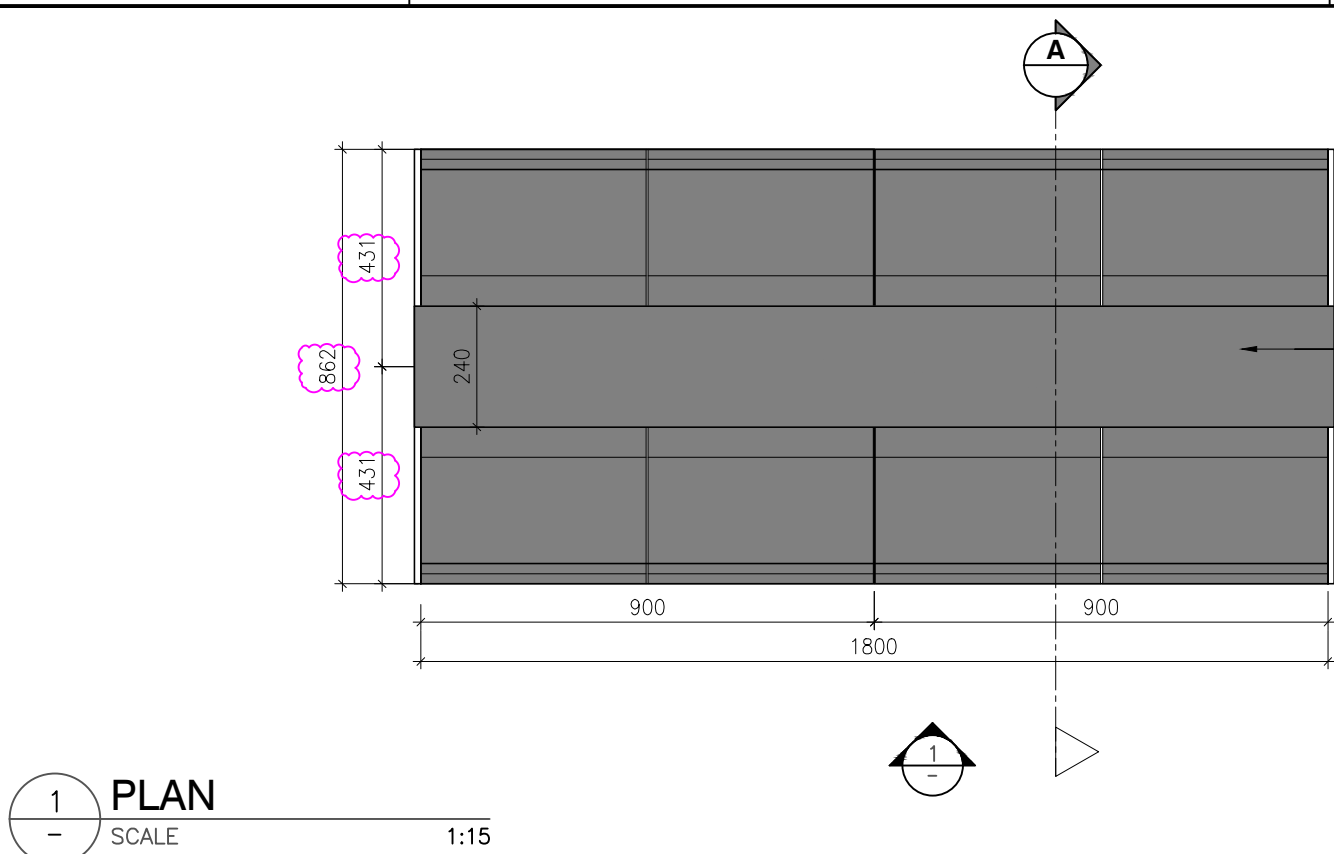


1 PLAN
SCALE 1:15

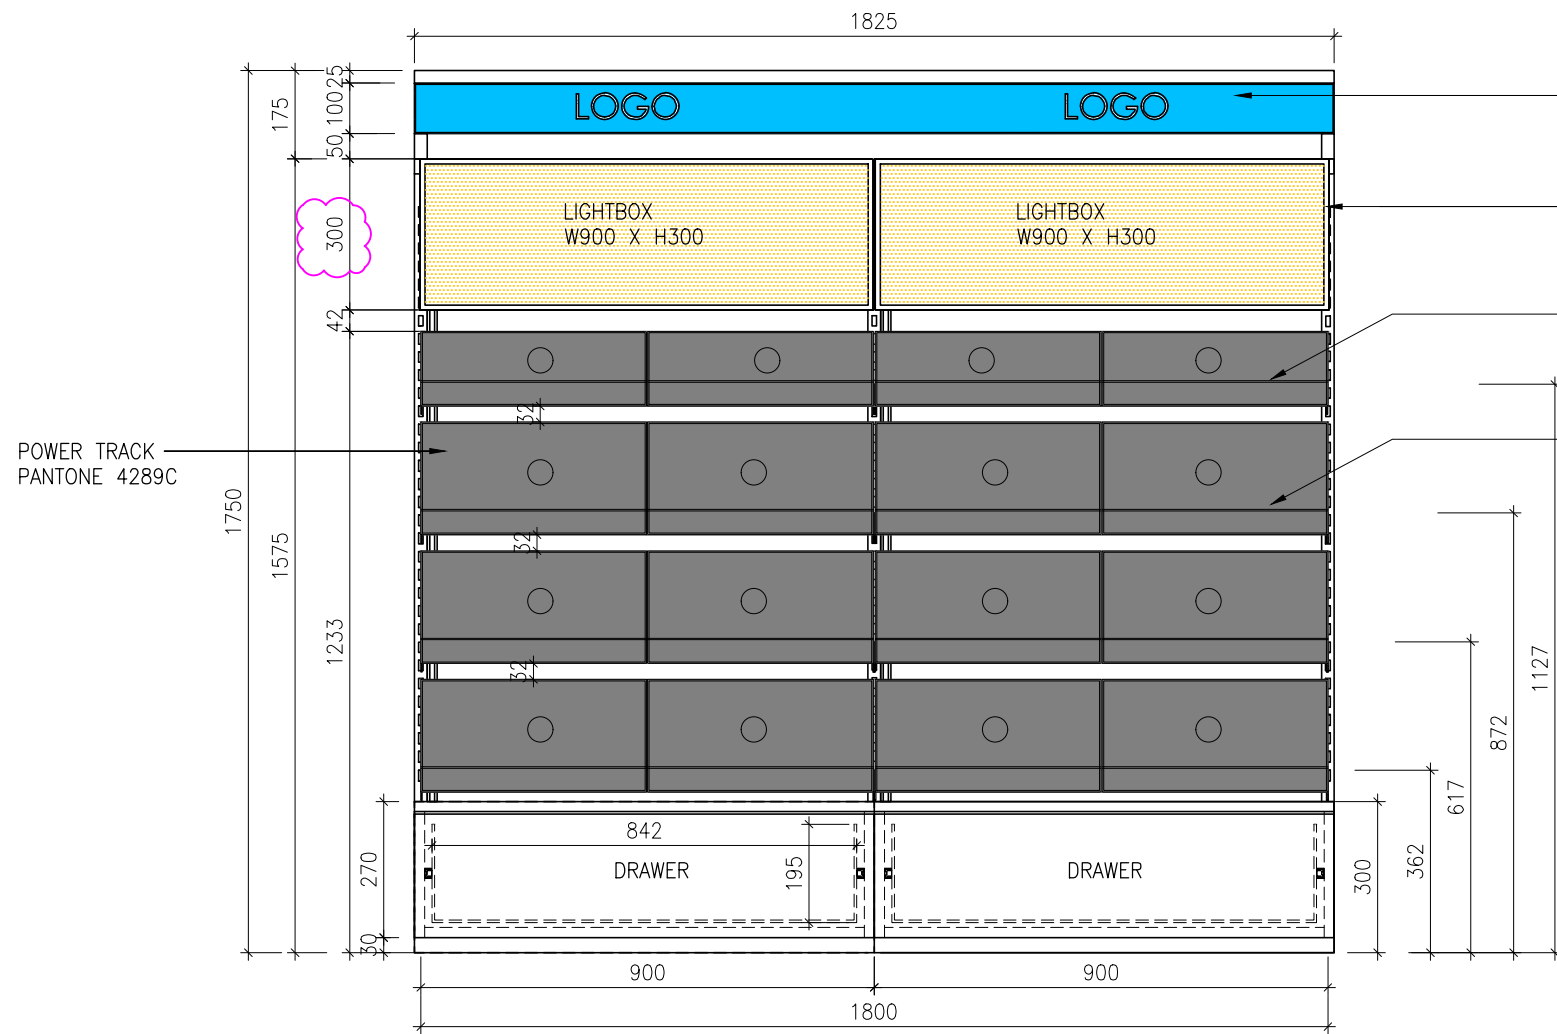

2 ELEVATION 1
SCALE 1:15

GONDOLA IN
POWDER COATED FIN;
PANTONE 4289C

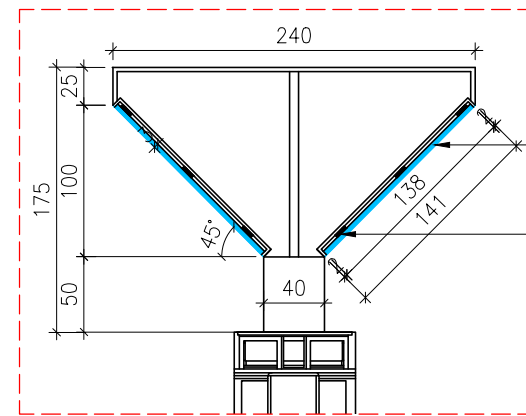

DETAIL A

DETAIL A


REMOVABLE MIRROR
WITH WHITE LOGO
STICKER

GONDOLA IN
POWDER COATED FIN;
PANTONE 4289C

MAKEUP DRAWER
W450XD376XH148

MAKEUP DRAWER
W450XD376XH223


SHELF IN PANTONE
4289C LED STRIP
LIGHT 6000K

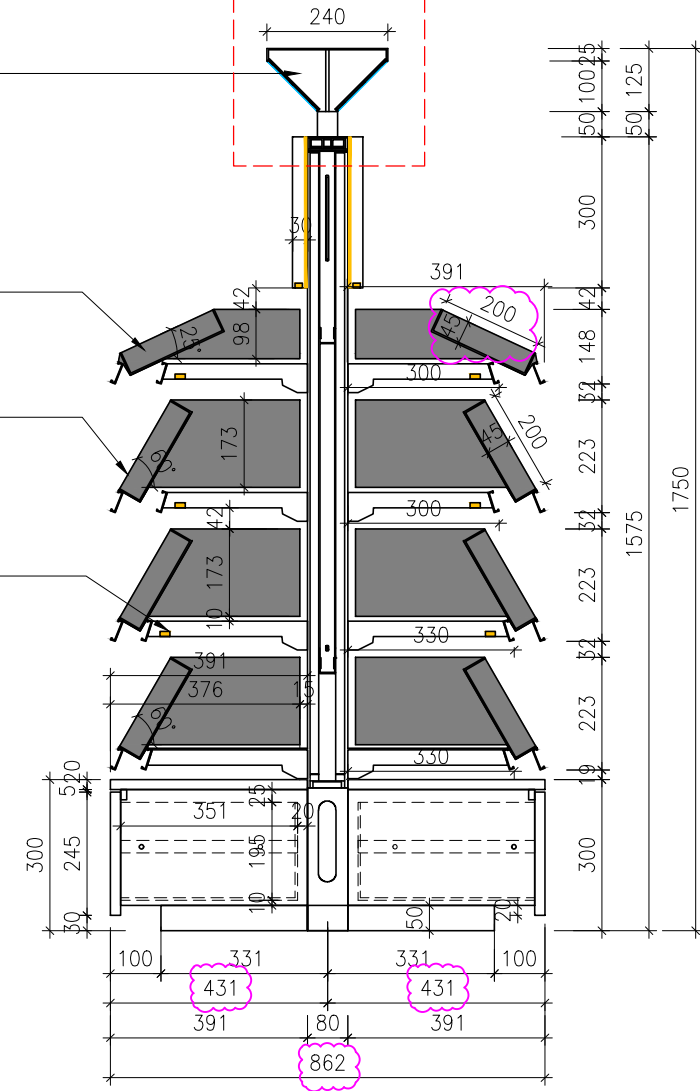


3 SECTION A
SCALE 1:15

GONDOLA	
MAKEUP	MAKEUP DRAWER + LIGHTBOX

Rev	Date	Description
Client:		
Project:		
FRAN @ BUGIS+ (#01-04)		
Project Management:		
 Studio J Solutions Pte. Ltd.		
email : enquiries@studioj.sg web : www.studioj.sg Add : 7 Mandal Link #03-20 Mandal Connection Singapore 728653		
Design Consultant:		
Main Contractor:		
 Studio J Solutions Pte. Ltd.		
email : enquiries@studioj.sg web : www.studioj.sg Add : 7 Mandal Link #03-20 Mandal Connection Singapore 728653		
Mechanical & Electrical Consultant:		
Structural Engineer:		
General Notes:		
COPYRIGHT OF ALL DESIGNS AND DATA SHOWN IN THIS DRAWING IS RETAINED BY STUDIO J SOLUTIONS PTE.LTD. WRITTEN PERMISSION IS REQUIRED FOR ANY USE AND/OR REPRODUCTION. ALL PRINTS, SPECIFICATIONS AND COPYRIGHTS ARE THE PROPERTY OF STUDIO J SOLUTIONS PTE.LTD. AND SHALL BE RETURNED ON COMPLETION OF WORKS. ALL MEASUREMENTS MUST BE CHECKED AT SITE BY THE CONTRACTOR AND NOTIFICATION TO BE MADE TO THE DESIGNER BEFORE COMMENCEMENT OF WORK. IN THE EVENT OF ANY DISCREPANCIES ARISING FROM THE DRAWINGS, ALL DRAWINGS MUST BE READ IN CONJUNCTION WITH OTHER CONSULTANT DRAWINGS.		
Drawn :		
WILLIAM		
Checked :		
JF		
Approved :		
First submission date:		
Scale :		
A3 AS SHOWN		
Drawing Title:		
GONDOLA (MAKE UP)		
Drawing Number:		
GD-M		
Project Number:		
FRAN_BUGIS+_270726		

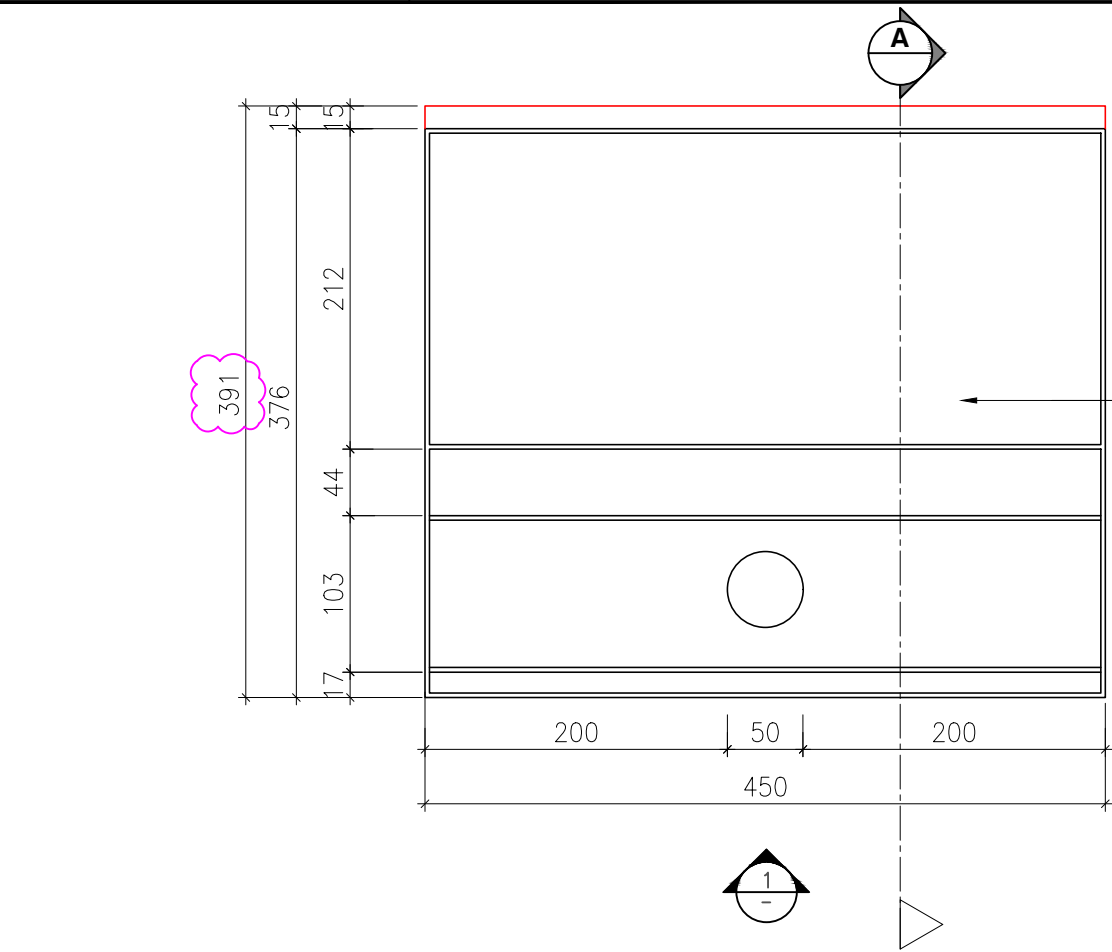

1 PLAN
SCALE 1:5

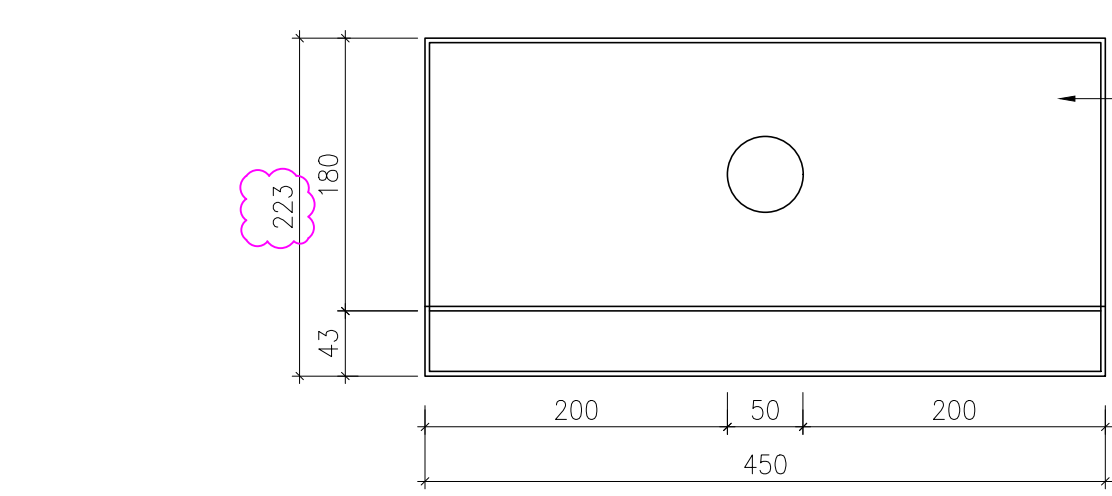


2 ELEVATION 1
SCALE 1:5

MAKEUP DRAWER IN
BLACK PAINT FIN;

MAKEUP DRAWER IN
BLACK PAINT FIN;

DRAWER RUNNER


SHELF WITH LED
LIGHT 6000K

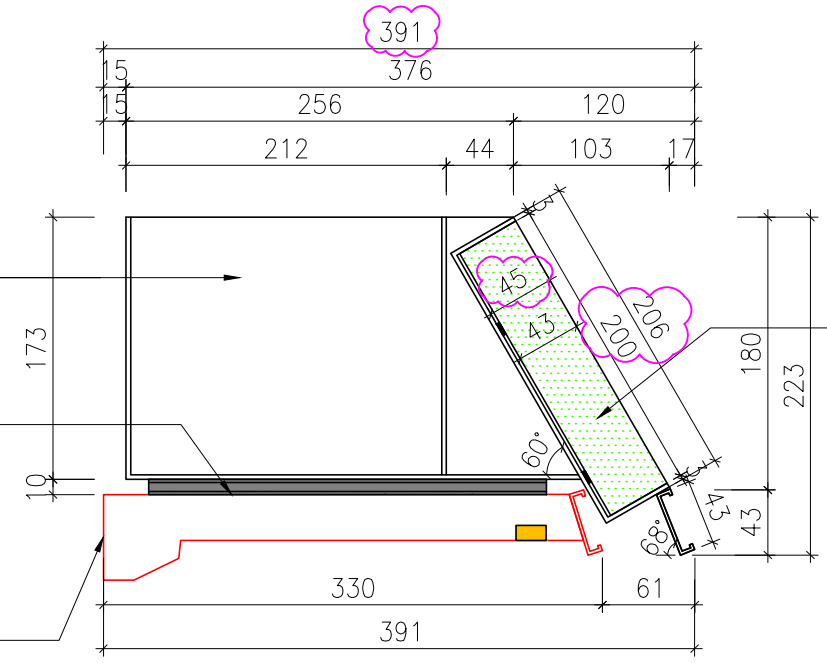


PLANOGRAM WITH
MAGNETS

3 SECTION A
SCALE 1:5

Rev	Date	Description
Client:		
Project:		
FRAN @ BUGIS+ (#01-04)		
Project Management:		
 Studio J Solutions Pte. Ltd. email : enquiries@studioj.sg web : www.studioj.sg Add : 7 Mandal Link #03-20 Mandal Connection Singapore 728653		
Design Consultant:		
Main Contractor:		
 Studio J Solutions Pte. Ltd. email : enquiries@studioj.sg web : www.studioj.sg Add : 7 Mandal Link #03-20 Mandal Connection Singapore 728653		
Mechanical & Electrical Consultant:		
Structural Engineer:		
General Notes:		
COPYRIGHT OF ALL DESIGNS AND DATA SHOWN IN THIS DRAWING IS RETAINED BY STUDIO J SOLUTION PTE.LTD. WRITTEN PERMISSION IS REQUIRED FOR ANY USE AND/OR REPRODUCTION. ALL RIGHTS, SPECIFICATIONS AND COPYRIGHTS ARE THE PROPERTY OF STUDIO J SOLUTION PTE.LTD. AND SHALL BE RETURNED ON COMPLETION OF WORKS. ALL MEASUREMENTS MUST BE CHECKED AT SITE BY THE CONTRACTOR AND NOTIFICATION TO BE MADE TO THE DESIGNER BEFORE COMMENCEMENT OF WORK IN THE EVENT OF ANY DISCREPANCIES ARISING FROM THE DRAWINGS. ALL DRAWINGS MUST BE READ IN CONJUNCTION WITH OTHER CONSULTANT DRAWINGS.		
Drawn :		
WILLIAM		
Checked:		
JF		
Approved:		
First submission date:		
Scale :		
A3 AS SHOWN		
Drawing Title:		
MAKEUP DRAWER GONDOLA		
Drawing Number:		
MD-G1		
Project Number:		
FRAN_BUGIS+_270726		

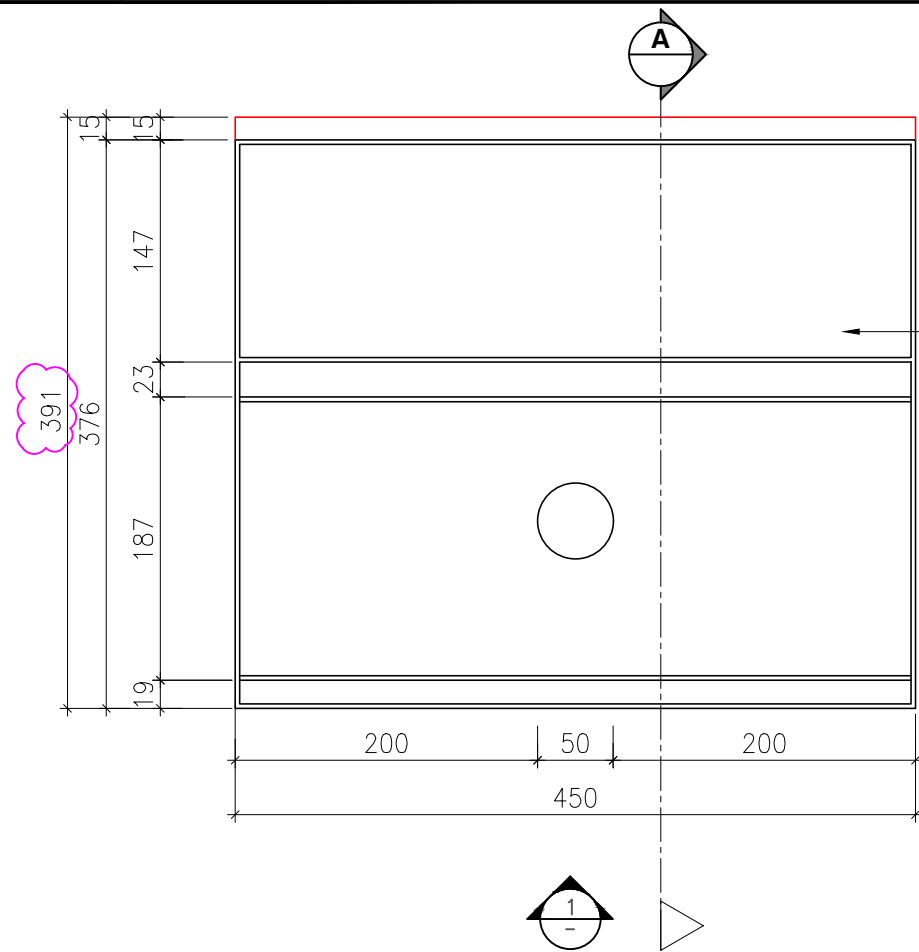

1 PLAN
SCALE 1:5

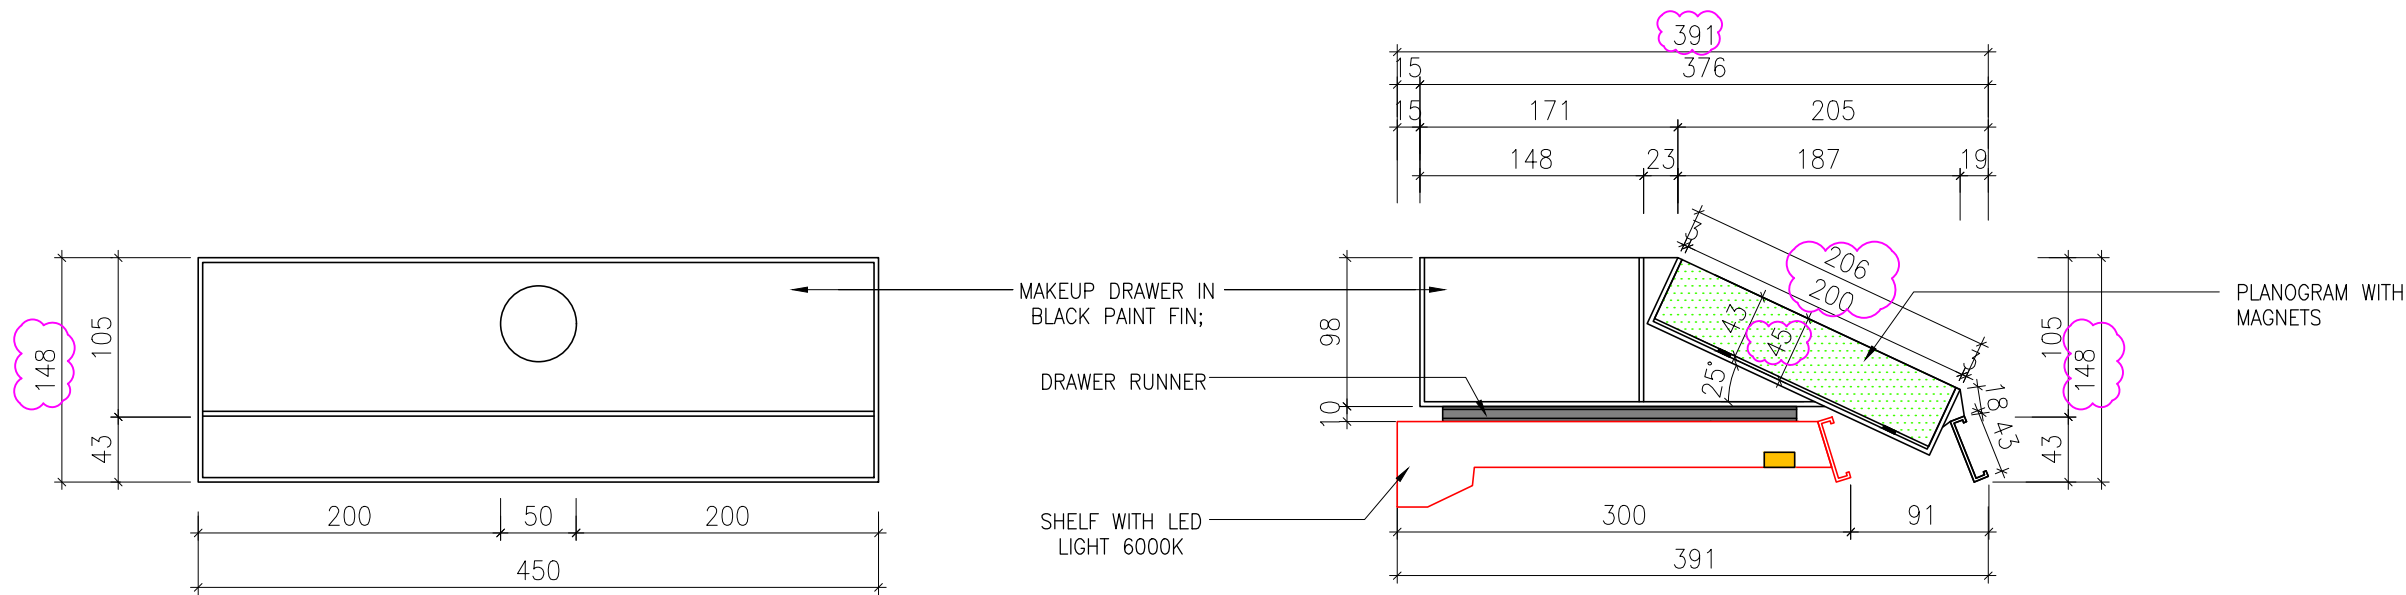

2 ELEVATION 1
SCALE 1:5

3 SECTION A
SCALE 1:5

Rev	Date	Description
Client:		
Project:		
FRAN @ BUGIS+ (#01-04)		
Project Management:		
 Studio J Solutions Pte. Ltd.		
email : enquiries@studioj.sg web : www.studioj.sg Add : 7 Mandal Link #03-20 Mandal Connection Singapore 728653		
Design Consultant:		
Main Contractor:		
 Studio J Solutions Pte. Ltd.		
email : enquiries@studioj.sg web : www.studioj.sg Add : 7 Mandal Link #03-20 Mandal Connection Singapore 728653		
Mechanical & Electrical Consultant:		
Structural Engineer:		
General Notes:		
COPYRIGHT OF ALL DESIGNS AND DATA SHOWN IN THIS DRAWING IS RETAINED BY STUDIO J SOLUTION PTE.LTD. WRITTEN PERMISSION IS REQUIRED FOR ANY USE AND/OR REPRODUCTION. ALL PRINTS, SPECIFICATIONS AND COPYRIGHTS ARE THE PROPERTY OF STUDIO J SOLUTION PTE.LTD. AND SHALL BE RETURNED ON COMPLETION OF WORKS. ALL MEASUREMENTS MUST BE CHECKED AT SITE BY THE CONTRACTOR AND NOTIFICATION TO BE MADE TO THE DESIGNER BEFORE COMMENCEMENT OF WORK IN THE EVENT OF ANY DISCREPANCIES ARISING FROM THE DRAWINGS. ALL DRAWINGS MUST BE READ IN CONJUNCTION WITH OTHER CONSULTANT DRAWINGS.		
Drawn :		
WILLIAM		
Checked:		
JF		
Approved:		
First submission date:		
Scale :		
A3 AS SHOWN		
Drawing Title:		
MAKEUP DRAWER GONDOLA		
Drawing Number:		
MD-G2		
Project Number:		
FRAN_BUGIS+_270726		