
AREA	SQ-M
TOTAL AREA	230

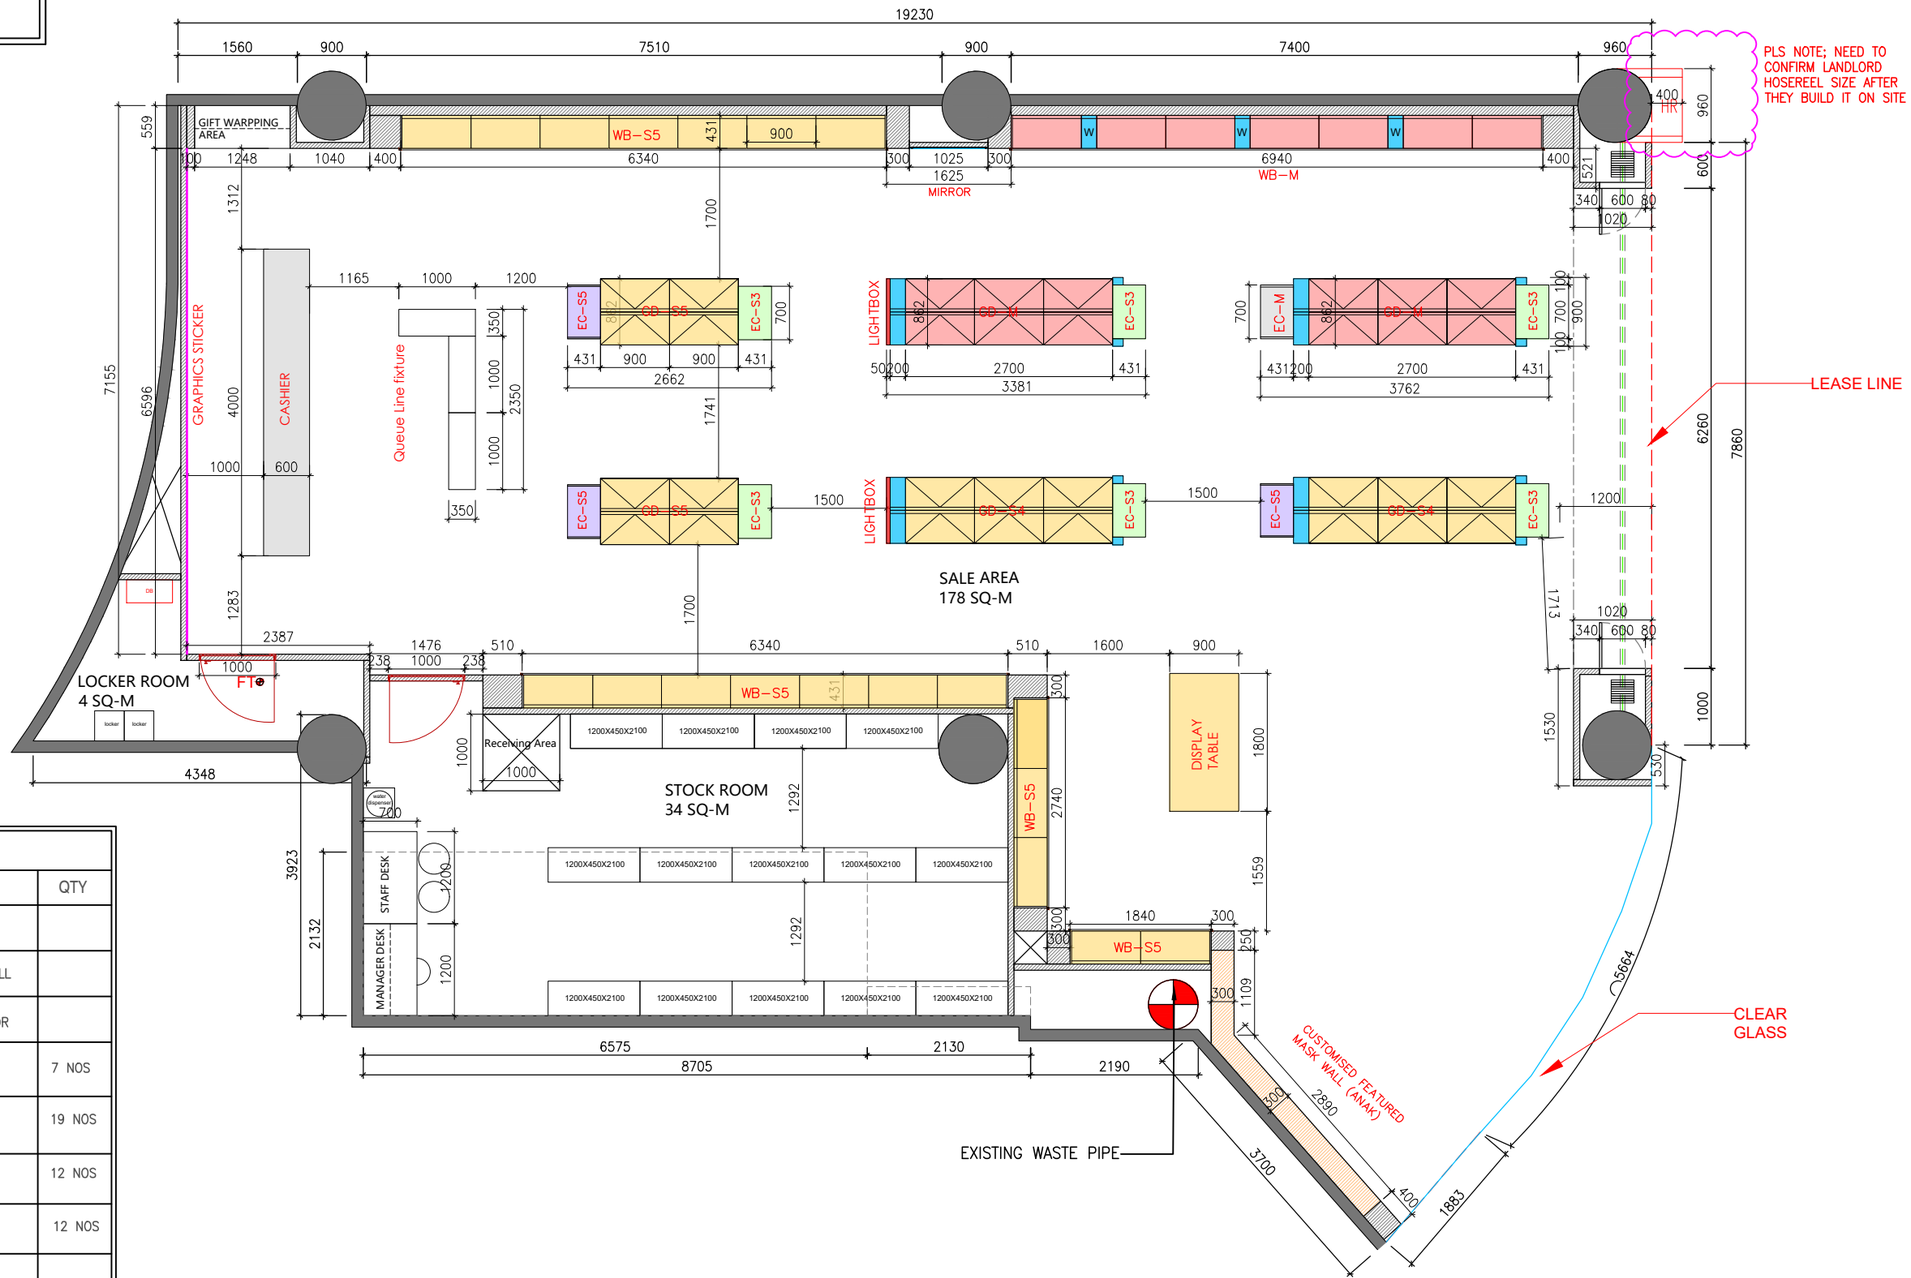

LEGEND:

SYMBOL	DESCRIPTION	QTY
	EXISTING STRUCTURE WALL	
	NEW BUILT–IN PARTITION WALL	
	BIFOLD POLYCARBONATE DOOR	
	MAKEUP WALLBAY	7 NOS
	STANDARD WALLBAY WITH 5 SHELVES	19 NOS
	MAKEUP GONDOLA	12 NOS
GD–S4	STANDARD GONDOLA (4 SHELVES)	12 NOS
GD–S5	STANDARD GONDOLA (5 SHELVES)	8 NOS
EC–M	MAKEUP ENDCAP (4 SHELVES)	1 NO
EC–S3	STANDARD ENDCAP (3 SHELVES) WITH L–SHAPE SIDE PANEL	6 NOS
EC–S5	STANDARD ENDCAP (5 SHELVES) WITH WHITE TRANSPARENT SIDE PANEL	3 NOS
	HYGIENE STATION	8 NOS
W	HYGIENE STATION FOR WALLBAY	3 NOS
	HYGIENE STATION MOUNTED ON L–SHAPE SIDE PANEL	8 NOS

STOCK ROOM	
RACKING	QTY
W1200xD450XH2100	14 NOS

01 FURNITURE PLAN

SCALE 1 : 80

Rev	Date	Description

Client:

Project :

FRAN @ BUGIS+

(#01-04)

Project Management:

Studio J Solutions Pte. Ltd

email : enquiries@studioj.sg
web : www.studioj.sg
Add : 7 Mandai Link
#03-20 Mandai Connection
Singapore 728653

Design Consultant:

Main Contractor:

Studio J Solutions Pte. Ltd

email : enquiries@studioj.sg
web : www.studioj.sg
Add : 7 Mandai Link
#03-20 Mandai Connection
Singapore 728653

Mechnical & Electrical Consultant:

Structural Engineer:

General Notes:

COPYRIGHT OF ALL DESIGNS AND DATA SHOWN IN THIS DRAWING IS RETAINED BY STUDIO J SOLUTION PTE.LTD. WRITTEN PERMISSION IS REQUIRED FOR ANY USE AND/OR REPRODUCTION. ALL PRINTS, SPECIFICATIONS AND COPYRIGHTS ARE THE PROPERTY OF STUDIO J SOLUTION PTE.LTD AND SHALL BE RETURNED ON COMPLETION OF WORKS. ALL MEASUREMENTS MUST BE CHECKED AT SITE BY THE CONTRACTOR AND NOTIFICATION TO BE MADE TO THE DESIGNER BEFORE COMMENCEMENT OF WORK IN THE EVENT OF ANY DISCREPANCIES ARISING FROM THE DRAWINGS. ALL DRAWINGS MUST BE READ IN CONJUNCTION WITH OTHER CONSULTANT DRAWINGS.

Drawn : WILLIAM

Checked: JF

Approved:

First submission date:

Scale : A3 AS SHOWN

Drawing Title:

FURNITURE PLAN

Drawing Number:

PL–01

Project Number:

FRAN_BUGIS+_020726